# OBJEKT D - PŮDORYS 1NP - KOORDINAČNÍ VÝKRES
1:50

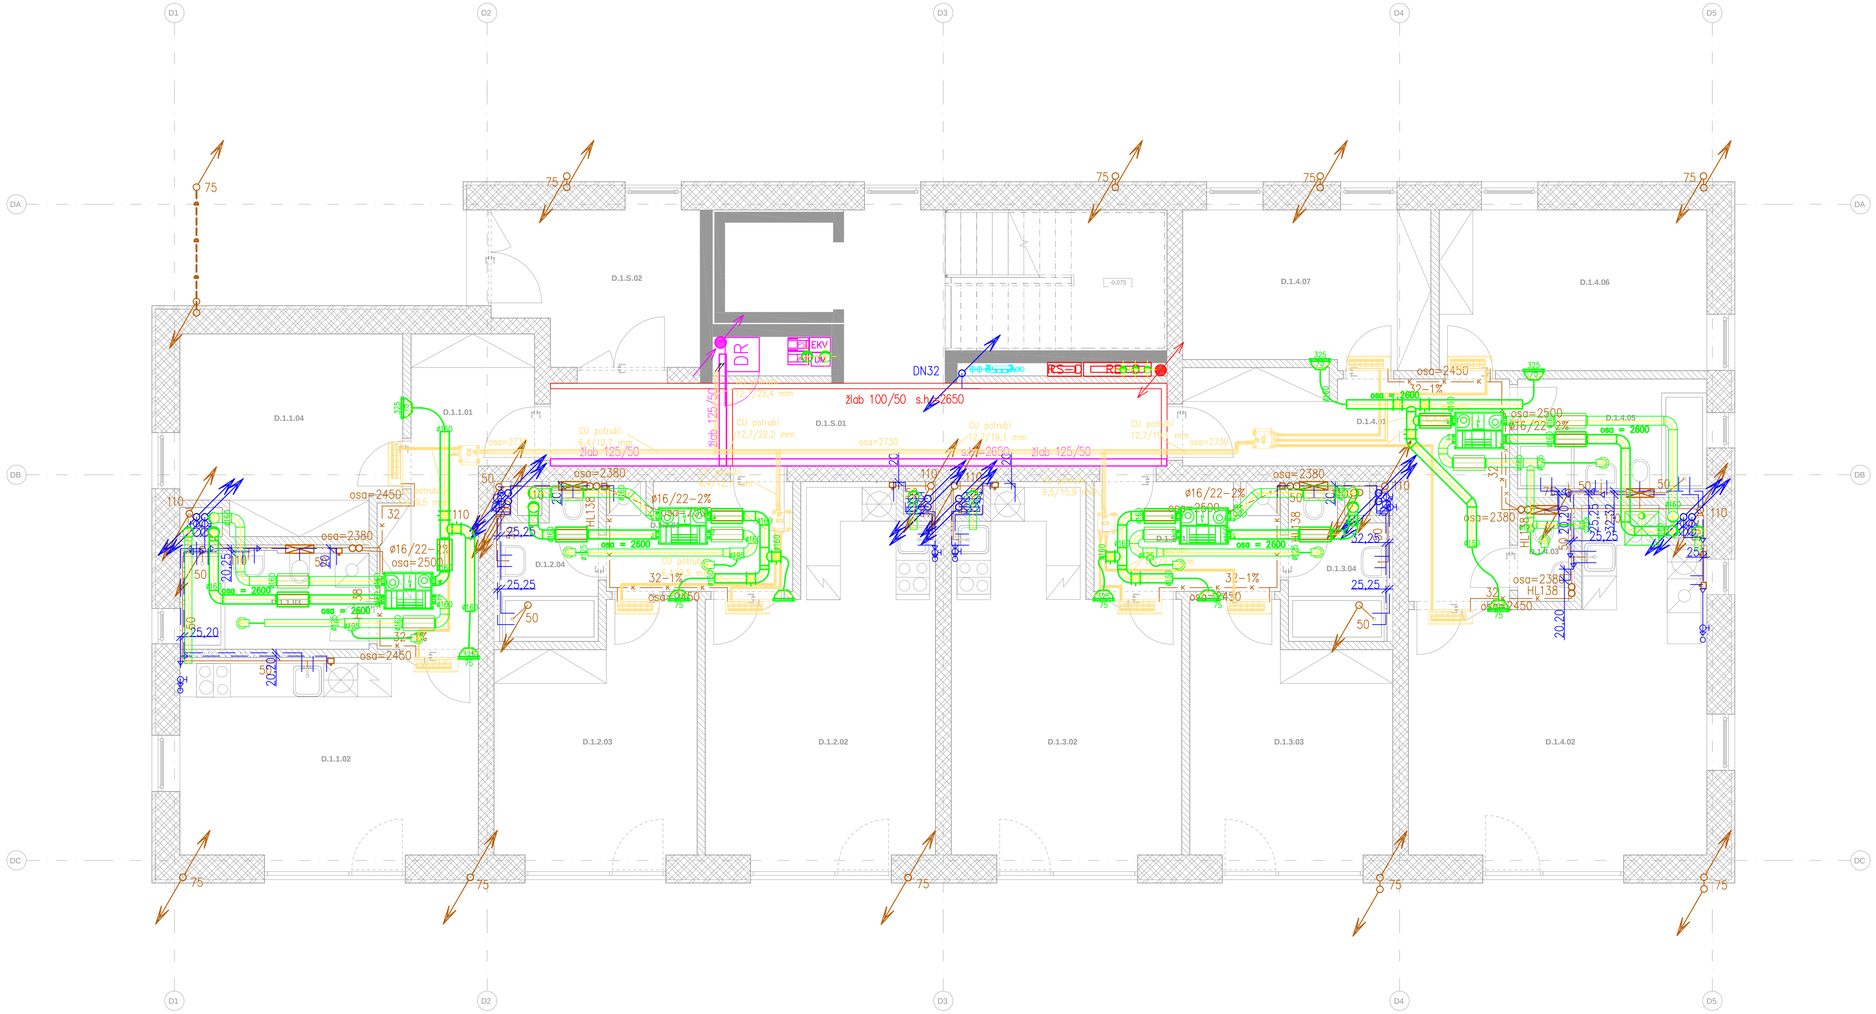


## Legenda rozvodů a zařízení

- vzduchotechnika
- chlazení
- vytápění
- vodovod (horizontální rozvody v bytech jsou vedeny v podlaze nebo max. ve výšce 1,3m)
- kanalizace
- silnoproud
- slaboproudy

## Tabulka místností 1.NP

| Č. místnosti | Název | Plocha |
|---|---|---|
| D.1.1.01 | CHODBA | 11 m² |
| D.1.1.02 | OBÝVACÍ POKOJ + KK | 19 m² |
| D.1.1.03 | KOUPELNA | 6 m² |
| D.1.1.04 | POKOJ | 13 m² |
| D.1.2.01 | CHODBA | 8 m² |
| D.1.2.02 | OBÝVACÍ POKOJ + KK | 23 m² |
| D.1.2.03 | POKOJ | 15 m² |
| D.1.2.04 | KOUPELNA | 4 m² |
| D.1.3.01 | CHODBA | 8 m² |
| D.1.3.02 | OBÝVACÍ POKOJ + KK | 23 m² |
| D.1.3.03 | POKOJ | 15 m² |
| D.1.3.04 | KOUPELNA | 5 m² |
| D.1.4.01 | CHODBA | 14 m² |
| D.1.4.02 | OBÝVACÍ POKOJ + KK | 27 m² |
| D.1.4.03 | WC | 2 m² |
| D.1.4.05 | KOUPELNA | 7 m² |
| D.1.4.06 | POKOJ | 14 m² |
| D.1.4.07 | POKOJ | 12 m² |
| D.1.S.01 | ZÁDVEŘÍ | 10 m² |
| D.1.S.02 | SPOLEČNÁ CHODBA | 16 m² |
| D.1.S.03 | SPOLEČNÁ CHODBA | 5 m² |

*projekt / project* — *číslo zakázky / project number:* 185-01

BYTOVÝ SOUBOR LIBUŠE

*stupeň dokumentace / design stage*

**DOKUMENTACE PRO PROVEDENÍ STAVBY** — **DPS**
DETAIL DESIGN DOCUMENTATION — DDD

*klient / client*

VELTON REAL ESTATE
Na Strži 2102/61a
140 00, Praha 4 - Krč

*architekt / architect*

adns architekti
A.D.N.S. architekti s.r.o.
Na Příkopě 853/12
110 00 Praha 1 - Nové Město

*generální projektant / general designer*

ABMV WORLD
ABMV world s.r.o.
Prosecká 527/24
180 00 Praha 8

*projektant / designer*

ABMV WORLD
ABMV world s.r.o.
Prosecká 527/24
180 00 Praha 8

*odpovědný projektant / designer*: Ing. arch. Zdeněk Vávra

*vypracoval / drawn by*: Štěpán Šustr

*kontroloval / checked by*: Ing. Marek Veselý

| *revize / revision* | *popis / description* | *datum / date* |
|---|---|---|
| *číslo* | *stručný popis revize* | *datum vydání revize* |

*část dokumentace / documentation part*

D | DOKUMENTACE OBJEKTŮ A TECHNICKÝCH A TECHNOLOGICKÝCH ZAŘÍZENÍ

*stavební objekt / building object*

SO01 | BYTOVÝ DŮM

*profesní díl / specialist part*

140 | ARCHITEKTONICKO-STAVEBNÍ ŘEŠENÍ - OBJEKT D, NADZEMNÍ ČÁST

*název výkresu / drawing title*

OBJEKT D - KOORDINAČNÍ VÝKRES 1.NP

| *datum revize 00 / revision date 00* | *měřítko / scale* | *počet A4 / A4 count* | *paré* |
|---|---|---|---|
| 15.09.2021 | 1:50 | 10 x A4 | |

±0.000 = 303,800 m n. m.
výškový systém: Bpv
souřadný systém: JTSK

*číslo výkresu / sheet number*: 9410

*kód výkresu / sheet code*: 185D1_DPS_D_SO01_140_9410_R00