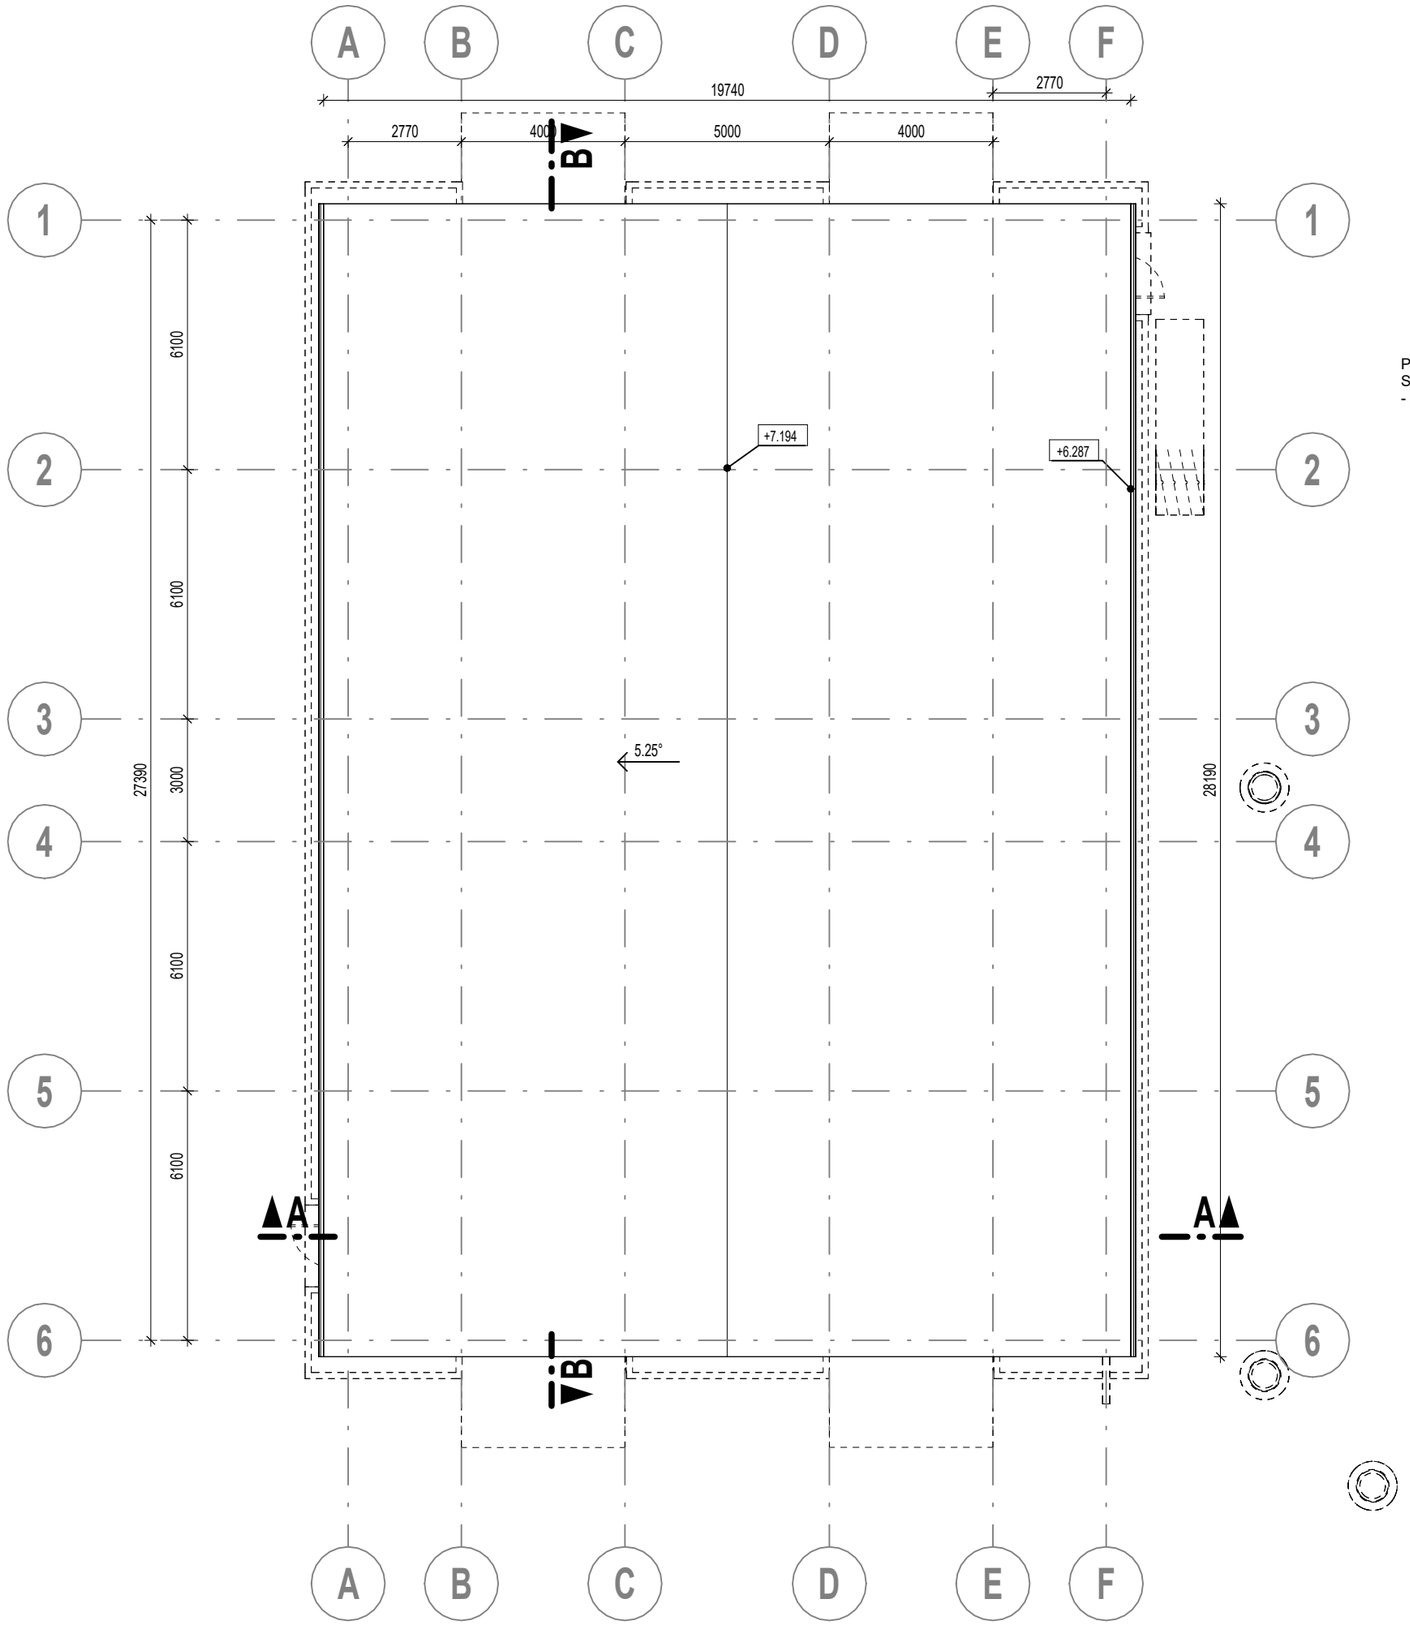


Poznámka:
STŘEŠNÍ PLÁŠŤ
- požadovaná pož. odolnost EI 15 DP1 + $B_{roof}$

# HALA HRADEC KRÁLOVÉ

Vážní 857, 50003 Hradec Králové - Slezské Předměstí

STUPEŇ PROJEKTU +0,000 = +234,690 mnm Bpv

**DOKUMENTACE PRO POVOLENÍ ZÁM ĚRU (DPZ)**


ODPOVĚDNÝ PROJEKTANT

Ing.arch. Jakub Volka, ČKA 03947
733 575 363, jakub.volka@basepoint.cz


AUTORIZOVANÝ ARCHITEKT (A1) ING. ARCH. JAKUB VOLKA ČKA 03 947 ČESKÁ REPUBLIKA

Digitálně podepsal Ing. arch. Jakub Volka
Datum: 2025.10.30 14:18:37 +01'00'


VYPRACOVAL

Ing. arch. Jakub Volka
Anna Abrahámová
Kristián Pócsik


INVESTOR

SOLAR DISPOREC s.r.o. , Praha IČO 19546220
Malostranské náměstí 5/28, Malá Strana (Praha 1), 118 00 Praha

DÍL

D

ČÁST DOKUMENTACE

D.1.1.2

OBSAH VÝKRESU

## PŮDORYS STŘECHY

| MĚŘÍTKO | FORMÁT |
|---|---|
| 1:150 | 2 X A4 |
| **DATUM** | **1.VYDÁNÍ** |
| 07/2025 | 07/2025 |

| STUPEŇ | DÍL | ČÁST | ČÍSLO | PŘÍLOHA | REVIZE |
|---|---|---|---|---|---|
| DPZ | D-S001 | ARS | A102 | STR | R00 |


ZPRACOVATEL ČÁSTI

**basepoint s.r.o.**
V Benátkách 2350/6
149 00, praha 4
www.basepoint.cz

GENERÁLNÍ PROJEKTANT

**basepoint s.r.o.**
V Benátkách 2350/6
149 00, praha 4
www.basepoint.cz