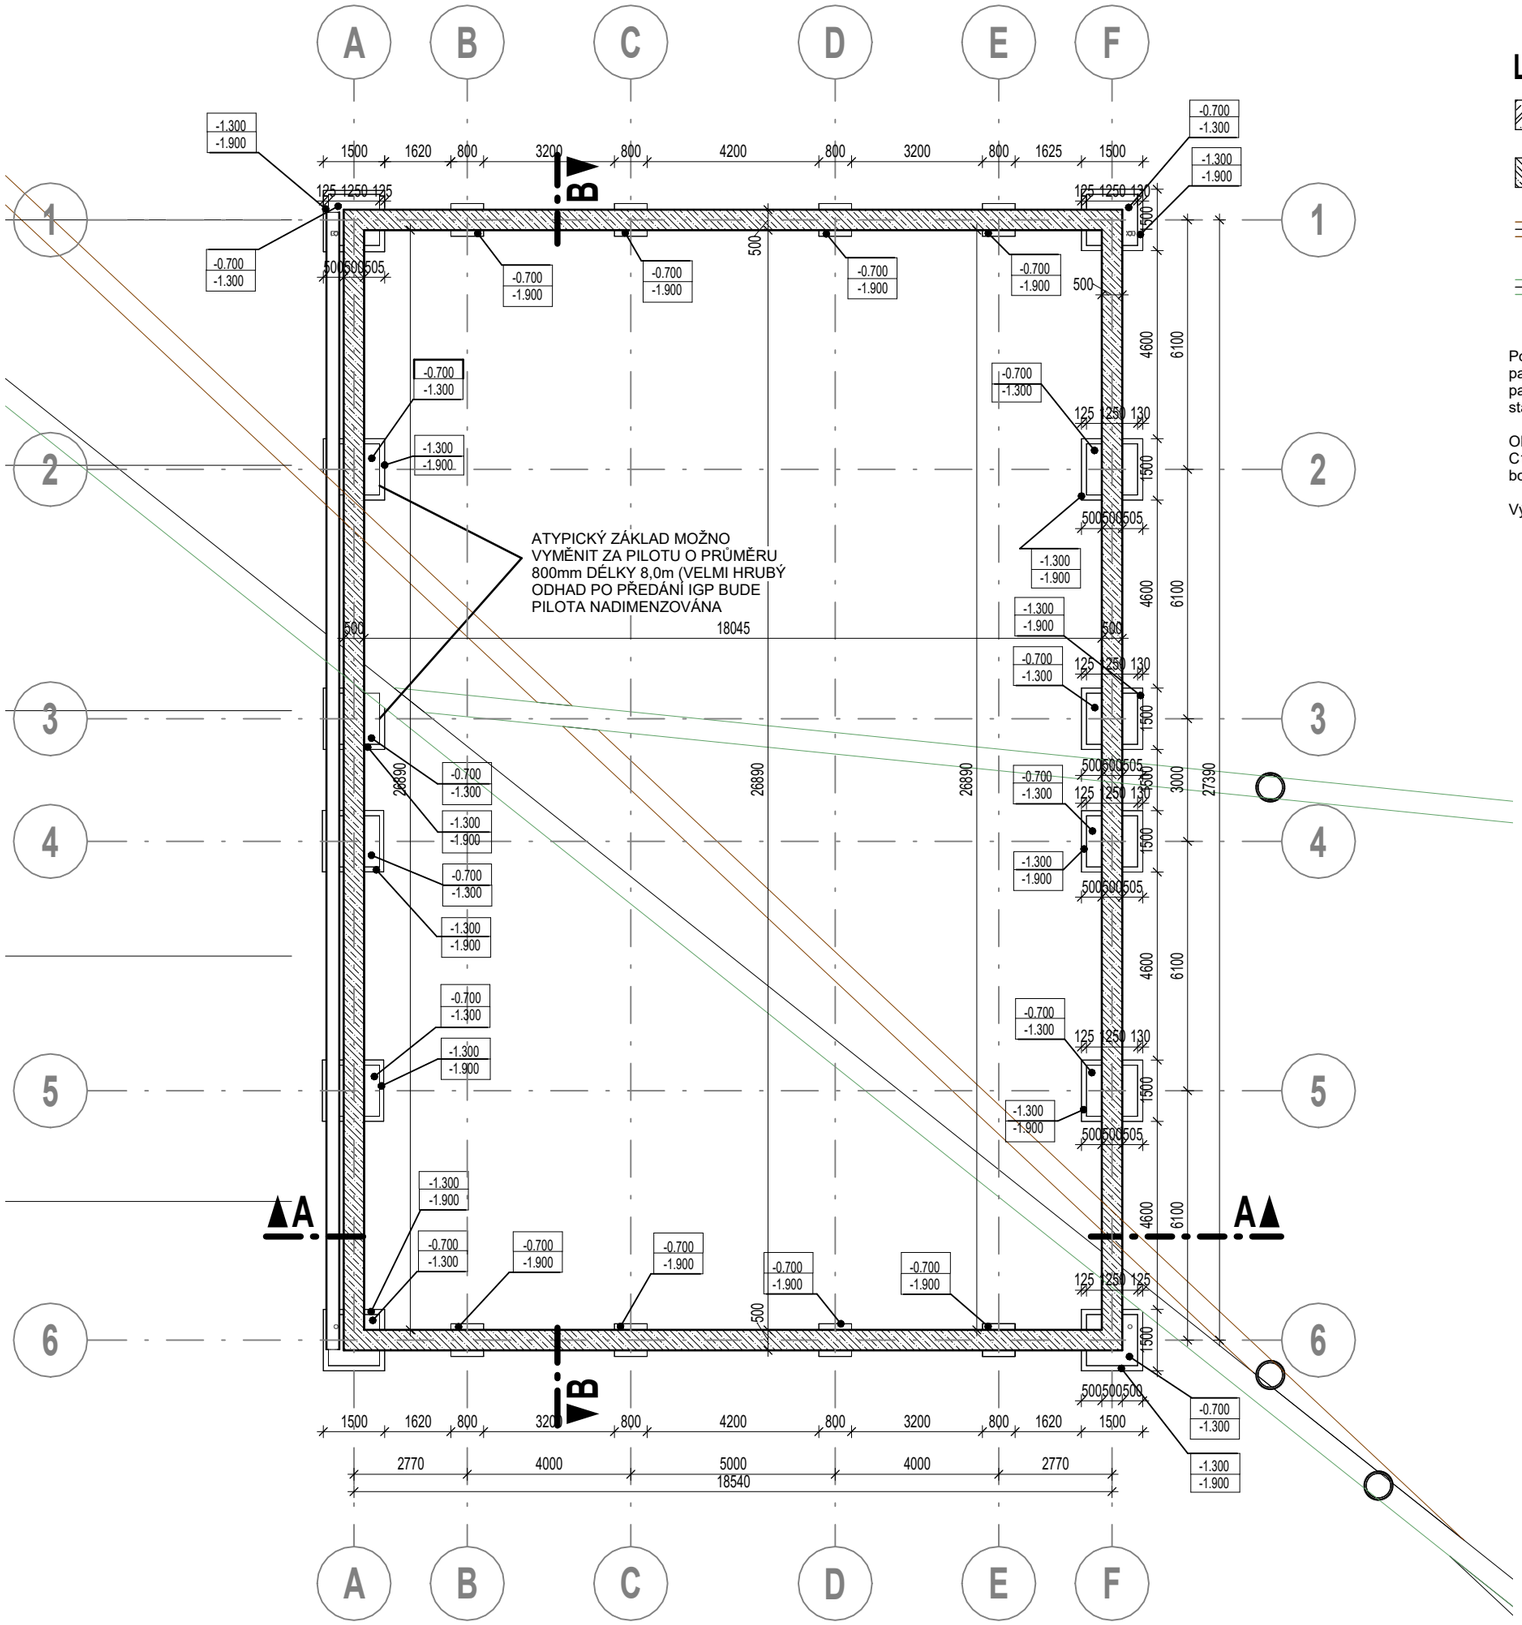

LEGENDA MATERIÁLŮ:

- Železobeton
- Beton prostý
- Stávající areálová splašková kan., p ředpoklad DN300
- Stávající areálová deš ťová kan., předpoklad DN300

Pozn.: V případě křížení potrubí se základovými pasy nebo patkami bude objekt založen na excentrických základových patkách, případně na pilotách. Varianta bude zvolena na základě statického posouzení a geologického průzkumu.

Obetonování trubek min. 100mm z každé strany, C16/20 nebo C25/30 (dle statika), v případě plast. potr. zasypat boky pískem/šterkopískem a betonovat až poté

Výkres základů převzatý od statika

HALA HRADEC KRÁLOVÉ

Vážní 857, 50003 Hradec Králové - Slezské Předměstí

STUPEŇ PROJEKTU +0,000 = +234,690 mnm Bpv

DOKUMENTACE PRO POVOLENÍ ZÁM ĚRU (DPZ)

ODPOVĚDNÝ PROJEKTANT

Ing.arch. Jakub Volka, ČKA 03947
733 575 363, jakub.volka@basepoint.cz

AUTORIZOVANÝ ARCHITEKT (A1) ING. ARCH. JAKUB VOLKA ČKA 03 947 ČESKÁ REPUBLIKA

Digitálně podepsal Ing. arch. Jakub Volka
Datum: 2025.10.30 14:21:18 +01'00'

VYPRACOVAL

Ing. arch. Jakub Volka
Anna Abrahámová
Kristián Pócsik

INVESTOR

SOLAR DISPOREC s.r.o. , Praha IČO 19546220
Malostranské náměstí 5/28, Malá Strana (Praha 1), 118 00 Praha

DÍL

D

ČÁST DOKUMENTACE

D.1.1.1

OBSAH VÝKRESU

ZÁKLADY

MĚŘÍTKO	FORMÁT
1:150	2 X A4
DATUM	1.VYDÁNÍ
07/2025	07/2025

STUPEŇ	DÍL	ČÁST	ČÍSLO	PŘÍLOHA	REVIZE
DPZ	D-S001	ARS	A105	ZAK	R00

ZPRACOVATEL ČÁSTI

basepoint s.r.o.
V Benátkách 2350/6
149 00, praha 4
www.basepoint.cz

GENERÁLNÍ PROJEKTANT

basepoint s.r.o.
V Benátkách 2350/6
149 00, praha 4
www.basepoint.cz