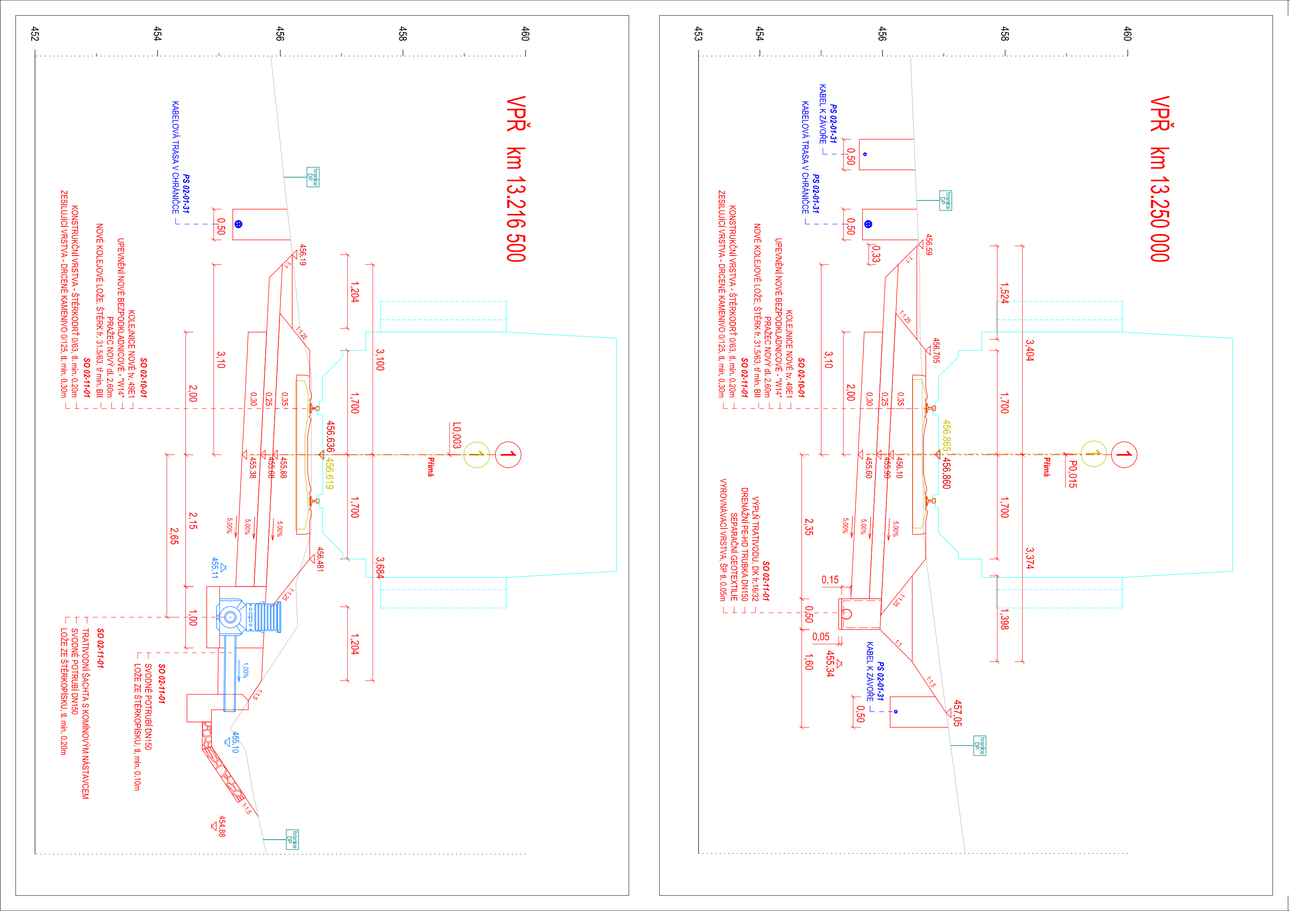


Jiná ověření:

Paré:

Orientační schéma:

Razítko oprávněné osoby:

Ing. ONDŘEJ VRÁNEK autorizovaný inženýr pro dopravní stavby ČKAIT - 0402684

Podpis:

Datum:

Revize:	Datum:	Popis:	Kontroloval:
000	18.06.2025	Definitivní odevzdání dokumentace	Ing. Ondřej Vránek

Stavebník/Investor:	**Správa železnic, státní organizace**
Adresa:	**Dlážděná 1003/7, 110 00 Praha 1**
Zástupce investora:	**Stavební správa západ**
Adresa:	**Sokolovská 1955/278, 190 00 Praha 9**

SPRÁVA ŽELEZNIC

Zhotovitel díla:	**VIAMONT Projekt, s.r.o.**
Adresa:	Českobrodská 628, 190 11 Praha 9 – Běchovice
Kontakt:	T: +420 477 070 481 E: info@viamontprojekt.cz
Zhotovitel části/objektu:	
Adresa:	
Kontakt:	
Hlavní projektant (HIP):	**Ing. Ondřej Vránek**
Specialista:	**Ing. Ondřej Vránek**

VIAMONT PROJEKT

Název stavby/akce:	**Výstavba PZS na přejezdu P137 v km 13,250 na trati Sokolov – Kraslice**		Označení investora: **S632300086**
			Zakázka: **15/2024**
Název části:	Kolejový svršek a spodek		Označení části: **D.2.1.1**
Název objektu/dílčí části:	**Železniční přejezd v km 13,250 (P137), železniční svršek a spodek**		Označení objektu/komplexu: **SK 02-00-02**
Název přílohy:	Vzorový příčný řez		Číslo přílohy (typ/pořadí): **2. 003**
Odpovědný projektant: Ing. Ondřej Vránek	Zpracovatel přílohy: Ing. Ondřej Vránek	Měřítko: 1:50 Formáty: 4xA4	Stupeň dokumentace: **PDPS**
Kraj: Karlovarský	Katastrální území: Viz textová část	TUDU: Viz. textová část	Smluvní datum zpracování: **18.06.2025**

Označení investora	Stupeň dokumentace	Část	Objekt	Profibranž	Příloha	Pořadí
S 6 3 2 3 0 0 8 6	- P D P S -	D 2 1 0 1	- S K 0 2 0 0 0 2 -	X X	- 2	- 0 0 3 - 0 0 0

(Prostor pro další informace)