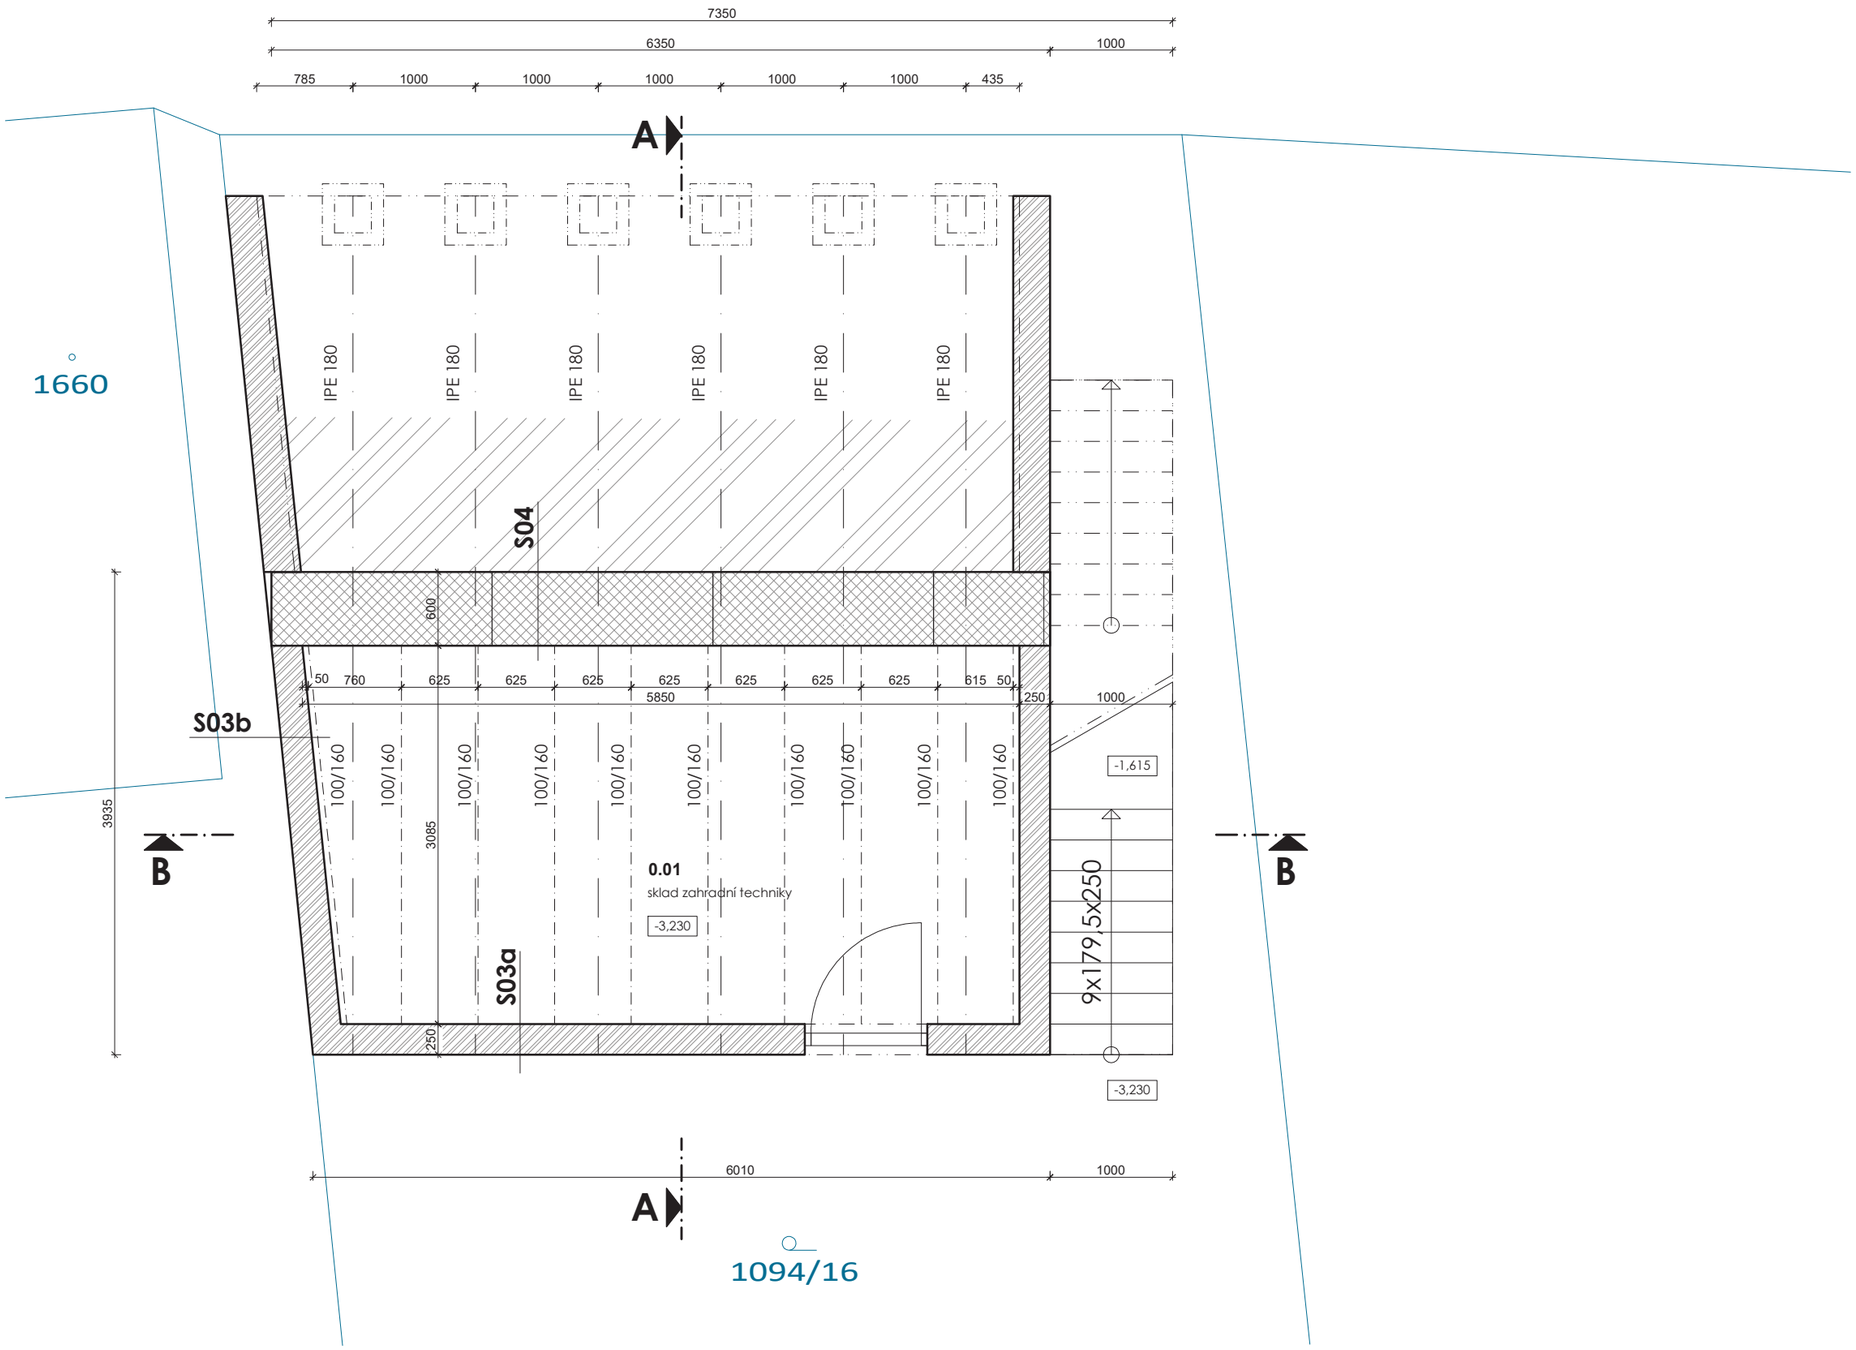

LEGENDA MÍSTNOSTÍ:

č. m.	název místnosti	podlaha	strop	stěny	plocha [m²]
0.01	sklad zahradní technicky	beton. dlažba			17,60

LEGENDA MATERIÁLU:

- obvodové nosné zdivo - betonové tvárnice
- ocelové konstrukce
- železobeton
- prostý beton
- betonové prefabrikované bloky
- tepelná izolace - XPS
- štěrkopískový násyp zhutněný na 0,2 MPa / násyp
- rostlý terén
- dřevěné konstrukce
- tepelná izolace - minerální vata/EPS *(viz. skladby konstrukcí)*
- ocelová konstrukce

SKLADBY KONSTRUKCÍ

S01 podlaha sklad
- betonová dlažba 50 mm
- kladecí vrstva - kamenná drf 4-8 mm 40 mm
- podkladní nosná vrstva - kamenná drf 4-8 mm 150 mm
- zhutněná zemní pláň (30 MPa)

S02 stropní konstrukce
- pojezdový ocelový pororošt 50 mm
- nosná ocelová konstrukce - ocel. nosníky 180 mm
- hydroizolační fólie
- záklop z dřevěných prken 20 mm
- dřevěné nosné trámy - KVH 100/160 160 mm

S03a obvodová stěna pod úrovní terénu
- povrch surový bez omítky
- obvodová stěna (dle legendy materiálů)
  - -- betonové tvárnice ztraceného bednění 250mm
- asfaltová penetrace
- 2x hydroizolační a protiradonový pás z modif. asfaltu 2x4mm
- drenážní vrstva - nopová folie 20mm

S03b obvodová stěna nad úrovní terénu
- povrch surový bez omítky
- obvodová stěna (dle legendy materiálů)
  - -- betonové tvárnice ztraceného bednění 250mm
- povrch surový bez omítky

S04 opěrná stěna
- povrch surový bez omítky
- opěrná stěna (dle legendy materiálů)
  - -- betonové prefa bloky usazené na zámek 600mm
- asfaltová penetrace
- 2x hydroizolační a protiradonový pás z modif. asfaltu 2x4mm
- drenážní vrstva - nopová folie 20mm

S05 schodiště
- schod z betonového prefa bloku
- kladecí vrstva ze zavlhlého betonu
- podkladní betonová deska
- zhutněná zemní pláň

výškový systém balt po vyrovnání
± 0,000 = +673,30 m.n.m.

revize	datum	popis
02		
01	02/2026	úprava statického řešení
00	09/2025	vydání dokumentace

Zahradní sklad a přístupové schodiště k RD

č.p. 733, Jáchymov,

parc. č. 1094/16, st.1022, k.ú. Jáchymov [656437]

razítko/podpis
autorizovaný projektant

Ing. arch. Marek Smolka
tel.: +420 732 618 505, email: smolka@smasharch.cz
autorizace: 05394

Digitálně podepsal Ing. arch. Marek Smolka
Datum: 2026.02.05 11:42:52 +01'00'

paré

investor
Volný Jindřich Mgr.
Fibichova 733, 36251 Jáchymov

zpracovatel projektové dokumentace/generální projektant
SMASH architekti s.r.o.
Vodňanského 1008/2, Břevnov, 169 00 Praha 6
IČO: 17666902

projektový stupeň
dokumentace pro povolení záměru

část
C Situační výkresy

projektant části
Ing. arch. Marek Smolka
tel.: +420 732 618 505, email: smolka@smasharch.cz

název výkresu
Půdorys suterénu / skladu

datum	měřítko	číslo výkresu
09/2025	1:50	**D.1.1.02**