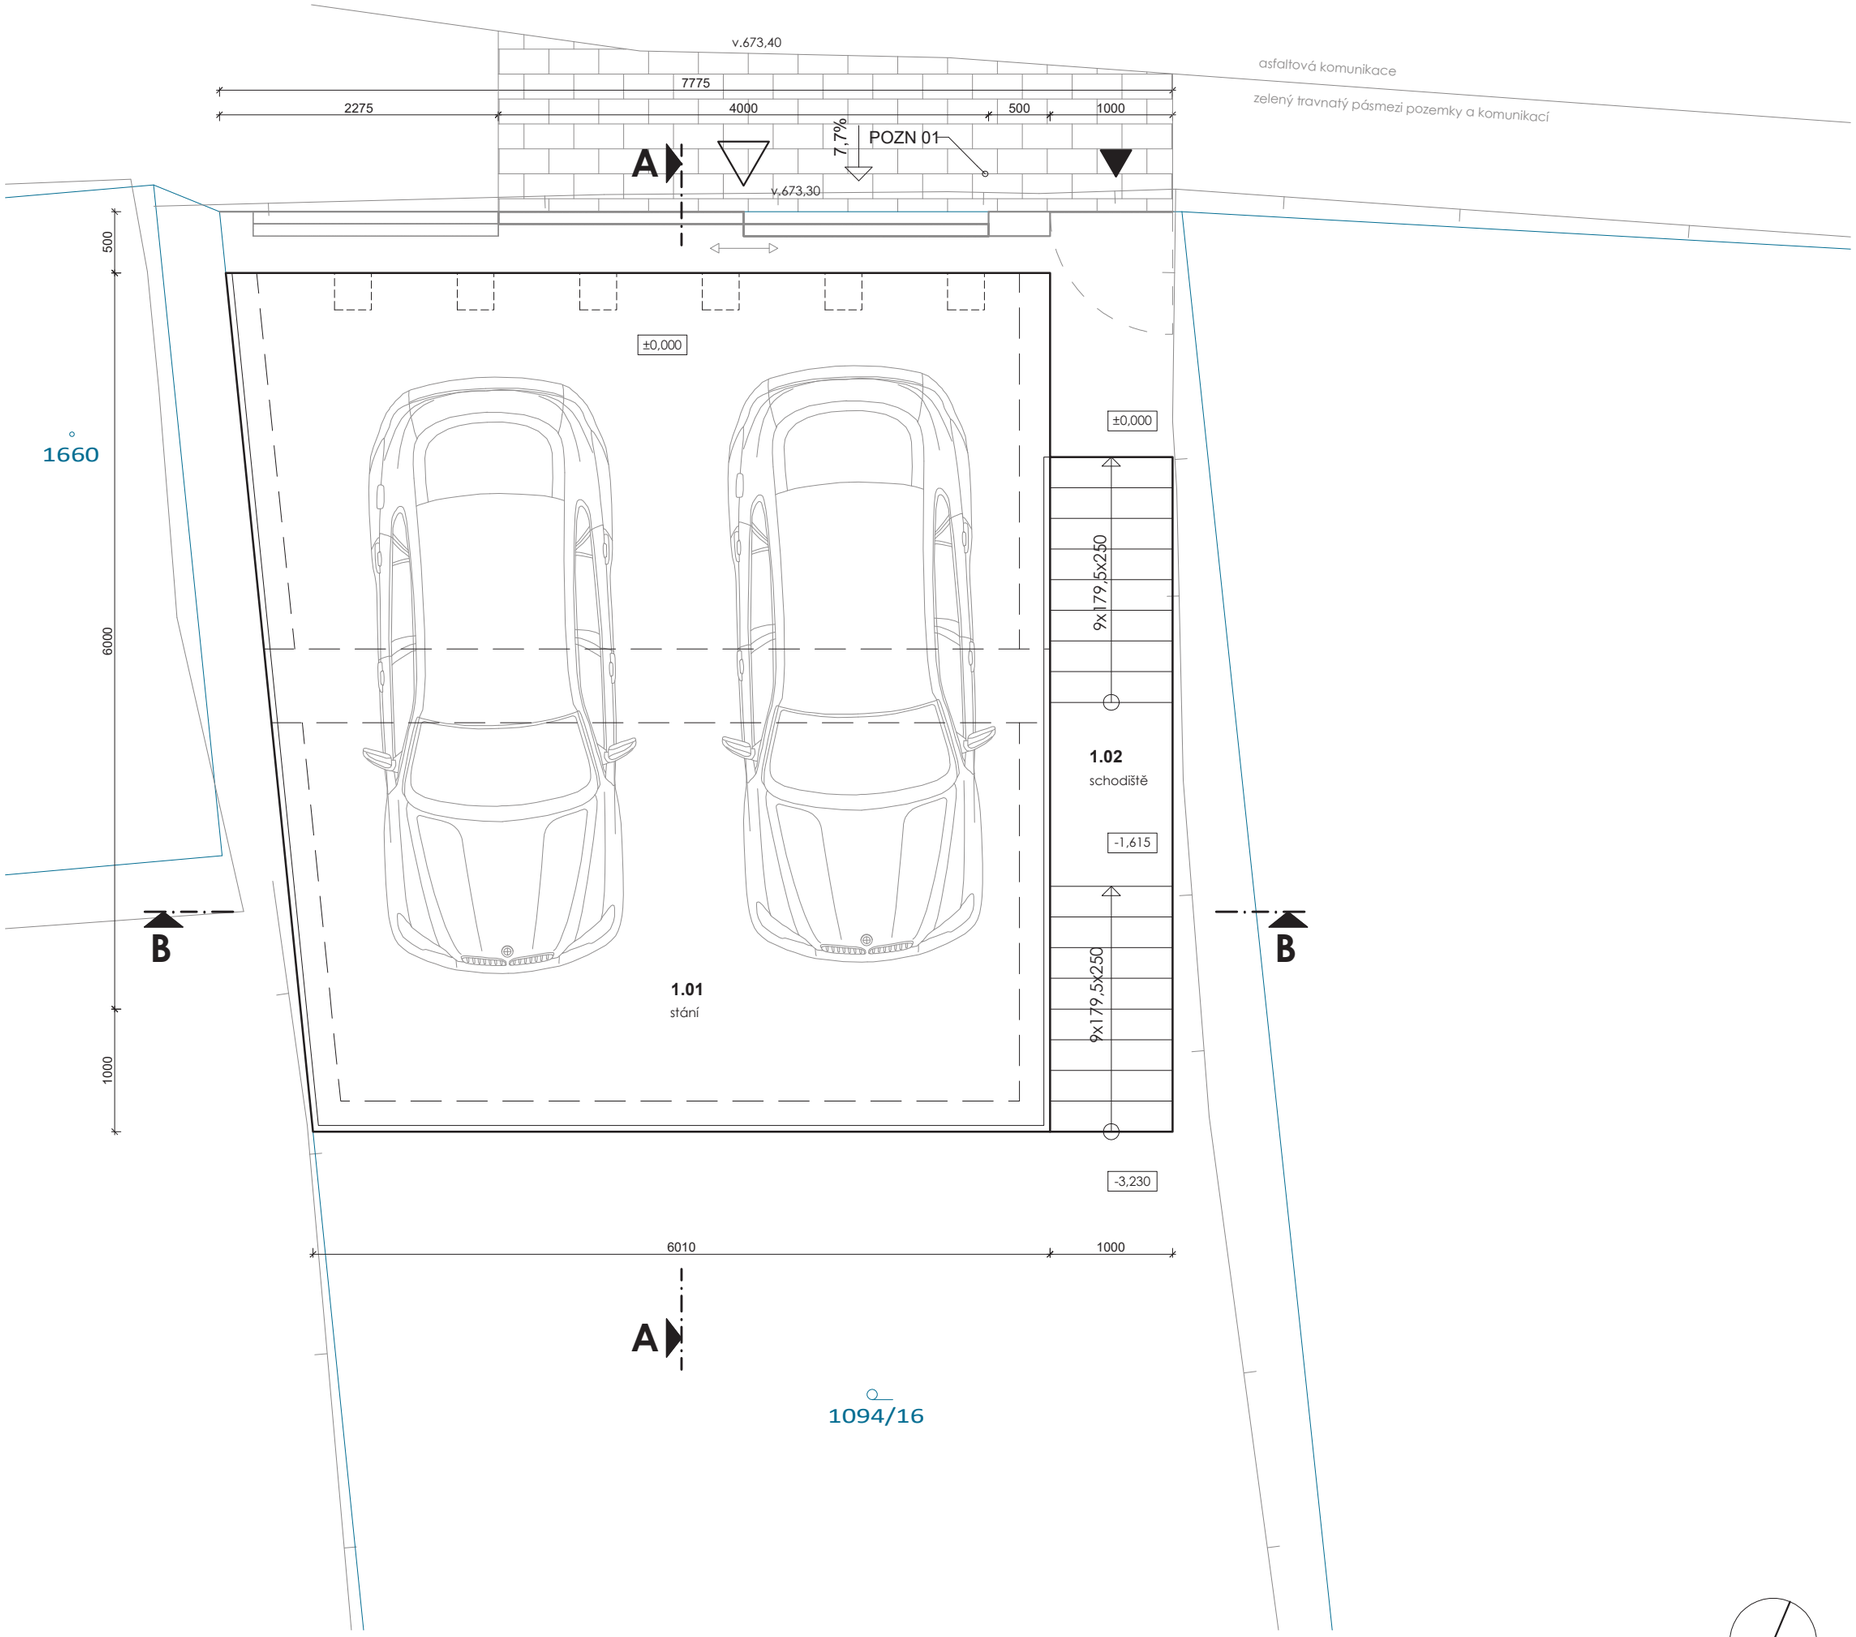

LEGENDA MÍSTNOSTÍ:

č. m.	název místnosti	podlaha	strop	stěny	plocha [m²]
1.01	stání	porost			44,60
1.02	schodiště	beton			5,50

LEGENDA

- navrhovaný objekt parkovacího stání
- hranice podzemní části navrhované budovy
- katastrální mapa
- ploty
- vstup / vjezd
- navrhovaný plot a vjezd / vstup
- napojení na komunikaci - dlážděná plocha - betonová dlažba

POZNÁMKY

POZN. 01 zpevněná plocha napojení na komunikaci bude provedena z hladké betonové dlažby. Plocha bude vyspádována směrem na pozemek investora. Výška napojení na komunikaci je cca 763,4 m, výška stání a vjedzu na hraně pozemku bude cca 763,3m. Spád bude proměnný, dle výšky stoupající komunikace, cca 7-9 %.

revize	datum	popis
02	02/2026	úprava statického řešení
01	10/2025	úpřesnění napojení na komunikaci
00	09/2025	vydání dokumentace

Zahradní sklad a přístupové schodiště k RD

č.p. 733, Jáchymov,

parc. č. 1094/16, st.1022, k.ú. Jáchymov [656437]

razítko/podpis
autorizovaný projektant

Ing. arch. Marek Smolka
tel.: +420 732 618 505, email: smolka@smasharch.cz
autorizace: 05394

AUTORIZOVANÝ ARCHITEKT Ing. arch. Marek Smolka ČKA 05 394 ČESKÁ REPUBLIKA

Digitálně podepsal Ing. arch. Marek Smolka
Datum: 2026.02.05 11:39:33 +01'00'

paré

investor
Volný Jindřich Mgr.
Fibichova 733, 36251 Jáchymov

zpracovatel projektové dokumentace/generální projektant
SMASH architekti s.r.o.
Vodňanského 1008/2, Břevnov, 169 00 Praha 6
IČO: 17666902

projektový stupeň
dokumentace pro povolení záměru

část
C Situační výkresy

projektant části
Ing. arch. Marek Smolka
tel.: +420 732 618 505, email: smolka@smasharch.cz

výškový systém balt po vyrovnání
± 0,000 = +673,30 m.n.m.

název výkresu
Půdorys střechy

datum	měřítko	číslo výkresu
09/2025	1:50	**D.1.1.01**