


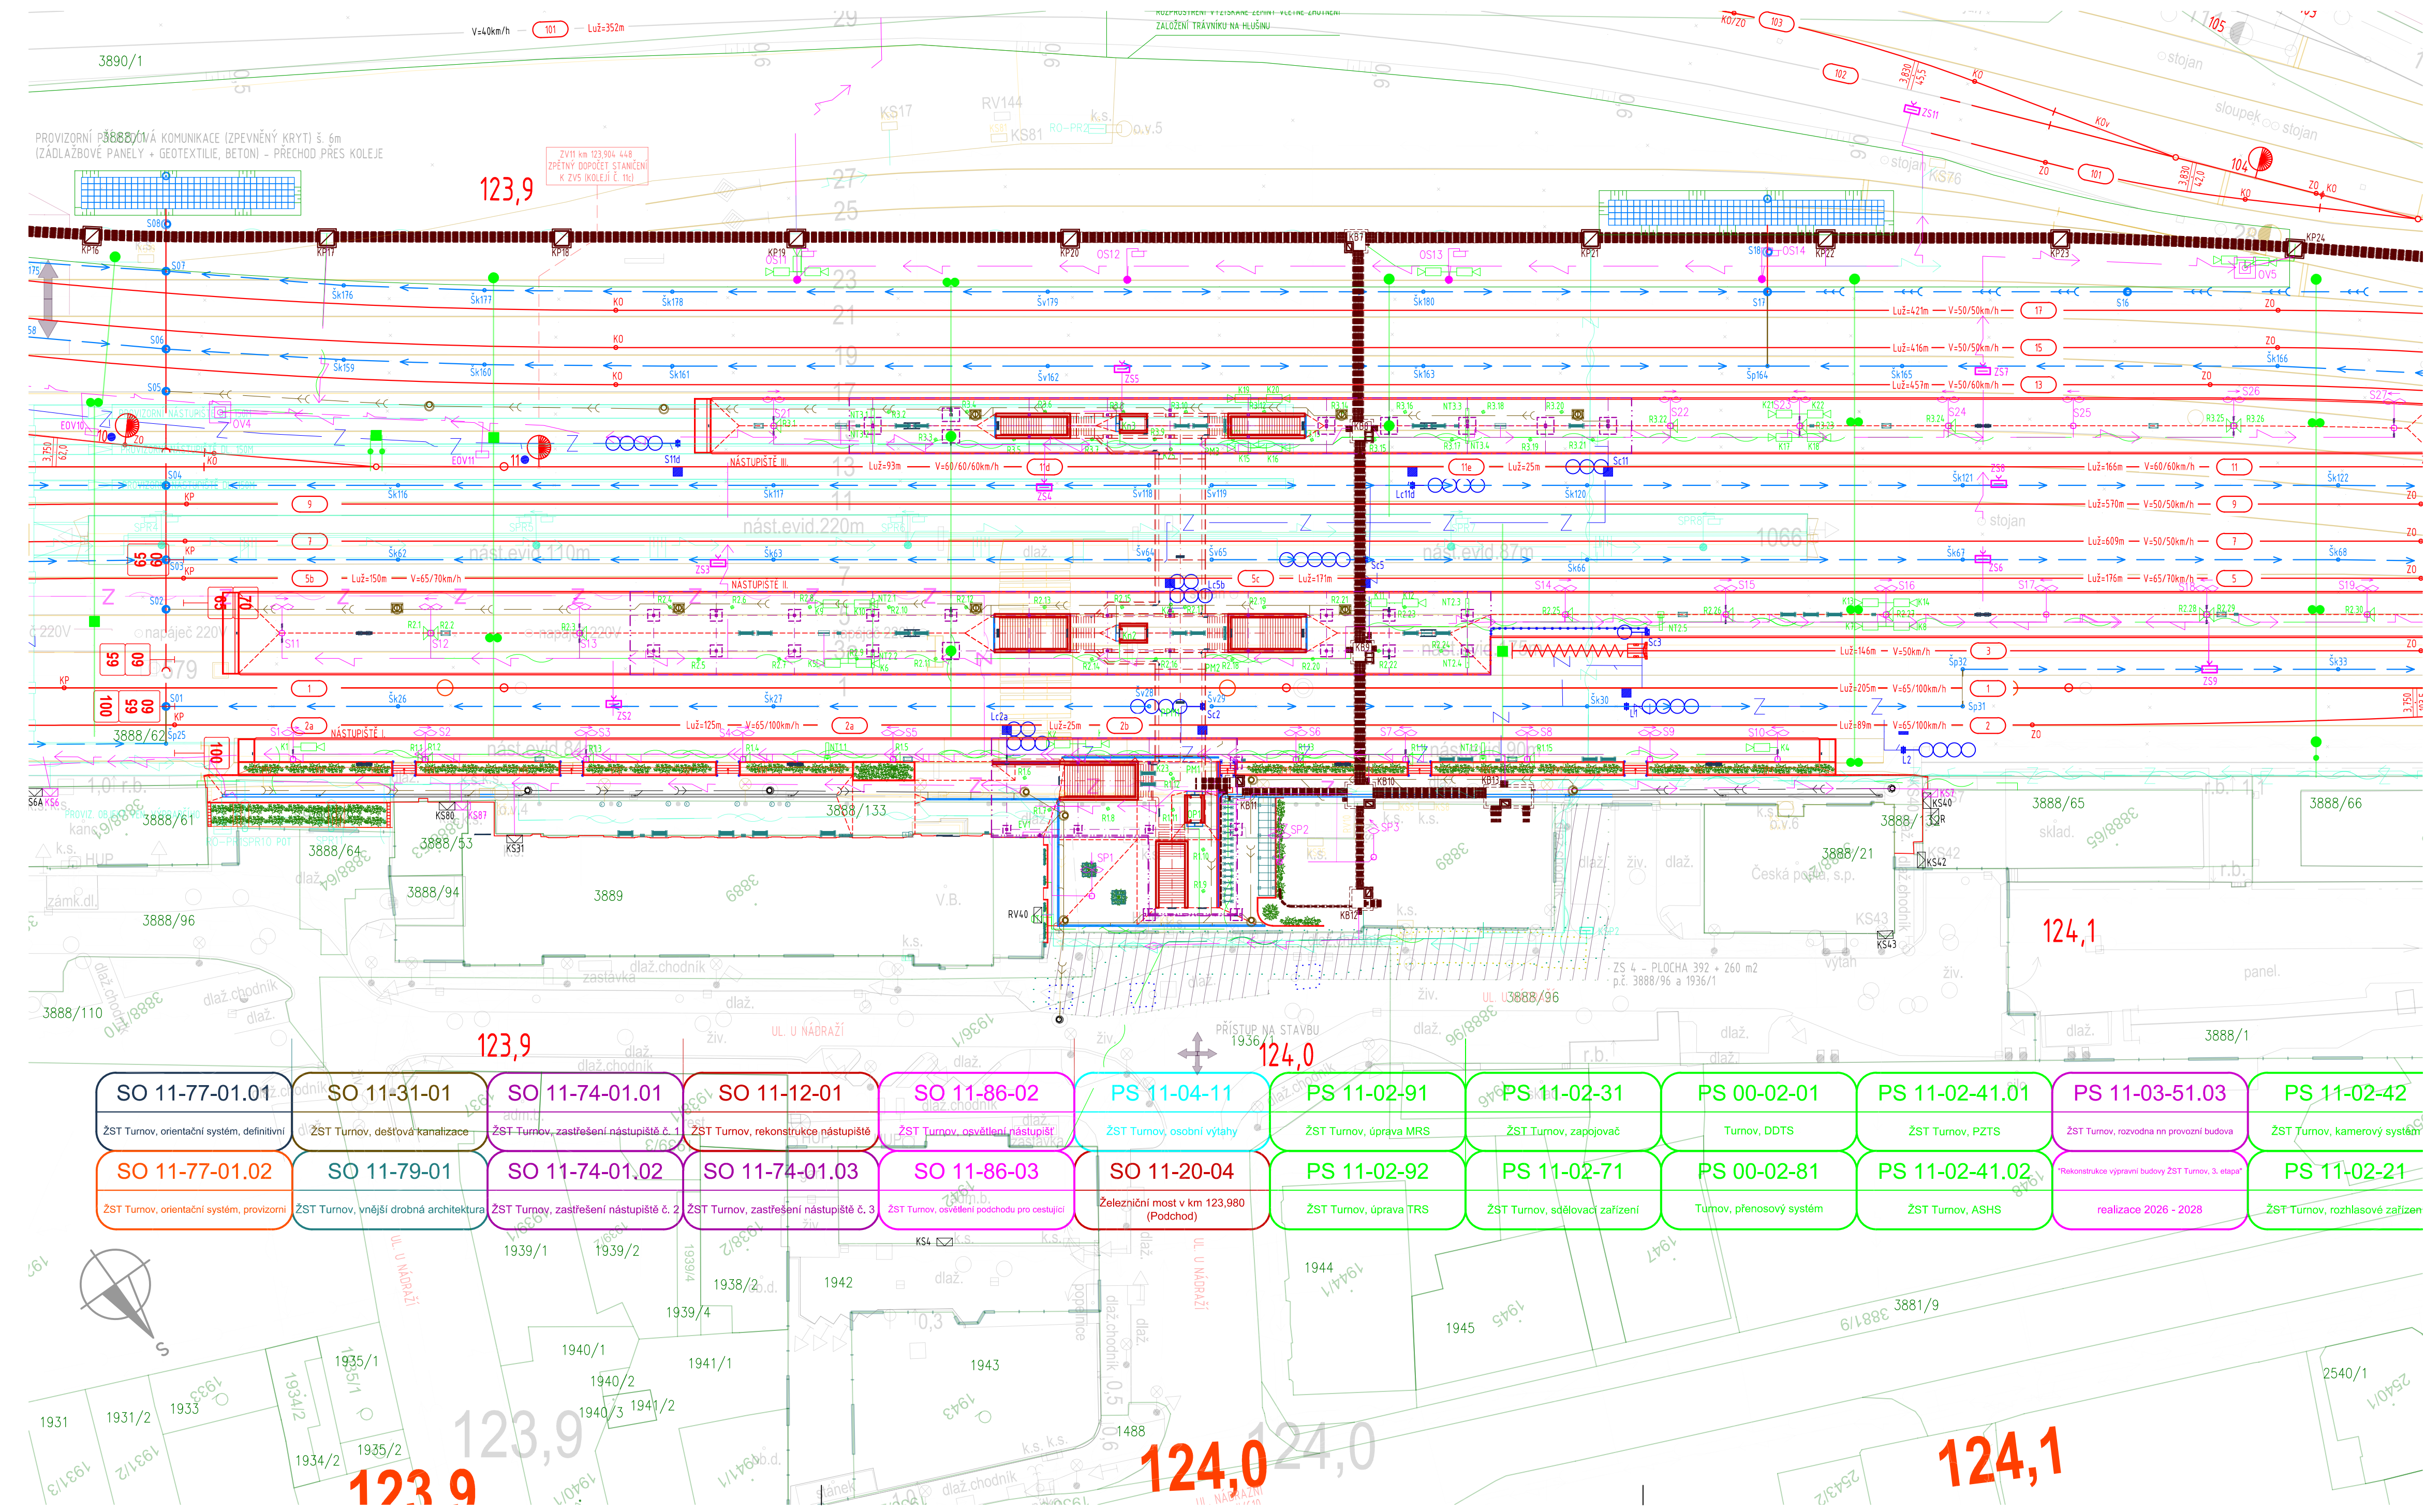

LEGENDA

LEGENDA STÁVAJÍCÍ SITUACE:

- STÁVAJÍCÍ KOLEJE
- STÁVAJÍCÍ (STAV) SITUACE
- HRANICE DRAŽNÍHO POZEMKU SŽ
- HRANICE DRAŽNÍHO POZEMKU ČD
- 193/1 HRANICE KATASTRU NEMOVITOSTI/PARCEL. ČÍSLO
- STÁVAJÍCÍ HRANICE OCHRANNÉHO PÁSMO DRAHY
- STÁVAJÍCÍ BODY ZAMĚŘENÍ

LEGENDA NOVÁ SITUACE:

- NOVÝ ŽELEZNIČNÍ SVRŠEK
- SMĚROVÁ A VÝŠKOVÁ ÚPRAVA KOLEJE
- POZEMNÍ KOMUNIKACE, HRANY DRAŽNÍCH OBJEKTŮ
- OSY POZEMNÍCH KOMUNIKACÍ A DALŠÍCH OBJEKTŮ
- HRANY NOVÉHO TERÉNU
- PROVIZORNÍ STAV KOLEJE
- RUŠENÉ KOLEJE / DEMOLICE
- NOVÝ ŽELEZNIČNÍ SPODEK-SANACE
- SOUVISEJÍCÍ STAVEBNÍ OBJEKTY NEBO STAVBY
- HRANICE NEBEZPEČNÉHO PÁSMO PŘEJEZDU A PŘECHODU
- ROZHLEDOVÉ POMĚRY NA PŘEJEZDU
- PROTILUKOVÉ STĚNY, GABIONY, OPĚRNÉ A ZÁRUBNÍ ZDI
- TRATIVODY
- PŘÍČNÉ A PODÉLNÉ SVODY
- TRATIVOD NAD SVODEM
- ZPEVNĚNÉ A NEZPEVNĚNÉ PŘÍKOPY
- VYZNAČENÍ A ČÍSLO PŘÍČNÉHO ŘEZU (VPR, PR)
- VYTÝČOVACÍ BODY
- SMĚROVÉ POSUNY OD STÁVAJÍCÍ KOLEJE

LEGENDA OSTATNÍ SITUACE:

- HRANICE OP VODNÍHO ZDROJE
- HRANICE CHRÁNĚNÉHO LOŽISKOVÉHO ÚZEMÍ
- HRANICE CHKO
- HRANICE OP CHKO
- HRANICE PAMÁTKOVÉ REZERVACE
- HRANICE OP PAMÁTKOVÉ REZERVACE
- HRANICE ARCHEOLOGICKÉ LOKALITY
- HRANICE PŘÍRODNÍHO PARKU
- BIOKORIDOR
- BIOCENTRUM
- HRANICE KATASTRÁLNÍHO ÚZEMÍ
- HRANICE KRAJE
- HRANICE OBCE
- NOVÉ NAVRŽENÉ HRANICE OCHR. PÁSMO DRAHY

LEGENDA NOVÝCH INŽENÝRSKÝCH SÍTÍ:

- VODOVOD
- KANALIZACE
- ZABEZPEČOVACÍ KABEL - PODZEMNÍ
- ZABEZPEČOVACÍ KABEL - NADZEMNÍ
- SDĚLOVACÍ KABEL - PODZEMNÍ
- SDĚLOVACÍ KABEL - NADZEMNÍ
- SLABOPROUDÝ KABEL NN - PODZEMNÍ
- SLABOPROUDÝ KABEL NN - NADZEMNÍ
- SILNOPROUDÝ KABEL VN - PODZEMNÍ
- SILNOPROUDÝ KABEL VN - NADZEMNÍ
- SILNOPROUDÝ KABEL ZVN/VVN - NADZEMNÍ
- EOV KABEL
- NTL PLYNOVOD
- STL PLYNOVOD
- VTL PLYNOVOD

LEGENDA NOVÁ - TECHNOLOGICKÉ PRVKY SITUACE:

- VÝSTRAŽNÍK SE ZÁVOROU/BEZ ZÁVORY
- RELEOVÝ DOMEK/TECHNOLOGICKÉ OBJEKTY
- STOŽÁRY TV
- ROZVADĚČ
- STOŽÁRY OSVĚTLENÍ
- KABELOVÉ PŘECHODY

LEGENDA ORGANIZACE VÝSTAVBY SITUACE:

- OBVOD STAVBY
- OBVOD STAVENIŠTĚ
- PŘÍSTUPY NA STAVENIŠTĚ
- PŘÍJEZDOVÉ KOMUNIKACE (ZPEVNĚNÝ POVRCH)
- PŘÍJEZDOVÉ KOMUNIKACE (NEZPEVNĚNÝ POVRCH)
- PROVIZORNÍ PŘÍJEZDOVÉ KOMUNIKACE

LEGENDA STÁVAJÍCÍCH INŽENÝRSKÝCH SÍTÍ:

- VODOVOD
- KANALIZACE
- ZABEZPEČOVACÍ KABEL - PODZEMNÍ
- ZABEZPEČOVACÍ KABEL - NADZEMNÍ
- SDĚLOVACÍ KABEL - PODZEMNÍ
- SDĚLOVACÍ KABEL - NADZEMNÍ
- SLABOPROUDÝ KABEL NN - PODZEMNÍ
- SLABOPROUDÝ KABEL NN - NADZEMNÍ
- SILNOPROUDÝ KABEL VN - PODZEMNÍ
- SILNOPROUDÝ KABEL VN - NADZEMNÍ
- SILNOPROUDÝ KABEL ZVN/VVN - NADZEMNÍ
- EOV KABEL
- NTL PLYNOVOD
- STL PLYNOVOD
- VTL PLYNOVOD
- PAROVOD - PODZEMNÍ
- PAROVOD - NADZEMNÍ
- TEPLOVOD - PODZEMNÍ
- TEPLOVOD - NADZEMNÍ

LEGENDA STÁVAJÍCÍCH INŽENÝRSKÝCH SÍTÍ - dle správců:

- SSZT SŽ OŘ SSZT KABEL
- SEE SŽ OŘ SEE KABEL
- SPS SŽ OŘ SPS KABEL
- ČD-TELEMATIKA KABEL
- ČD RSM
- CETIN CETIN
- VODAFONE VODAFONE

LEGENDA PLOCH:

- POZEMNÍ KOMUNIKACE (ASFALTOVÝ KRYT)
- CHODNÍK (BETONOVÁ DLAŽBA)
- POCHOZÍ PLOCHA (NÁSTUPIŠTĚ)
- DEMOLICE
- HMATOVÉ PRVKY (BETONOVÁ RELIEFNÍ DLAŽBA)
- ZDRSNĚNÉ HMATOVÉ PÁSY
- VODICÍ LINIE S FUNKCÍ VAROVNÉHO PÁSU
- BEZPEČNOSTNÍ PRVKY (NATĚR)
- ZPEVNĚNÉ PLOCHY (NAPŘ. ŽULOVÁ DLAŽBA)
- ZELENÁ PLOCHA
- VEGETAČNÍ PRVKY
- ŽELEZNIČNÍ PŘEJEZDY
- ŽELEZNIČNÍ PŘECHODY
- SANACE TĚLESA ŽELEZNIČNÍHO SPODKU
- VSÁKOVACÍ OBJEKTY
- DRAŽNÍ STEZKY
- DRAŽNÍ POZEMNÍ OBJEKTY
- KCE Z ŽELEZOBETONU
- KCE Z PROSTÉHO BETONU
- ZÁŘÍZENÍ STAVENIŠTĚ
- SILNIČNÍ OBRUBNÍK +120 mm
- SILNIČNÍ OBRUBNÍK +/-0 mm
- CHODNÍKOVÝ OBRUBNÍK +60 mm
- CHODNÍKOVÝ OBRUBNÍK +/-0 mm

Ministerstvo dopravy Státní fond dopravní infrastruktury	
Jiná ověření:	Paré:
Orientační schéma:	Razítko oprávněné osoby:
Podpis: Datum:	
Revize:	Datum:
Stavění/Investor:	Správa železnic, státní organizace
Adresa:	Dlažďená 1003/7, 110 00 Praha 1
Zástupce investora:	Stavební správa západ
Adresa:	Ke Štvanici 656/3, 186 00 Praha 8 - Karlín
Zhotovitel díla:	Ps + SB + A4 - ŽST Turnov DSP, PDPS
Adresa:	U Elektry 830/2b, 198 00 Praha 9
Kontakt:	T: +420 281 090 860 E: firma@projekt-servis.cz
Zhotovitel objektu:	PROJEKT servis spol. s r.o.
Adresa:	U Elektry 830/2b, 198 00 Praha 9
Kontakt:	T: +420 281 090 860 E: firma@projekt-servis.cz
Hlavní projektant (HIP):	Ing. Martin Koudełka
Specialista:	Ing. Radomír Hanák
Název stavby/akce:	Rekonstrukce žst. Turnov
Název části:	Mosty, propustky a zdi
Název objektu/díli části:	Železniční most v km 123,980 (Podchod)
Název přílohy:	Situace
Název díli části přílohy:	-
Odpovědný projektant:	Ing. Aleš Menšík
Zpracovatel přílohy:	Ing. Anna Popová
Měřítko:	1:500
Formáty:	6 x A4
Kraj:	Liberecký
Katastrální území:	viz textová část
TUDU:	viz textová část
Číslo:	5631700077
Podpis:	Ing. Aleš Menšík
Průběh:	31.08.2025