OBJEKT B - PŮDORYS 1NP - KOORDINAČNÍ VÝKRES
1:50

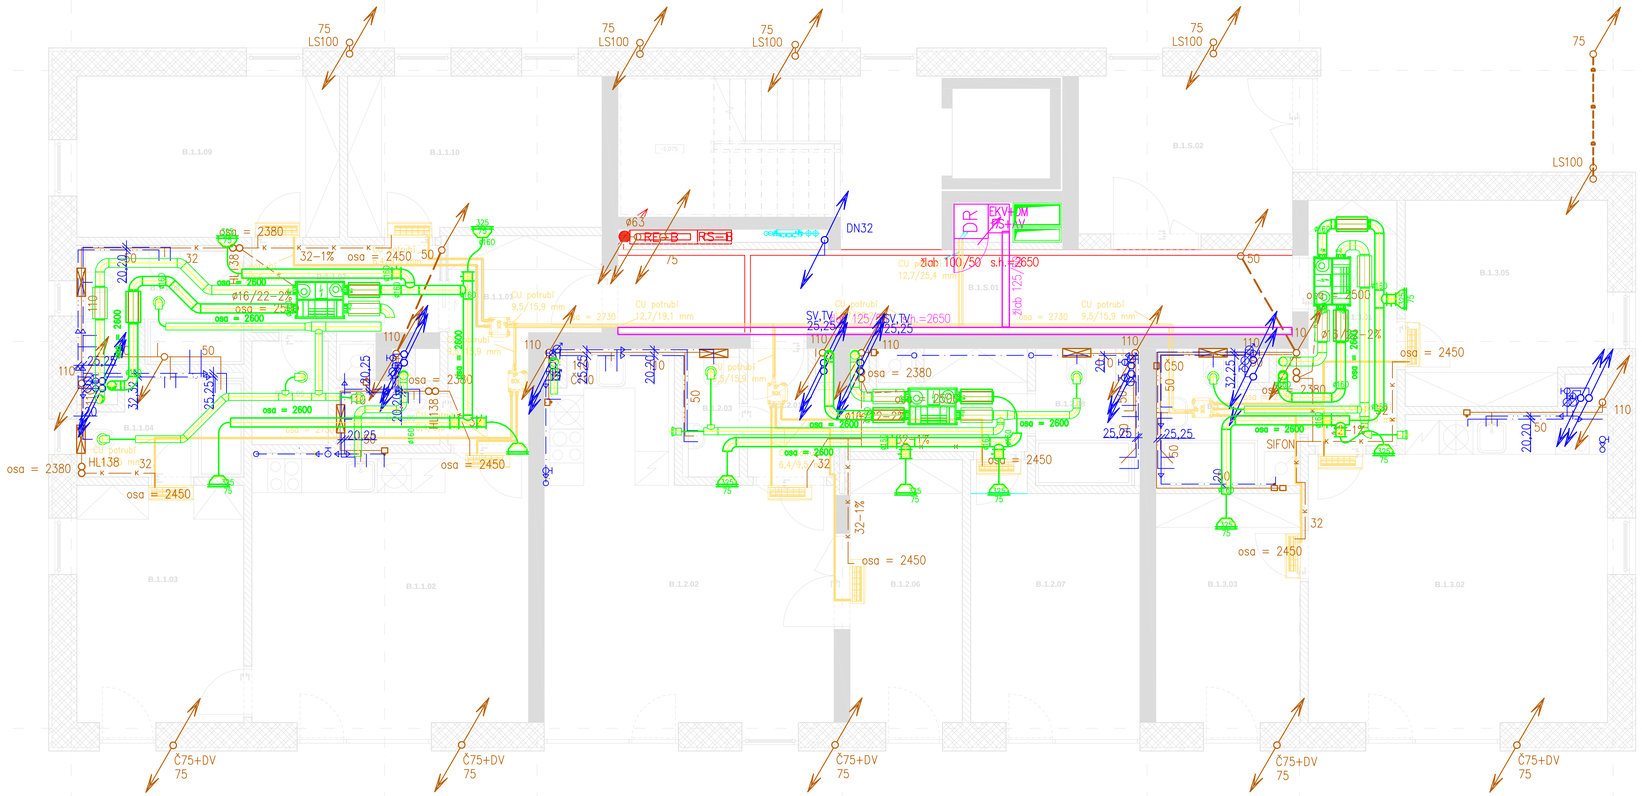

Legenda rozvodů a zařízení

- vzduchotechnika
- chlazení
- vytápění
- vodovod (horizontální rozvody v bytech jsou vedeny v podlaze nebo max. ve výšce 1,3m)
- kanalizace
- silnoproud
- slaboproudy

Tabulka místností 1.NP

Č. místností	Název	Plocha
B.1.1.01	CHODBA	8 m²
B.1.1.02	OBÝVACÍ POKOJ + KK	24 m²
B.1.1.03	POKOJ	12 m²
B.1.1.04	KOUPELNA	5 m²
B.1.1.05	KOMORA	2 m²
B.1.1.06	WC	2 m²
B.1.1.07	CHODBA	6 m²
B.1.1.08	KOUPELNA	6 m²
B.1.1.09	POKOJ	13 m²
B.1.1.10	POKOJ	12 m²
B.1.2.01	CHODBA	3 m²
B.1.2.02	OBÝVACÍ POKOJ + KK	27 m²
B.1.2.03	WC	2 m²
B.1.2.05	CHODBA	5 m²
B.1.2.06	POKOJ	9 m²
B.1.2.07	POKOJ	13 m²
B.1.2.08	KOUPELNA	4 m²
B.1.3.01	CHODBA	7 m²
B.1.3.02	OBÝVACÍ POKOJ + KK	28 m²
B.1.3.03	POKOJ	10 m²
B.1.3.04	KOUPELNA	5 m²
B.1.3.05	POKOJ	12 m²
B.1.S.01	ZÁDVEŘÍ	11 m²
B.1.S.02	SPOLEČNÁ CHODBA	18 m²
B.1.S.03	SPOLEČNÁ CHODBA	5 m²

projekt / project — číslo zakázky / project number: 185-01

BYTOVÝ SOUBOR LIBUŠE

stupeň dokumentace / design stage

DOKUMENTACE PRO PROVEDENÍ STAVBY — DPS
DETAIL DESIGN DOCUMENTATION — DDD

klient / client

VELTON REAL ESTATE
Na Strži 2102/61a
140 00, Praha 4 - Krč

architekt / architect

adns architekti
A.D.N.S. architekti s.r.o.
Na Příkopě 853/12
110 00 Praha 1 - Nové Město

generální projektant / general designer

ABMV WORLD
ABMV world s.r.o.
Prosecká 527/24
180 00 Praha 8

projektant / designer

ABMV WORLD
ABMV world s.r.o.
Prosecká 527/24
180 00 Praha 8

odpovědný projektant / designer
Ing. arch. Zdeněk Vávra

vypracoval / drawn by
Štěpán Šustr

kontroloval / checked by
Ing. Marek Veselý

revize / revision	popis / description	datum / date
Rev	stručný popis revize	datum vydání revize

část dokumentace / documentation part

D | DOKUMENTACE OBJEKTŮ A TECHNICKÝCH A TECHNOLOGICKÝCH ZAŘÍZENÍ

stavební objekt / building object

SO01 | BYTOVÝ DŮM

profesní díl / specialist part

120 | ARCHITEKTONICKO-STAVEBNÍ ŘEŠENÍ - OBJEKT B, NADZEMNÍ ČÁST

název výkresu / drawing title

OBJEKT B - KOORDINAČNÍ VÝKRES 1.NP

datum revize 00 / revision date 00	měřítko / scale	počet A4 / A4 count	paré
15.09.2021	1:50	10 x A4	

číslo výkresu / sheet number: 9210

kód výkresu / sheet code: 185D1_DPS_D_SO01_120_9210_R00

N

±0,000 = 303,800 m n. m.
výškový systém: Bpv
souřadný systém: JTSK