


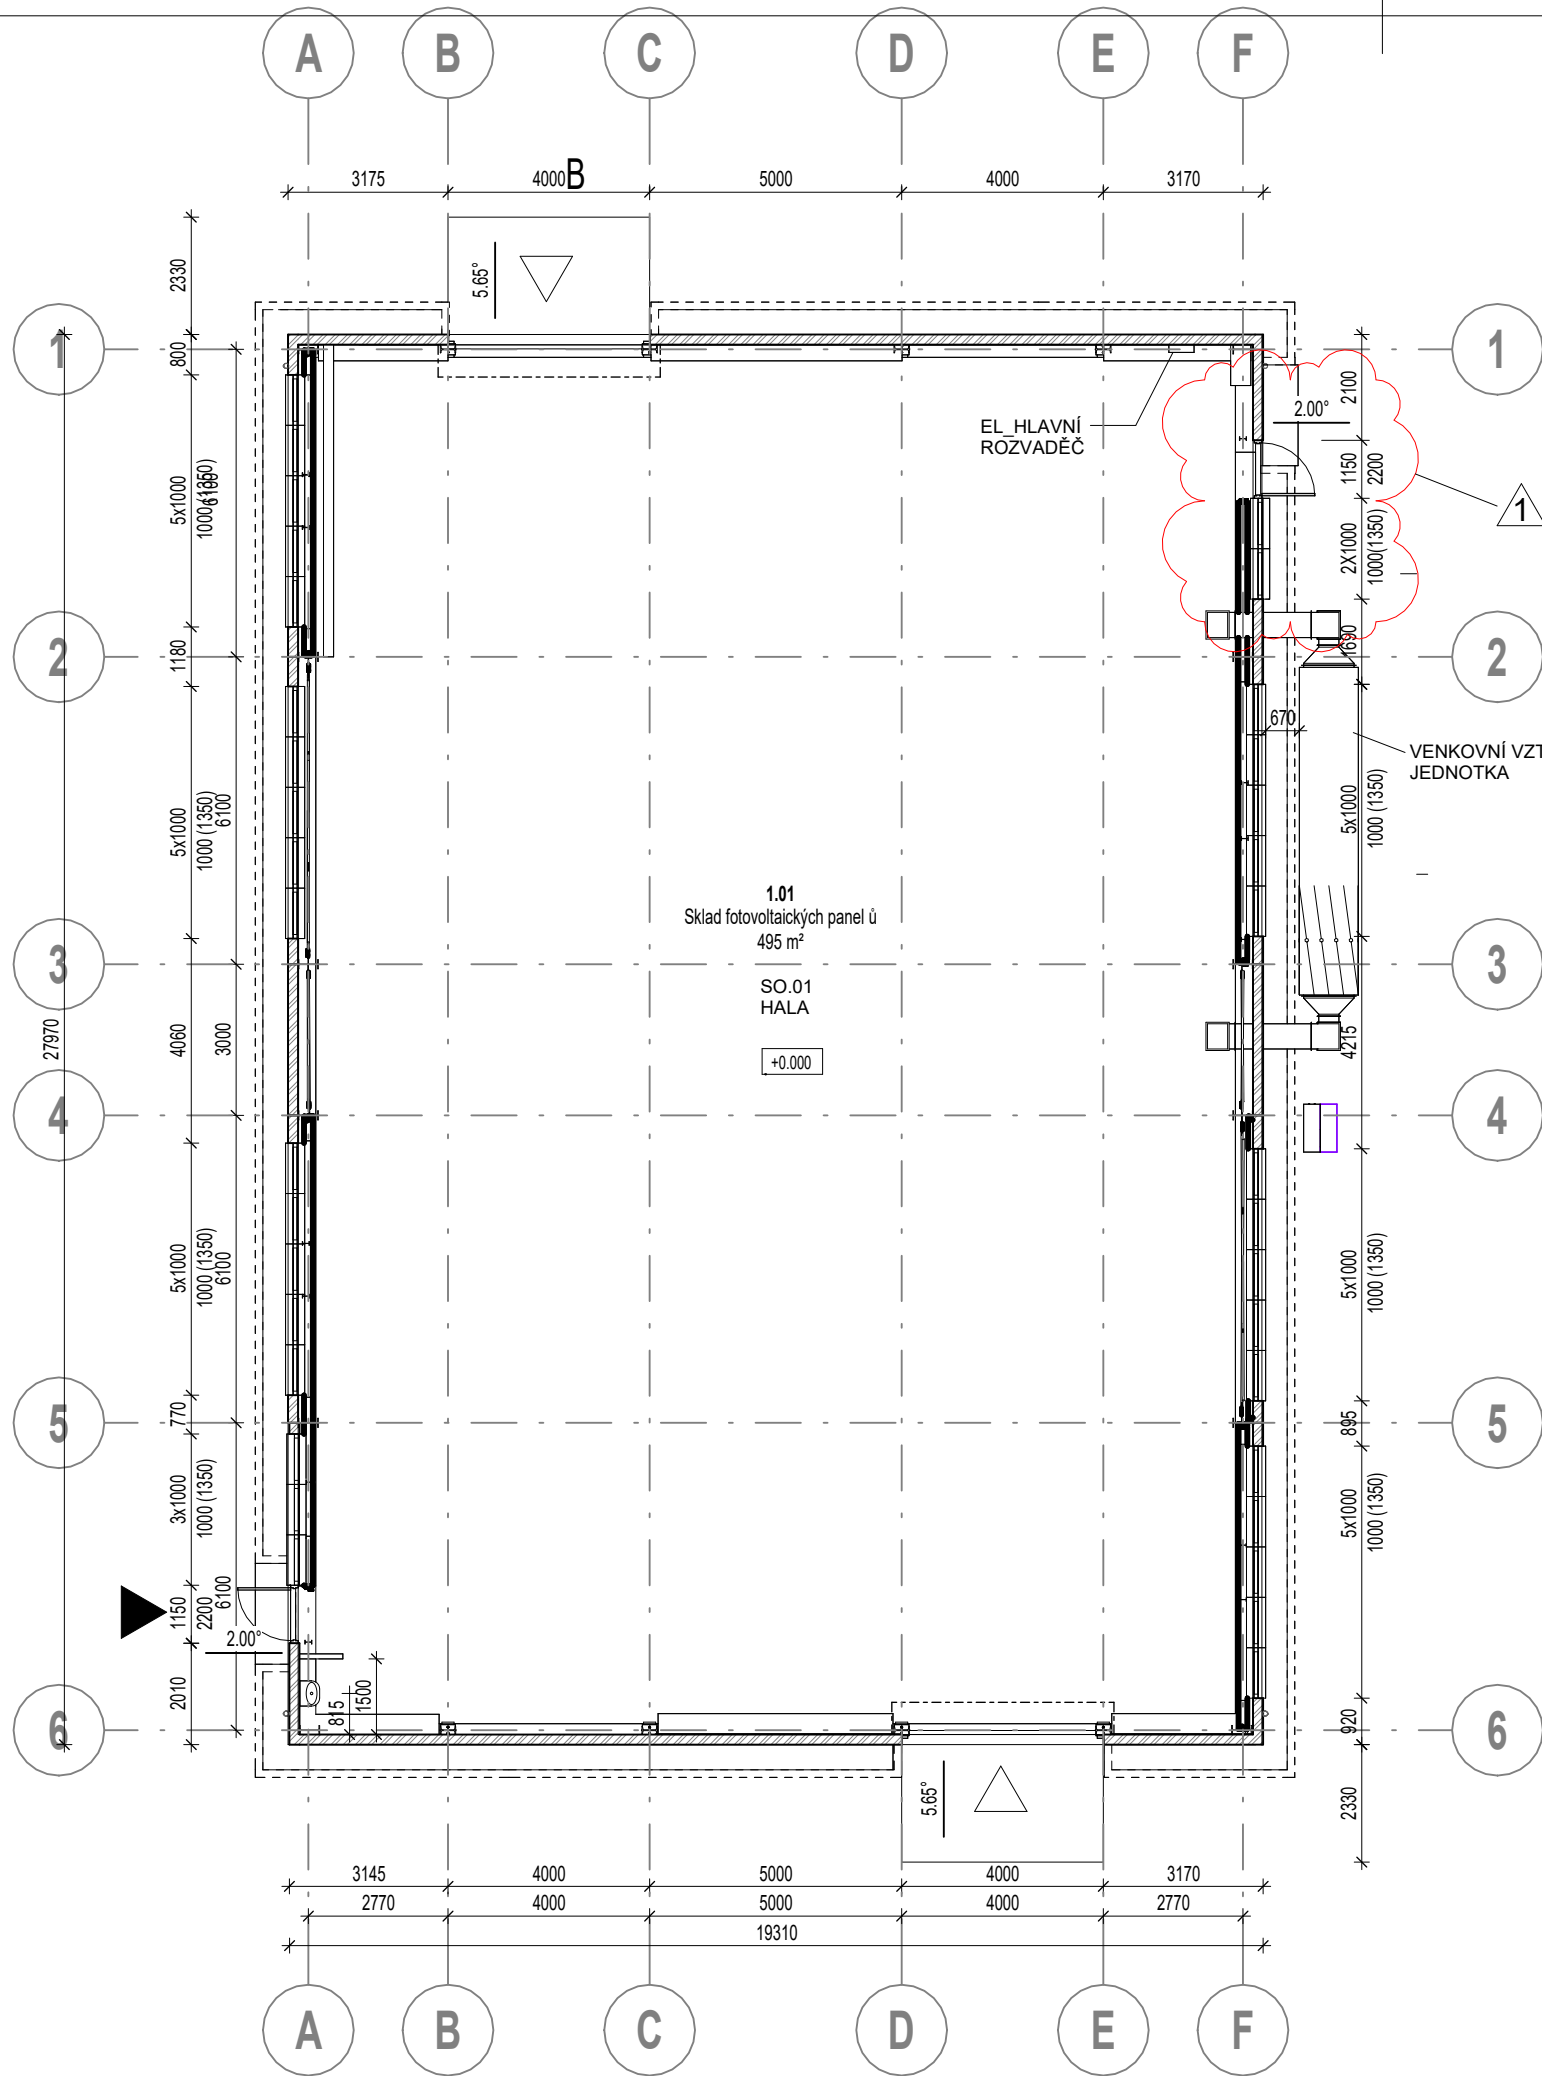

TABULKA MÍSTNOSTÍ					
ČÍSLO	NÁZEV MÍSTNOSTÍ	PLOCHA	PODLAHA	POVRCH STĚN	POVRCH STROPU
1.01	Sklad fotovoltaických panelů	495 m²	Stěrka	Stěrka	Kingspan povr. úpr.

LEGENDA MATERIÁLŮ:

- Obvodový plášť - panely Kingspan s požární odolností EW 15 DP1
- Železobeton
- Beton prostý

Poznámka:
- Zatížení podlahy $\geq 1600\text{kg/m}^2$
- EW 15 DP1: požární dveře požár omezující po dobu 15 minut, dřevěné, opatřené samozavíračem,

OCEL:
- Konstrukční OCEL ČSN EN 10025 S235 - Profily, Styč. plechy
- Konstrukční OCEL ČSN EN 10025 8.8 - Spoj. Prvky (Svorníky, Kolíky, Čepy)
-- Specifikace v TZ STATIKA

BETON:
- Deska ČSN EN 206-1 C30/37-XC2 (CZ F.1) - CI 0,4 - Dmax 16-S3
-- Specifikace v TZ STATIKA
- Základy ČSN EN 206-1 C16/20-XC0, (CZ F.1)-CI 0,4-Dmax 16-S3
-- Specifikace v TZ STATIKA

- Při provádění je potřeba posutpovat podle nejnovější revize výkresů.
- Před prováděním je potřeba porovnat výkresy stavebně konstrukční a architektonicko-stavební částí a na případné rozpory upozornit hlavního inženýra projektu a statika
- Dokumentace je vypracovaná ve stupni dokumentace pro stavební povolení a nenahrazuje prováděcí dokumentaci. Cílem posudku je ověřit proveditelnost konstrukce a předpokládá se v pokračování projekčních prací v dalším stupni.

Výkaz revizních obláčků	
Označení	Popis
1	Posun dveří vůči původnímu PBR, mají být na obou dveřích panikové klíky?

HALA HRADEC KRÁLOVÉ

Vážní 857, 50003 Hradec Králové - Slezské Předměstí

STUPEŇ PROJEKTU +0,000 = +234,690 mmm Bpv

DOKUMENTACE PRO POVOLENÍ ZÁM ĚRU (DPZ)

ODPOVĚDNÝ PROJEKTANT

Ing.arch. Jakub Volka, ČKA 03947
733 575 363, jakub.volka@basepoint.cz

VYPRACOVAL

Ing. arch. Jakub Volka
Anna Abrahámová
Kristián Pócsik
INVESTOR

SOLAR DISPOREC s.r.o. , Praha IČO 19546220
Malostranské náměstí 5/28, Malá Strana (Praha 1),
118 00 Praha

DÍL

D

ČÁST DOKUMENTACE

D.1.1.1

OBSAH VÝKRESU

PŮDORYS 1NP

MĚŘÍTKO	FORMÁT
1:150	2 X A4
DATUM	1.VYDÁNÍ
03/2026	07/2025

STUPEŇ	DÍL	ČÁST	ČÍSLO	PŘÍLOHA	REVIZE
DPZ	D-S001	ARS	A101	1NP	R00

ZPRACOVATEL ČÁSTI

basepoint s.r.o.
V Benátkách 2350/6
149 00, praha 4
www.basepoint.cz

GENERÁLNÍ PROJEKTANT

basepoint s.r.o.
V Benátkách 2350/6
149 00, praha 4
www.basepoint.cz

