


LEGENDA:

- Dodp. E-HP 9 kW
PT Vents UET-150
- Nízkotepelný elektrický ohřev s ventilátorem
9 kW
- Vysokotepelný solární panel FENIX
ECOSUN S+ 12

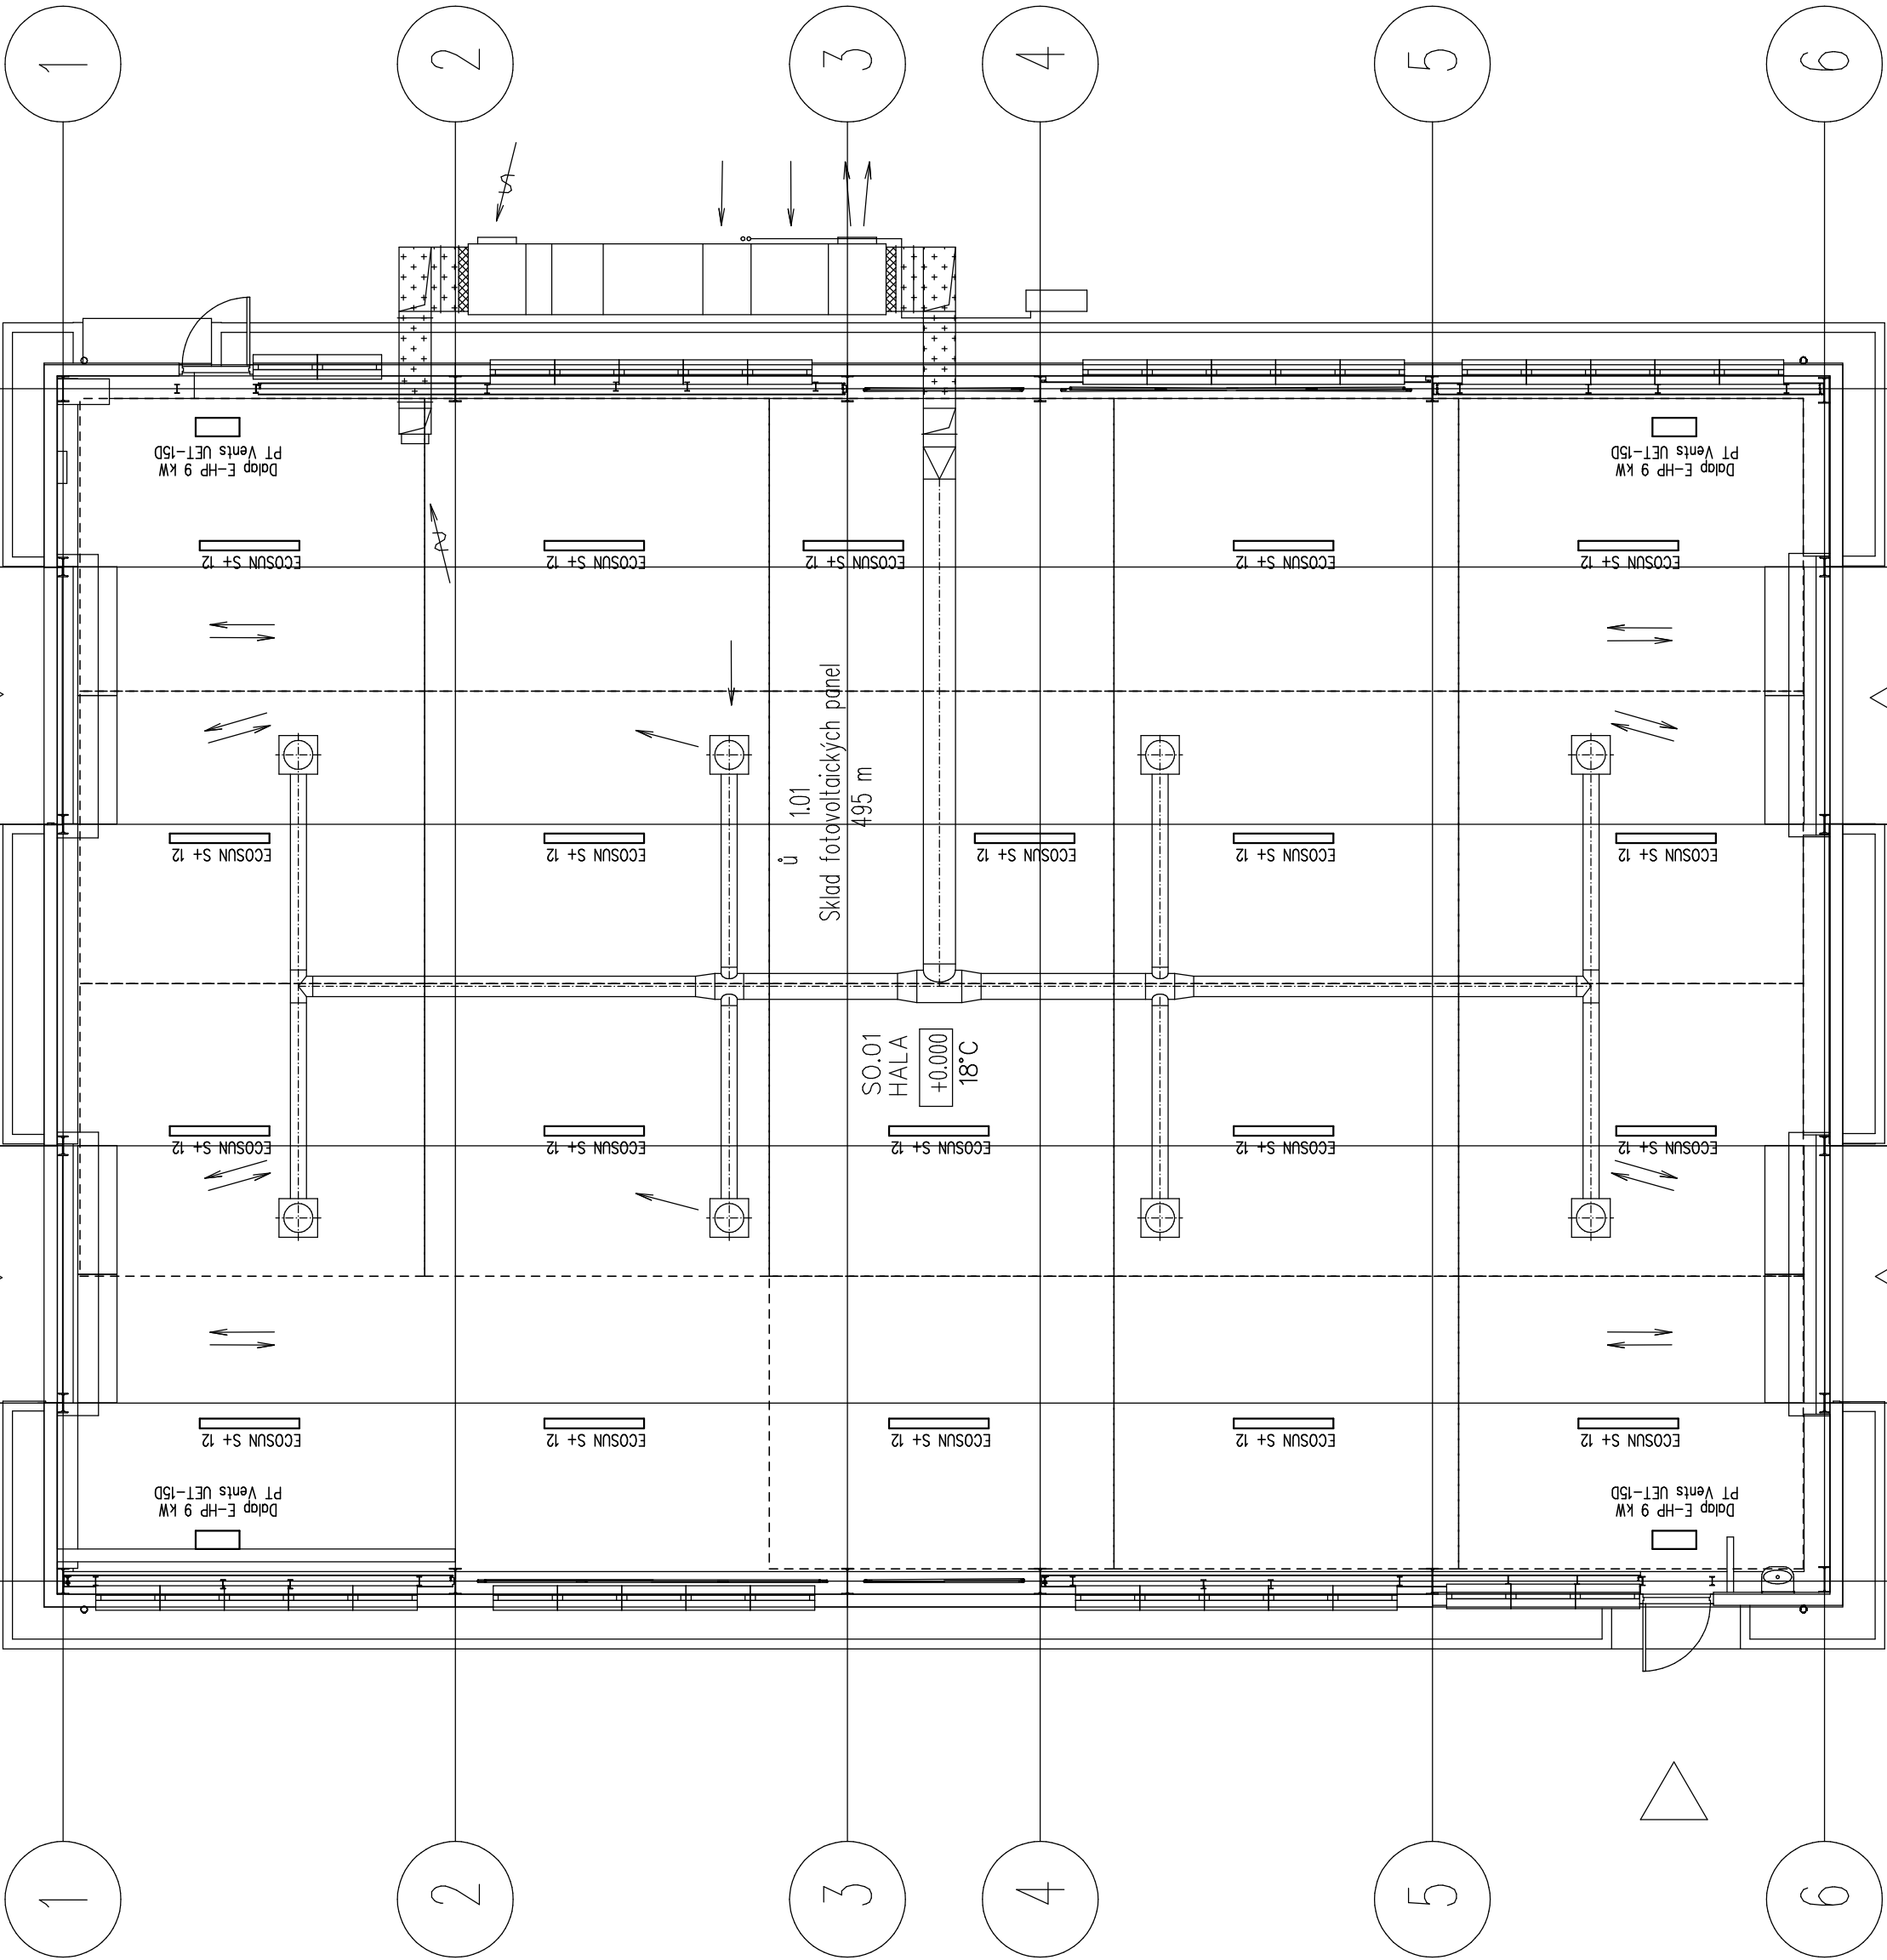

HALA HRADEC KRÁLOVÉ

Vzdání 857, 50003 Hradec Králové – Slezské
Předměstí

STUPĚŇ PROJEKTU +0.000→+234.690 mm BpV
DOKUMENTACE PRO PROVEDENÍ STAVBY

ODPOVĚDNÝ PROJEKTANT
Ing. Stanislav Jirucha, ČKAIT 0009051
603 265 695, jirucha@iol.cz
Projektant

VYPRACOVAL
Ing. Stanislav Jirucha, ČKAIT 0009051

INVESTOR
SOLAR DISPOREC s.r.o., Praha, IČO 1846220
Hradec Králové, náměstí 5/28 Mladá Strana (Praha)
118 08 Praha

ČÁST DOKUMENTACE
D.1.4.2 VYTÁPĚNÍ

OBSAH VÝKRESU
Půdorys rozmístění topidel

MĚŘÍTKO 1:100
FORMÁT A2-4x44

DATUM 05/2026

ČÍSLO VÝKRESU / REVIZE ČÍSLO PÁŘE

02

GENERÁLNÍ PROJEKTANT
Basepoint s.r.o.
V Benátkách 2350/6
149 00 Praha 4
www.basepoint.cz