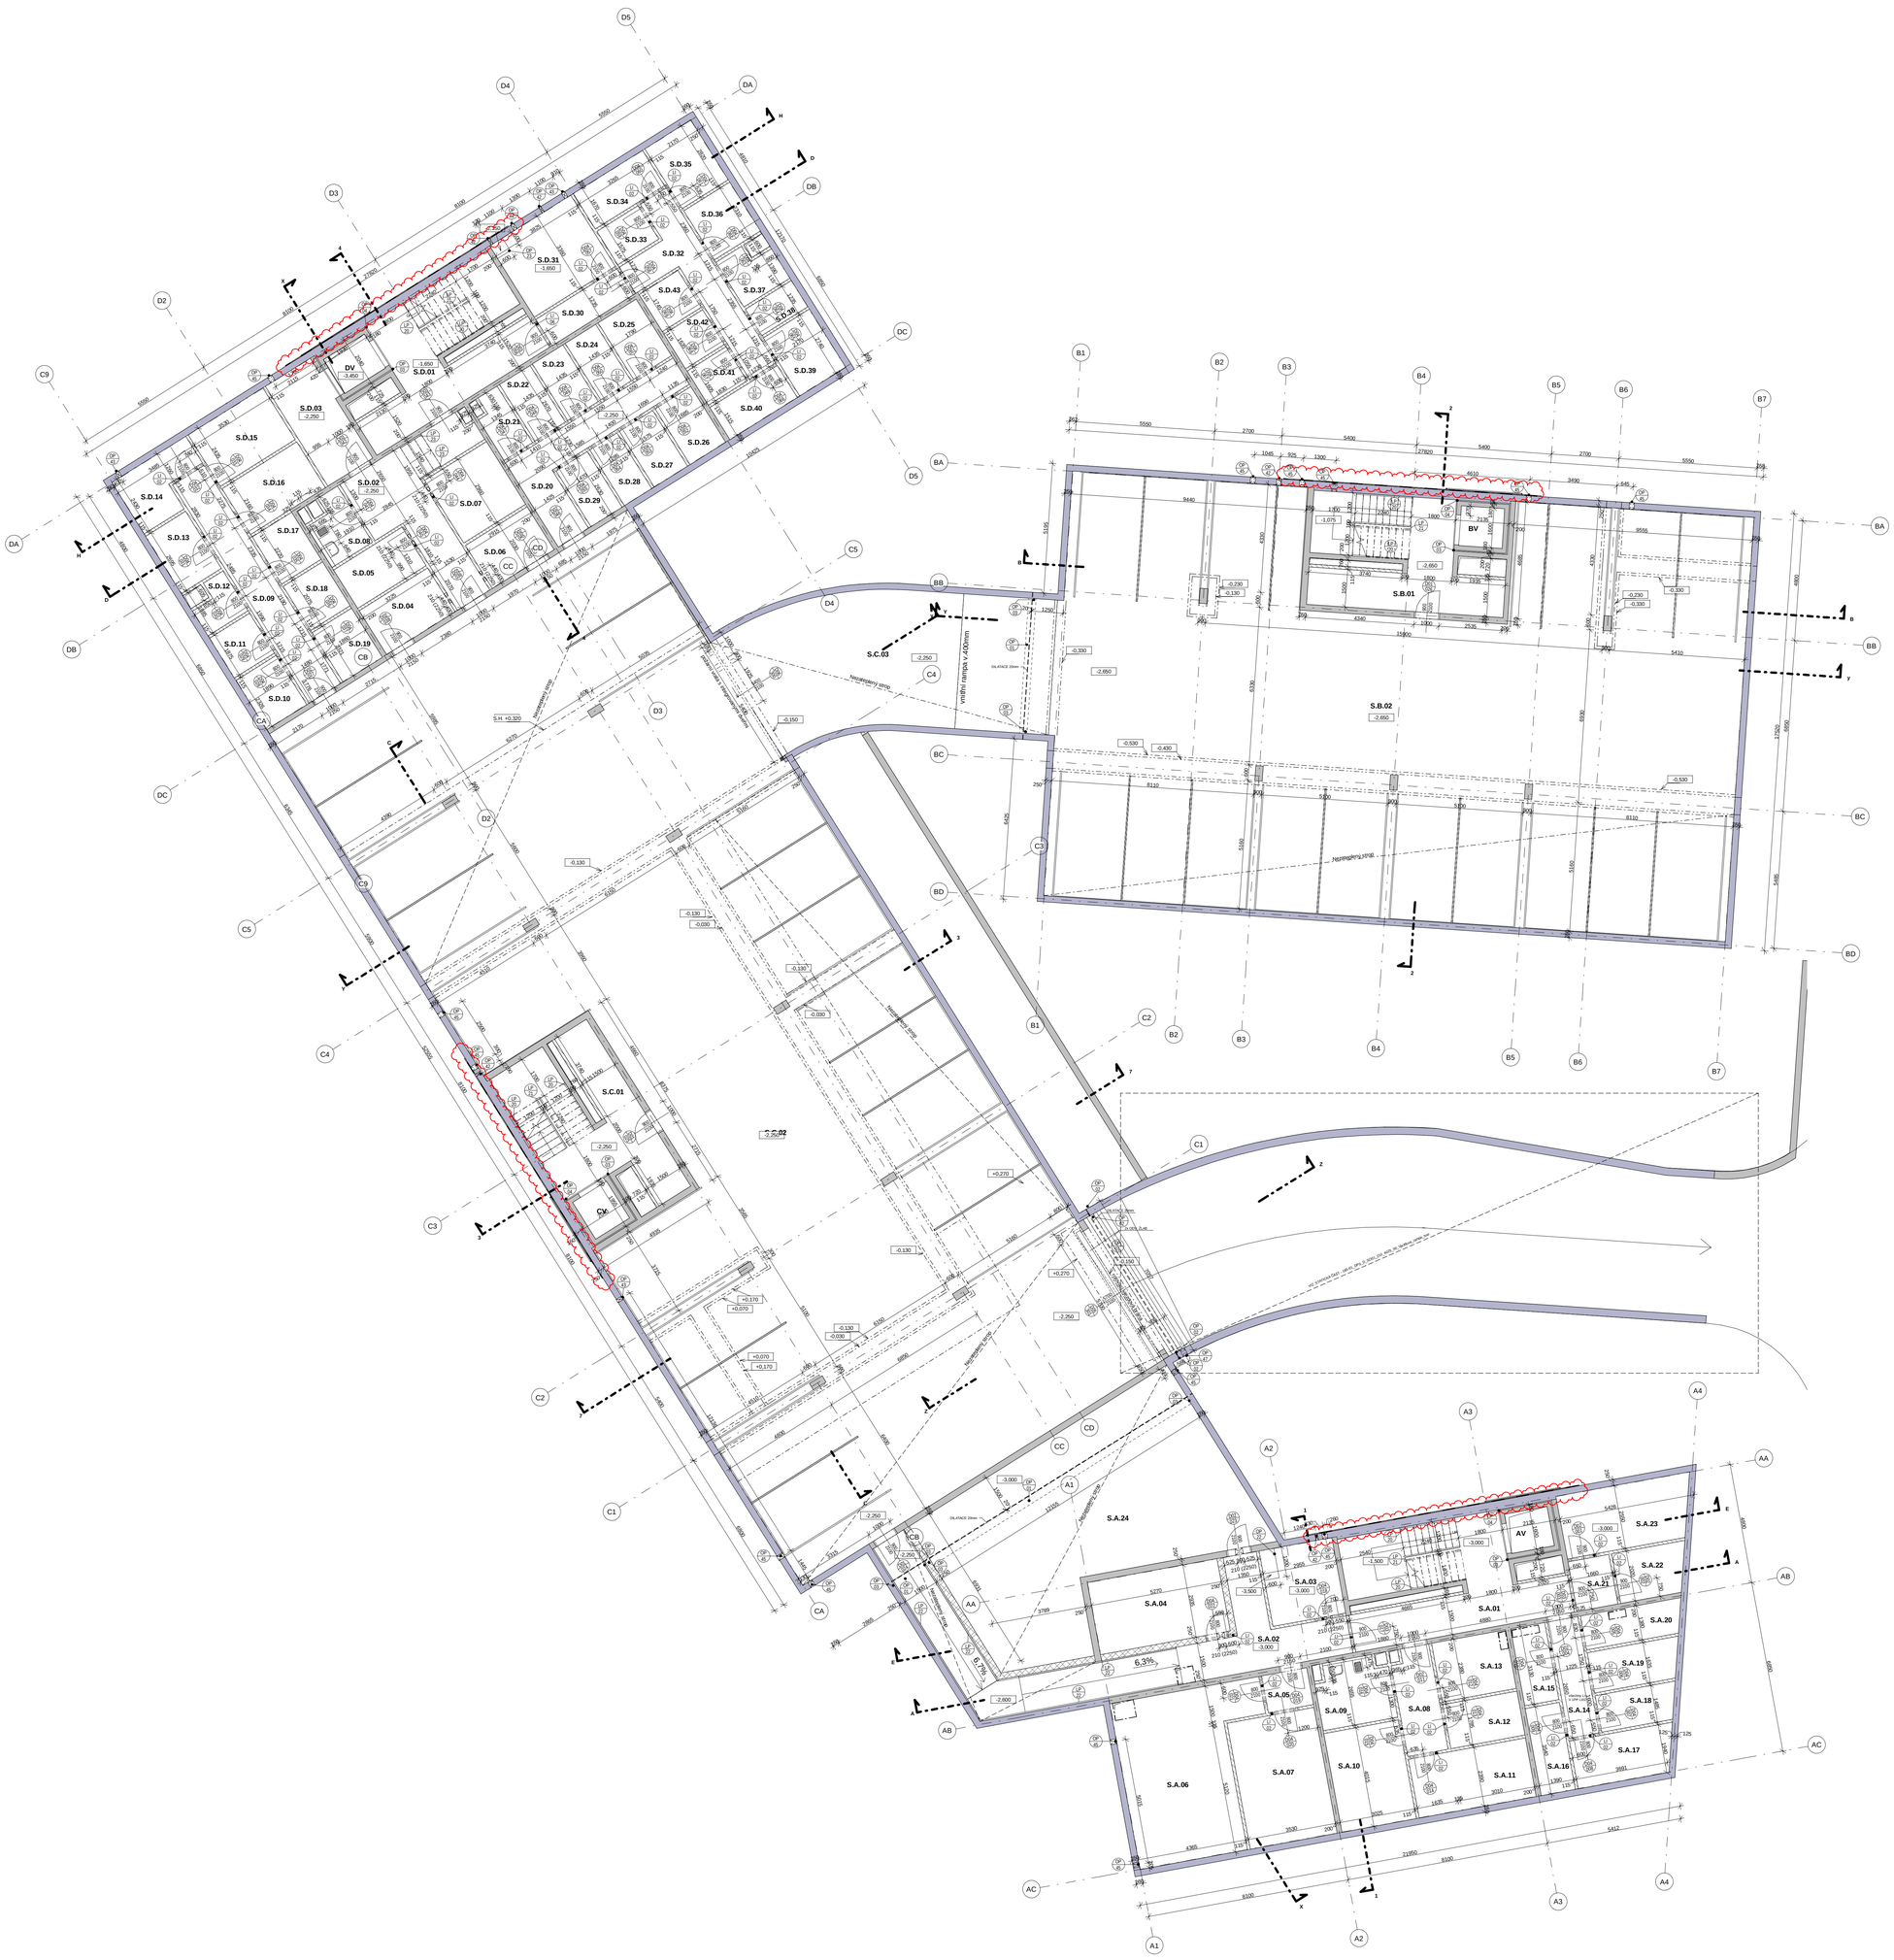

Tabulka místností 1.PP

Number	Name	Area
AV	VÝTAHOVÁ ŠACHTA	3 m²
BV	VÝTAHOVÁ ŠACHTA	3 m²
CV	VÝTAHOVÁ ŠACHTA	3 m²
DV	VÝTAHOVÁ ŠACHTA	3 m²
S.A.01	SPOLEČNÁ CHODBA	31 m²
S.A.02	SPOLEČNÁ CHODBA	38 m²
S.A.03	TECHNICKÁ MÍSTNOST	9 m²
S.A.04	SKLAD	15 m²
S.A.05	CHODBA	3 m²
S.A.06	SKLAD	32 m²
S.A.07	SKLAD	18 m²
S.A.08	CHODBA	7 m²
S.A.09	ÚKLID	7 m²
S.A.10	SKLAD	12 m²
S.A.11	SKLAD	11 m²
S.A.12	SKLAD	5 m²
S.A.13	SKLAD	7 m²
S.A.14	CHODBA	6 m²
S.A.15	SKLEPNÍ KÓJE - A	4 m²
S.A.16	SKLEPNÍ KÓJE - A	5 m²
S.A.17	SKLEPNÍ KÓJE - A	8 m²
S.A.18	SKLEPNÍ KÓJE - A	5 m²
S.A.19	SKLEPNÍ KÓJE - A	6 m²
S.A.20	SKLEPNÍ KÓJE - A	5 m²
S.A.21	CHODBA	3 m²
S.A.22	SKLAD	5 m²
S.A.23	TECHNICKÁ MÍSTNOST	13 m²
S.A.24	SKLAD	86 m²
S.B.01	SPOLEČNÁ CHODBA	27 m²
S.B.02	GARÁŽE	424 m²
S.C.01	SPOLEČNÁ CHODBA	27 m²
S.C.02	GARÁŽE	642 m²
S.C.03	GARÁŽE	69 m²
S.D.01	SPOLEČNÁ CHODBA	28 m²
S.D.02	SPOLEČNÁ CHODBA	18 m²
S.D.03	SPOLEČNÁ CHODBA	10 m²
S.D.04	SKLAD	7 m²
S.D.05	SKLAD	6 m²
S.D.06	SKLAD	6 m²
S.D.07	SKLAD	9 m²
S.D.08	ÚKLID	4 m²
S.D.09	CHODBA	15 m²
S.D.10	SKLEPNÍ KÓJE - C	4 m²
S.D.11	SKLEPNÍ KÓJE - C	4 m²
S.D.12	SKLEPNÍ KÓJE - C	3 m²
S.D.13	SKLEPNÍ KÓJE - C	5 m²
S.D.14	SKLEPNÍ KÓJE - C	7 m²
S.D.15	SKLEPNÍ KÓJE - C	9 m²
S.D.16	SKLEPNÍ KÓJE - C	8 m²
S.D.17	SKLEPNÍ KÓJE - C	4 m²
S.D.18	SKLEPNÍ KÓJE - C	4 m²
S.D.19	SKLEPNÍ KÓJE - C	4 m²
S.D.20	CHODBA	14 m²
S.D.21	SKLEPNÍ KÓJE - B	3 m²
S.D.22	SKLEPNÍ KÓJE - B	4 m²
S.D.23	SKLEPNÍ KÓJE - B	4 m²
S.D.24	SKLEPNÍ KÓJE - B	4 m²
S.D.25	SKLEPNÍ KÓJE - B	5 m²
S.D.26	SKLEPNÍ KÓJE - B	4 m²
S.D.27	SKLEPNÍ KÓJE - B	4 m²
S.D.28	SKLEPNÍ KÓJE - B	3 m²
S.D.29	SKLEPNÍ KÓJE - B	4 m²
S.D.30	SPOLEČNÁ CHODBA	5 m²
S.D.31	TECHNICKÁ MÍSTNOST	13 m²
S.D.32	CHODBA	13 m²
S.D.33	SKLEPNÍ KÓJE - D	3 m²
S.D.34	SKLEPNÍ KÓJE - D	5 m²
S.D.35	SKLEPNÍ KÓJE - D	6 m²
S.D.36	SKLEPNÍ KÓJE - D	5 m²
S.D.37	SKLEPNÍ KÓJE - D	4 m²
S.D.38	SKLEPNÍ KÓJE - D	3 m²
S.D.39	SKLEPNÍ KÓJE - D	6 m²
S.D.40	SKLEPNÍ KÓJE - D	5 m²
S.D.41	SKLEPNÍ KÓJE - D	3 m²
S.D.42	SKLEPNÍ KÓJE - D	3 m²
S.D.43	SKLEPNÍ KÓJE - D	3 m²

LEGENDA MATERIÁLŮ

- ŽELEZOBETON (WF 21)
- VODOSTAVEBNÍ BETON (WF 61)
- NOSNÉ ZDIVO - KERAMICKÁ TVÁRNICE (WF 10)
- NOSNÉ ZDIVO - AKUSTICKÉ KERAM. TVÁRNICE (WF20)
- PŘÍČKY - KERAMICKÁ TVÁRNICE (WF 3x)
- TEPELNÁ IZOLACE - EXTRUDOVANÝ POLYSTYREN

LEGENDA TAGŮ

- XF 01 — Označení specifikace skladby a povrchu; značení CF, WF, FF, RF. Viz D_01_0100_030 - Tabulka specifikace skladeb a povrchů
- D01 001 — Označení dveří. Viz D_01_100_041 - Tabulka dveří
- LP 01 — Označení zámečnických prvků. Viz D_01_100_050 - Tabulka zámečnických prvků
- TP 01 — Označení klempířských prvků. Viz D_01_100_060 - Tabulka klempířských prvků
- OP 001 — Označení ostatních prvků. Viz D_01_100_080 - Tabulka ostatních prvků
- W 01 — Označení oken. Viz D_01_100_040 - Tabulka výplně otvorů
- F 01 — Označení povrchů. Viz D_01_0100_030 - Tabulka specifikace skladeb a povrchů

POZN.:
VŠECHNY ČÁSTI PROJEKTOVÉ DOKUMENTACE A REALIZACE JEDNOTLIVÝCH PROFESNÍCH ČÁSTÍ (ARCHITEKTONICKÁ, STAVEBNĚ KONSTRUKČNÍ, TZB A DALŠÍ) PODLEHAJÍ KOORDINACI GENERÁLNÍHO PROJEKTANTA, V PŘÍPADĚ JAKÝCHKOLIV ROZPORŮ V PROJEKTOVÉ DOKUMENTACI NEBO V PRŮBĚHU REALIZACE JSOU ZHOTOVITELÉ/DODAVATELÉ JEDNOTLIVÝCH ČÁSTÍ POVINNI VYŽÁDAT SI STANOVISKO AUTORIZOVANÉ OSOBY A ARCHITEKTA.

KONSTRUKCE JSOU KÓTOVÁNY BEZ POVRCHOVÝCH ÚPRAV.

UVEDENÉ ROZMĚRY A POZICE KONSTRUKCÍ, INSTALAČNÍCH ROZVODŮ, KONCOVÝCH PRVKŮ APOD. JSOU JEN ORIENTAČNÍ. ZHOTOVITEL/DODAVATEL JE POVINEN ZAMĚŘIT SKUTEČNÝ STAV NA MÍSTĚ STAVBY. V PŘÍPADĚ ZMĚNY PODKLADŮ ČI VZNIKU NOVÝCH SKUTEČNOSTÍ JE NUTNÉ INFORMOVAT GP A DÁLE POSTUPOVAT AŽ PO KOORDINACI, VYDÁNÍ A SCHválENÍ ZMĚNY V PROJEKTOVÉ DOKUMENTACI.

DODAVATEL STAVBY MUSÍ DBÁT NA DODRŽOVÁNÍ MONTÁŽNÍCH A TECHNOLOGICKÝCH POKYNŮ PŘÍSLUŠNÝCH VÝROBCŮ STAVEBNÍCH PRVKŮ A KONSTRUKCÍ UVEDENÝCH V TÉTO DOKUMENTACI.

DOKUMENTACI JE MOŽNÉ UŽÍVAT VÝHRADNĚ A BEZ VÝJIMKY VE SMYSLU SMLOUVY O DÍLO. DOKUMENTACE JE POVAŽOVÁNA ZA RELEVANTNÍ JEN JAKO CELEK PODLE PLATNÉHO SEZNAMU DOKUMENTACE.

NAVRŽENÉ VÝROBKY A MATERIÁLY BUDOU ZHOTOVITELEM PŘEDLOŽENY KE SCHVÁLENÍ V RÁMCI VZORKOVÁNÍ. PŘESNÉ UMÍSTĚNÍ KONCOVÝCH PRVKŮ V PODHLEDECH BUDE REALIZOVÁNO PODLE VÝKRESU PODHLEDŮ V ARCHITEKTONICKO-STAVEBNÍ ČÁSTI.

PROJEKT INTERIÉRU JE ŘEŠEN SAMOSTATNOU DOKUMENTACÍ.

TATO PROJEKTOVÁ DOKUMENTACE BYLA ZPRACOVÁNA NA ZÁKLADĚ INFORMACÍ, PODKLADŮ A ZNALOSTÍ PLATNÝCH KE DNI JEJÍHO VYDÁNÍ A SLOUŽÍ VÝHRADNĚ PRO POTŘEBY UVEDENÉHO STUPNĚ DOKUMENTACE (NENAHRAZUJE PŘEDCHOZÍ NEBO NÁSLEDUJÍCÍ STUPNĚ). V PŘÍPADĚ ROZPORŮ MEZI JEDNOTLIVÝMI PŘÍLOHAMI NEBO PROFESNÍMI DÍLY JE POTŘEBNÉ NA TENTO ROZPOR UPOZORNIT A VYŽÁDAT SI OFICIÁLNÍ STANOVISKO GENERÁLNÍHO PROJEKTANTA.

N

±0,000 = 303,800 m n. m.
výškový systém: Bpv
souřadný systém: JTSK

projekt / project	číslo zakázky / project number: 18S-01

BYTOVÝ SOUBOR LIBUŠE

stupeň dokumentace / design stage
DOKUMENTACE PRO PROVEDENÍ STAVBY — DPS
DETAIL DESIGN DOCUMENTATION — DDD

klient / client
VELTON REAL ESTATE s.r.o.
Na Strži 2102/61a
140 00, Praha 4 - Kyč

architekt / architect
adns architekti
A.D.N.S. architekti s.r.o.
Na Příkopě 853/12
110 00 Praha 1 - Nové Město

generál projektant / general designer
ABMV world s.r.o.
Prosecká 527/24,180 00 Praha 8
tel.: +420 731 441 125

projektant / designer
ABMV world s.r.o.
Prosecká 527/24,180 00 Praha 8
tel.: +420 731 441 125

odpovědný projektant / designer: Ing. arch. Zdeněk Vávra
vypracoval / drawn by: Ing. Lukáš Vojta
kontroloval / checked by: Ing. Marek Veselý

revize / revision	popis / description	datum / date
R01	Tvar stavební jámy a opatření proti radonu, nadpraží oken bytů	30.11.2021

část dokumentace / documentation part
D — DOKUMENTACE OBJEKTŮ A TECHNICKÝCH A TECHNOLOGICKÝCH ZAŘÍZENÍ
stavební objekt / building object
SO01 — BYTOVÝ DŮM
profesní díl / specialist part
100 — ARCHITEKTONICKO-STAVEBNÍ ŘEŠENÍ

název výkresu / drawing title
PŮDORYS 1PP

datum revize 00 / revision date 00	měřítko / scale	podíl A4 / A4 count	paré
15/09/21	1:100	15 x A4	

číslo výkresu / sheet number: 4030
kód výkresu / sheet code: 18S-01_SP5_D_SO01_100_4030_R01