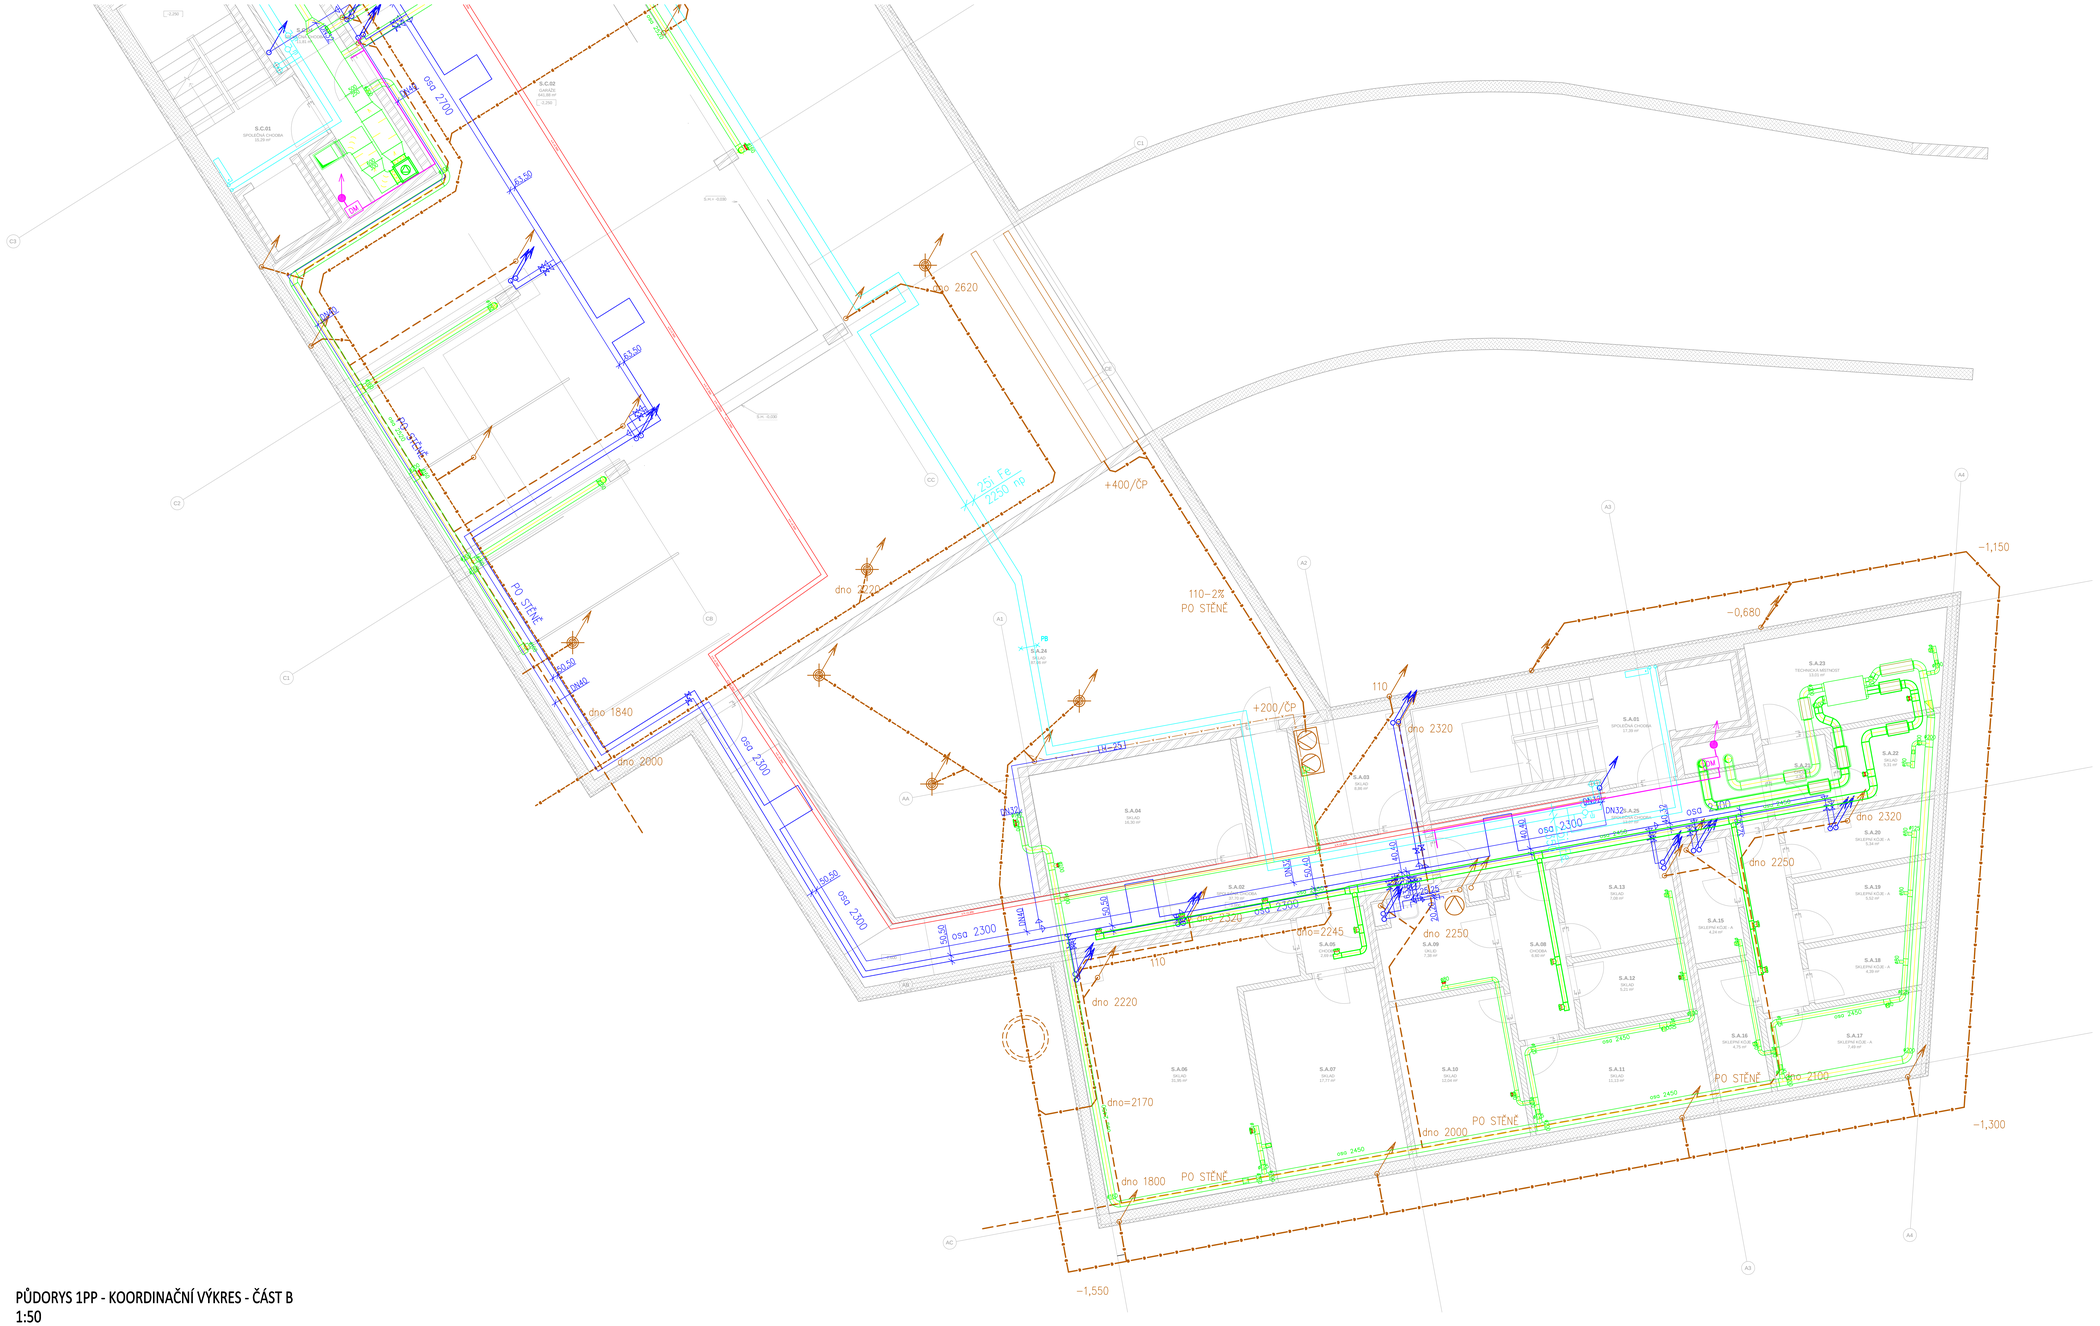


## PŮDORYS 1PP - KOORDINAČNÍ VÝKRES - ČÁST B
1:50

### Tabulka místností 1.PP

| Number | Name | Area |
|---|---|---|
| S.A.01 | SPOLEČNÁ CHODBA | 17 m² |
| S.A.02 | SPOLEČNÁ CHODBA | 38 m² |
| S.A.03 | SKLAD | 9 m² |
| S.A.04 | SKLAD | 16 m² |
| S.A.05 | CHODBA | 3 m² |
| S.A.06 | SKLAD | 32 m² |
| S.A.07 | SKLAD | 18 m² |
| S.A.08 | CHODBA | 7 m² |
| S.A.09 | ÚKLID | 7 m² |
| S.A.10 | SKLAD | 12 m² |
| S.A.11 | SKLAD | 11 m² |
| S.A.12 | SKLAD | 5 m² |
| S.A.13 | SKLAD | 7 m² |
| S.A.14 | CHODBA | 6 m² |
| S.A.15 | SKLEPNÍ KÓJE - A | 4 m² |
| S.A.16 | SKLEPNÍ KÓJE - A | 5 m² |
| S.A.17 | SKLEPNÍ KÓJE - A | 7 m² |
| S.A.18 | SKLEPNÍ KÓJE - A | 4 m² |
| S.A.19 | SKLEPNÍ KÓJE - A | 6 m² |
| S.A.20 | SKLEPNÍ KÓJE - A | 5 m² |
| S.A.21 | CHODBA | 3 m² |
| S.A.22 | SKLAD | 5 m² |
| S.A.23 | TECHNICKÁ MÍSTNOST | 13 m² |
| S.A.24 | SKLAD | 87 m² |
| S.A.25 | SPOLEČNÁ CHODBA | 13 m² |
| S.B.01 | SPOLEČNÁ CHODBA | 15 m² |
| S.B.02 | GARÁŽE | 424 m² |
| S.B.03 | SPOLEČNÁ CHODBA | 12 m² |
| S.C.01 | SPOLEČNÁ CHODBA | 15 m² |
| S.C.02 | GARÁŽE | 642 m² |
| S.C.03 | GARÁŽE | 69 m² |
| S.C.04 | SPOLEČNÁ CHODBA | 12 m² |
| S.D.01 | SPOLEČNÁ CHODBA | 15 m² |
| S.D.02 | SPOLEČNÁ CHODBA | 18 m² |
| S.D.03 | SPOLEČNÁ CHODBA | 10 m² |
| S.D.04 | SKLAD | 7 m² |
| S.D.05 | SKLAD | 6 m² |
| S.D.06 | SKLAD | 6 m² |
| S.D.07 | SKLAD | 8 m² |
| S.D.08 | ÚKLID | 4 m² |
| S.D.09 | CHODBA | 15 m² |
| S.D.10 | SKLEPNÍ KÓJE - C | 4 m² |
| S.D.11 | SKLEPNÍ KÓJE - C | 3 m² |
| S.D.12 | SKLEPNÍ KÓJE - C | 3 m² |
| S.D.13 | SKLEPNÍ KÓJE - C | 5 m² |
| S.D.14 | SKLEPNÍ KÓJE - C | 6 m² |
| S.D.15 | SKLEPNÍ KÓJE - C | 8 m² |
| S.D.16 | SKLEPNÍ KÓJE - C | 8 m² |
| S.D.17 | SKLEPNÍ KÓJE - C | 4 m² |
| S.D.18 | SKLEPNÍ KÓJE - C | 4 m² |
| S.D.19 | SKLEPNÍ KÓJE - C | 4 m² |
| S.D.20 | CHODBA | 13 m² |
| S.D.21 | SKLEPNÍ KÓJE - B | 3 m² |
| S.D.22 | SKLEPNÍ KÓJE - B | 4 m² |
| S.D.23 | SKLEPNÍ KÓJE - B | 4 m² |
| S.D.24 | SKLEPNÍ KÓJE - B | 4 m² |
| S.D.25 | SKLEPNÍ KÓJE - B | 5 m² |
| S.D.26 | SKLEPNÍ KÓJE - B | 4 m² |
| S.D.27 | SKLEPNÍ KÓJE - B | 4 m² |
| S.D.28 | SKLEPNÍ KÓJE - B | 3 m² |
| S.D.29 | SKLEPNÍ KÓJE - B | 4 m² |
| S.D.30 | SPOLEČNÁ CHODBA | 5 m² |
| S.D.31 | TECHNICKÁ MÍSTNOST | 13 m² |
| S.D.32 | CHODBA | 12 m² |
| S.D.33 | SKLEPNÍ KÓJE - D | 3 m² |
| S.D.34 | SKLEPNÍ KÓJE - D | 5 m² |
| S.D.35 | SKLEPNÍ KÓJE - D | 6 m² |
| S.D.36 | SKLEPNÍ KÓJE - D | 5 m² |
| S.D.37 | SKLEPNÍ KÓJE - D | 4 m² |
| S.D.38 | SKLEPNÍ KÓJE - D | 3 m² |
| S.D.39 | SKLEPNÍ KÓJE - D | 6 m² |
| S.D.40 | SKLEPNÍ KÓJE - D | 5 m² |
| S.D.41 | SKLEPNÍ KÓJE - D | 3 m² |
| S.D.42 | SKLEPNÍ KÓJE - D | 3 m² |
| S.D.43 | SKLEPNÍ KÓJE - D | 3 m² |
| S.D.44 | SPOLEČNÁ CHODBA | 12 m² |

### SCHEMA ROZVRŽENÍ - KLAD LISTŮ

Legenda rozvodů a zařízení

- vzduchotechnika
- chlazení
- vytápění
- vodovod
- kanalizace
- silnoproud
- slaboproudy
- plyn

| | |
|---|---|
| projekt / project | číslo zakázky / project number: 100-01 |
| BYTOVÝ SOUBOR LIBUŠE | |
| stupeň dokumentace / design stage | |
| DOKUMENTACE PRO PROVEDENÍ STAVBY | DPS |
| DETAIL DESIGN DOCUMENTATION | DDD |
| investor / client | VELTON REAL ESTATE<br>Na Strži 2102/61a<br>140 00, Praha 4 - Krč |
| architekt / architect | adns architekti — A.D.N.S. architekti s.r.o.<br>Na Příkopě 853/12<br>110 00 Praha 1- Nové Město |
| generální projektant / general designer | ABMV world s.r.o.<br>Provazská 521/24<br>180 00 Praha 8 |
| projektant / designer | ABMV world s.r.o.<br>Provazská 521/24<br>180 00 Praha 8 |
| zodpovědný projektant / designer | Ing. arch. Zdeněk Vávra |
| vypracoval / drawn by | Štěpán Šustr |
| kontroloval / checked by | Ing. Marek Veselý |

| revize / revision | popis / description | datum / date |
|---|---|---|
| 000 | stručný popis revize | datum vydání revize |

část dokumentace / documentation part: D — DOKUMENTACE OBJEKTŮ A TECHNOLOGICKÝCH ZAŘÍZENÍ

stavební objekt / building object: SO01 - BYTOVÝ DŮM

profesní díl / speciality part: 100 — ARCHITEKTONICKO-STAVEBNÍ ŘEŠENÍ

název výkresu / drawing title: PŮDORYS 1PP - KOORDINAČNÍ VÝKRES - ČÁST B

| datum revize 00 / revision date 00 | měřítko / scale | podíl A4 / A4 count | perf |
|---|---|---|---|
| 15/09/2021 | 1:50 | 2 | 1 x A4 | |

číslo výkresu / sheet number: 9001

kód výkresu / sheet code: 18001_DPS_D_SO01_100_9001_A01

S-JTSK / S-JTSK/05 m.n.m. Křováková systém Bpv
Jaa Pacholík systém ČSN