HALA – KONSTRUKCE

M1:100

PŮDORYS

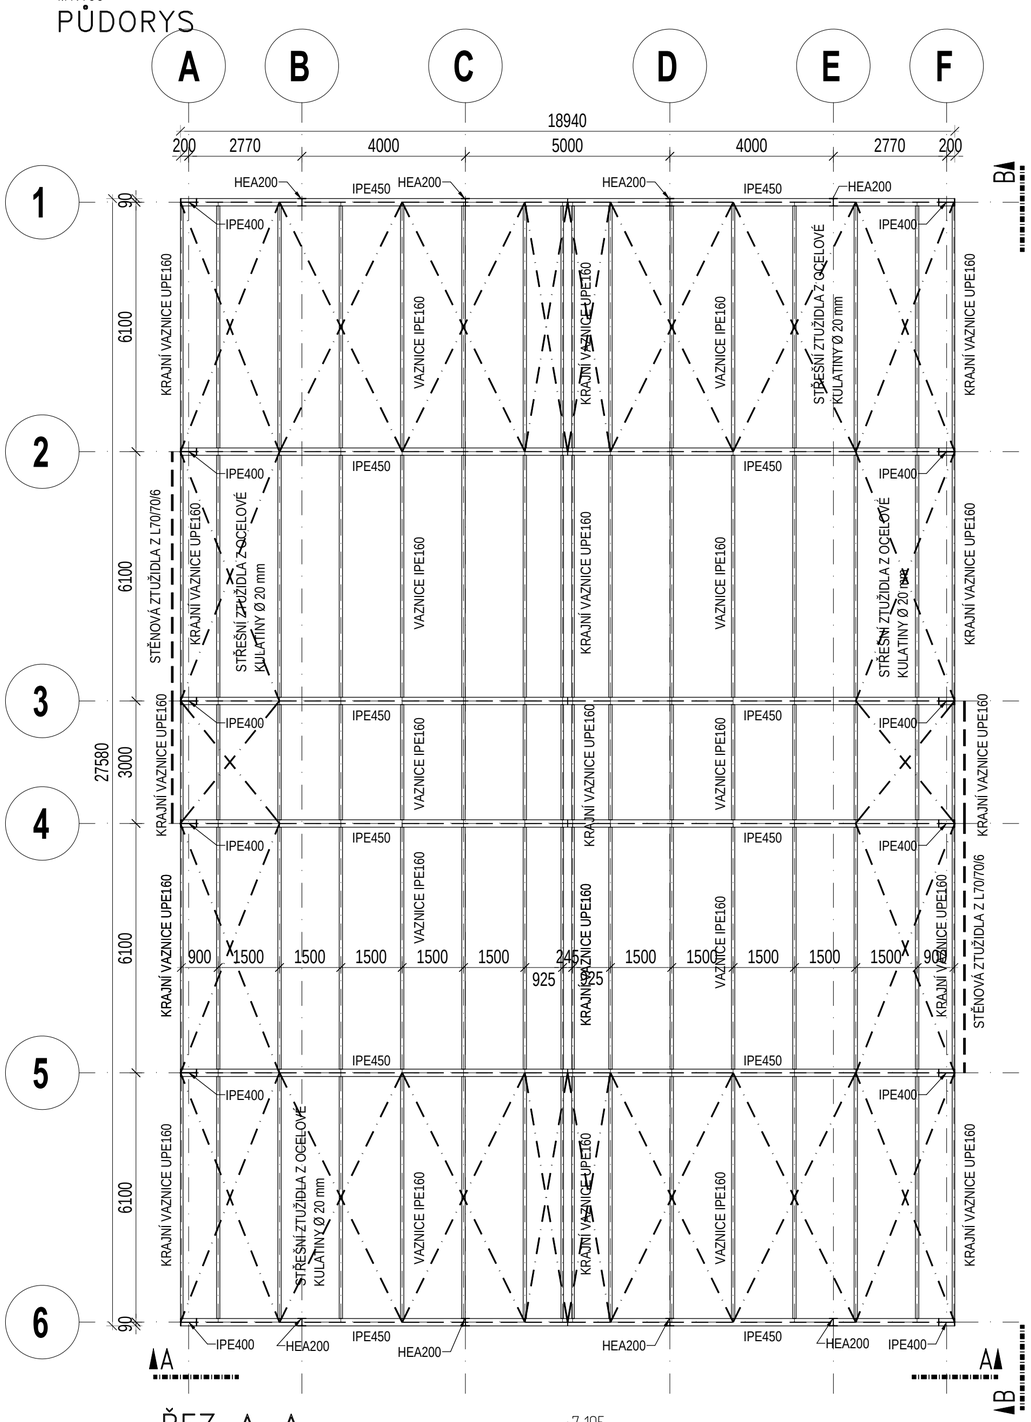

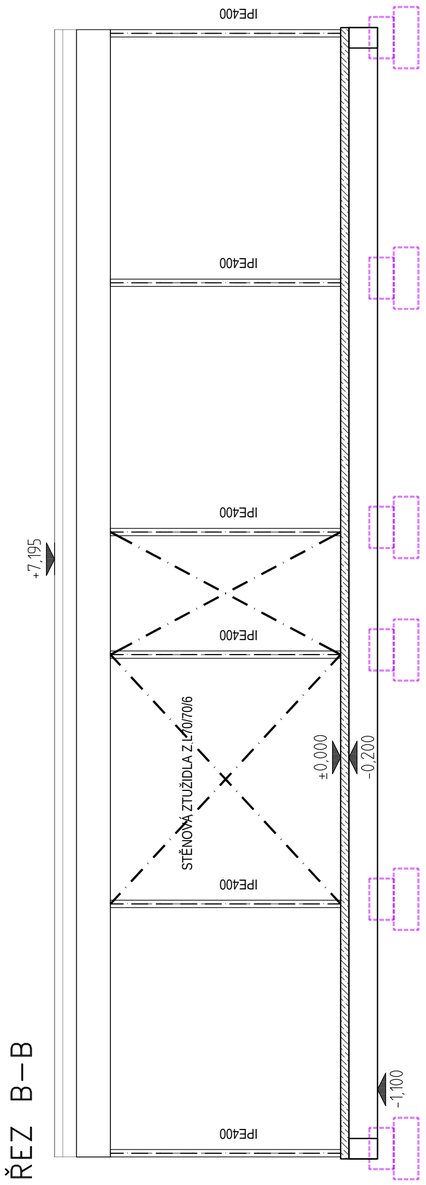

ŘEZ B–B

ŘEZ A–A

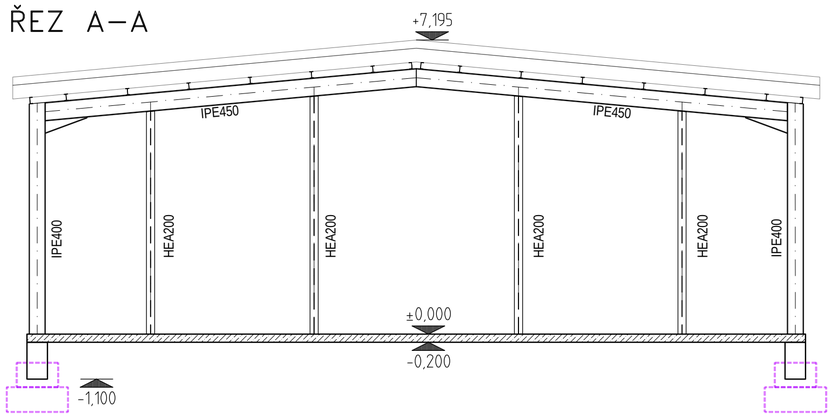

MATERIÁL:

KONSTRUKČNÍ OCEL ČSN EN 10025

S235

PROFILY, STYČNÍKOVÉ PLECHY

SPOJOVACÍ PRVKY

8.8

SVORNÍKY, KOLÍKY, ČEPY

Poznámky:

- Při provádění je potřeba posutpovat podle nejnovější revize výkresů.
- Před prováděním je potřeba porovnat výkresy stavebně konstrukční a architektonicko-stavební části a na případné rozpory upozornit hlavního inženýra projektu a statika
- Dokumentace je vypracovaná ve stupni dokumentace pro stavební povolení a nenahrazuje prováděcí dokumentaci. Cílem posudku je ověřit proveditelnost konstrukce a předpokládá se v pokračování projekčních prací v dalším stupni.

LEGENDA:

- ZDIVO POD DESKOU
- ŽELEZOBETON POD DESKOU
- ZDIVO NAD DESKOU
- ŽELEZOBETON NAD DESKOU
- ZDIVO V ŘEZU
- ŽELEZOBETON ŘEZU
- BETON V ŘEZU
- PROSTUPY DESKOU

AKCE: HALA HRADEC KRÁLOVÉ SOLAR DISPOREC VÁŽNÍ 857		PROJEKTOVÝ STUPEŇ: DSP	
INVESTOR: SOLAR DISPOREC s.r.o, Malostranské náměstí 5/28, Malá Strana (Praha 1), 118 00 Praha	PROJEKTANT ČÁSTI: Vypracoval: Bc. Martin Doležal, ADRESA: Jeseniova 381, Poděbrady, IČO: 21981078, TEL: 606 287 393, EMAIL: dolezalmpodebrady@seznam.cz	AUTORIZAČNÍ RAZÍTKO: Ing. JIŘÍ PLACHÝ, Autorizovaný inženýr pro statiku a dynamiku stavby, ČKAIT - 0013051	PARÉ Č.:
AUTOR NÁVRHU: Ing. arch Jakub Volka, Kristián Pócsik		DATUM: 09/2025	SLOŽKA: D.2.3
ZODP. PROJEKT.: Ing. Jiří Plachý, ČKAIT 0013051		MĚŘÍTKO: 1:100	
VYPRACOVAL: Bc. Martin Doležal		FORMÁT: 6 x A4	
VÝKRES: HALA - KONSTRUKCE		ČÁST DOKUMENTACE: STAVEBNĚ KONSTRUKČNÍ	V.Č.: 02

REV00