OBJEKT A - PŮDORYS 1NP - KOORDINAČNÍ VÝKRES
1:50

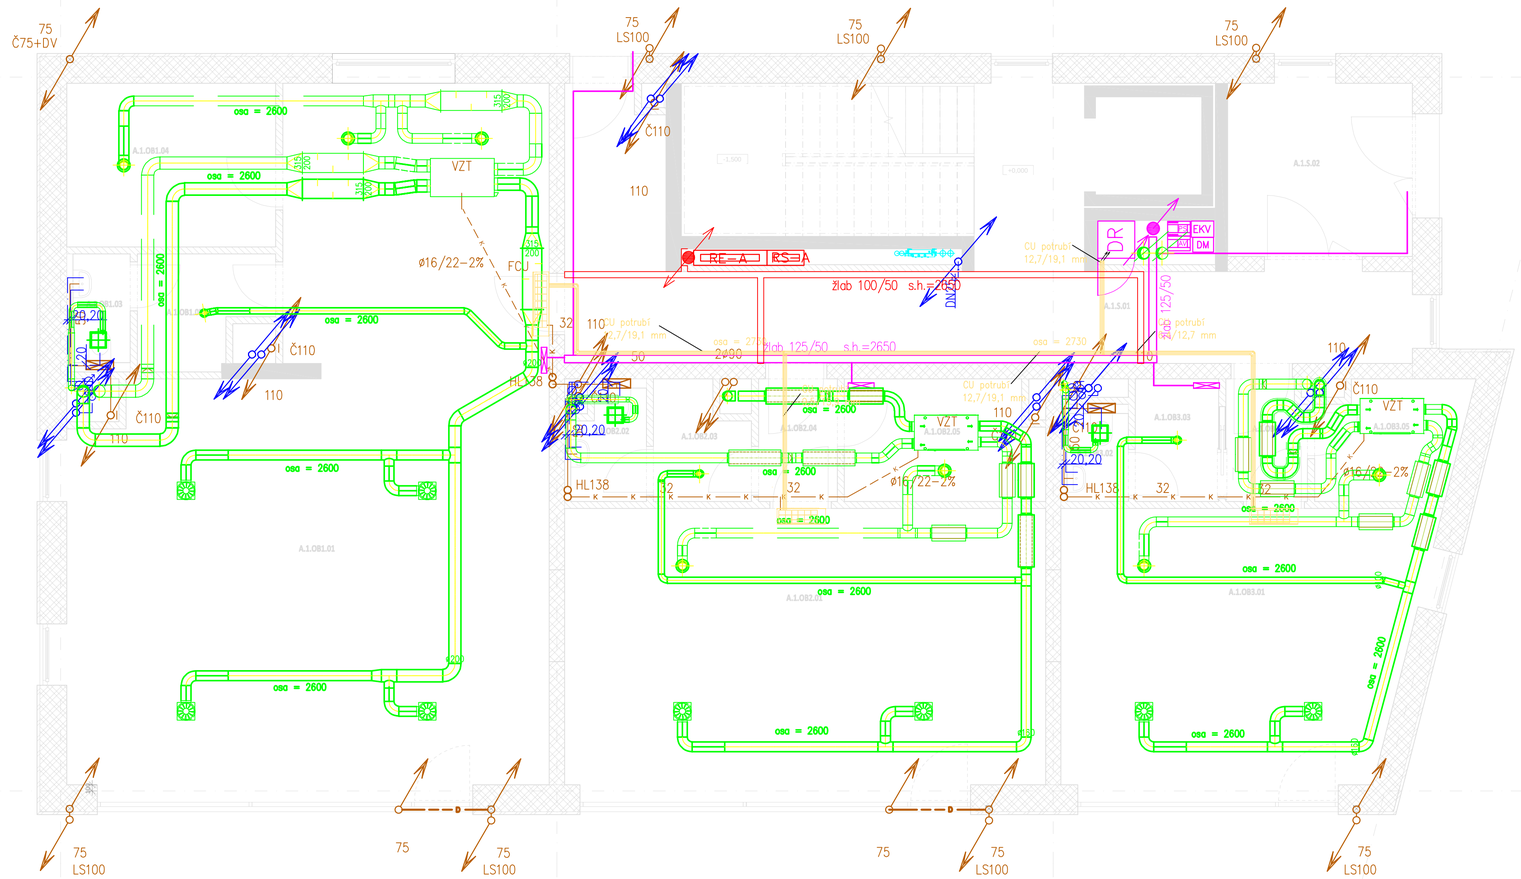

Legenda rozvodů a zařízení

- vzduchotechnika
- chlazení
- vytápění
- vodovod (horizontální rozvody v bytech jsou vedeny v podlaze nebo max. ve výšce 1,3m)
- kanalizace
- silnoproud
- slaboproudy

Tabulka místností 1.NP

Number	Name	Area
A.1.0B1.01	OBCHODNÍ JEDNOTKA	72 m²
A.1.0B1.02	ŠATNA	3 m²
A.1.0B1.03	WC	2 m²
A.1.0B1.04	SKLAD	9 m²
A.1.0B2.01	OBCHODNÍ JEDNOTKA	35 m²
A.1.0B2.02	WC	2 m²
A.1.0B2.03	ŠATNA	3 m²
A.1.0B2.04	CHODBA	3 m²
A.1.0B2.05	SKLAD	6 m²
A.1.0B3.01	OBCHODNÍ JEDNOTKA	25 m²
A.1.0B3.02	WC	2 m²
A.1.0B3.03	ŠATNA	3 m²
A.1.0B3.04	CHODBA	3 m²
A.1.0B3.05	SKLAD	4 m²
A.1.5.01	ZÁDVEŘÍ	9 m²
A.1.5.02	SPOLEČNÁ CHODBA	28 m²
A.1.5.03	SPOLEČNÁ CHODBA	5 m²

projekt / project — *číslo zakázky / project number:* 185-01

BYTOVÝ SOUBOR LIBUŠE

stupeň dokumentace / design stage

DOKUMENTACE PRO PROVEDENÍ STAVBY — DPS
DETAIL DESIGN DOCUMENTATION — DDD

klient / client

VELTON REAL ESTATE
Na Strži 2102/61a
140 00, Praha 4 - Krč

architekt / architect

adns architekti
A.D.N.S. architekti s.r.o.
Na Příkopě 853/12
110 00 Praha 1 - Nové Město

generální projektant / general designer

ABMV WORLD
ABMV world s.r.o.
Prosecká 527/24
180 00 Praha 8

projektant / designer

ABMV WORLD
ABMV world s.r.o.
Prosecká 527/24
180 00 Praha 8

odpovědný projektant / designer
Ing. arch. Zdeněk Vávra

vypracoval / drawn by
Štěpán Šustr

kontroloval / checked by
Ing. Marek Veselý

revize / revision	*popis / description*	*datum / date*
RR#	*stručný popis revize*	*datum vydání revize*

část dokumentace / documentation part

D | DOKUMENTACE OBJEKTŮ A TECHNICKÝCH A TECHNOLOGICKÝCH ZAŘÍZENÍ

stavební objekt / building object

SO01 | BYTOVÝ DŮM

profesní díl / specialist part

110 | ARCHITEKTONICKO-STAVEBNÍ ŘEŠENÍ - OBJEKT A, NADZEMNÍ ČÁST

název výkresu / drawing title

OBJEKT A - KOORDINAČNÍ VÝKRES 1.NP

datum revize 00 / revision date 00	*měřítko / scale*	*počet A4 / A4 count*
15.09.2021	1:50	8 x A4

číslo výkresu / sheet number 9110

kód výkresu / sheet code 18501_DPS_D_SO01_110_9110_R00

paré

±0.000 = 303,800 m n. m.
výškový systém: Bpv
souřadný systém: JTSK