# OBJEKT A - PŮDORYS 2NP - KOORDINAČNÍ VÝKRES
1:50

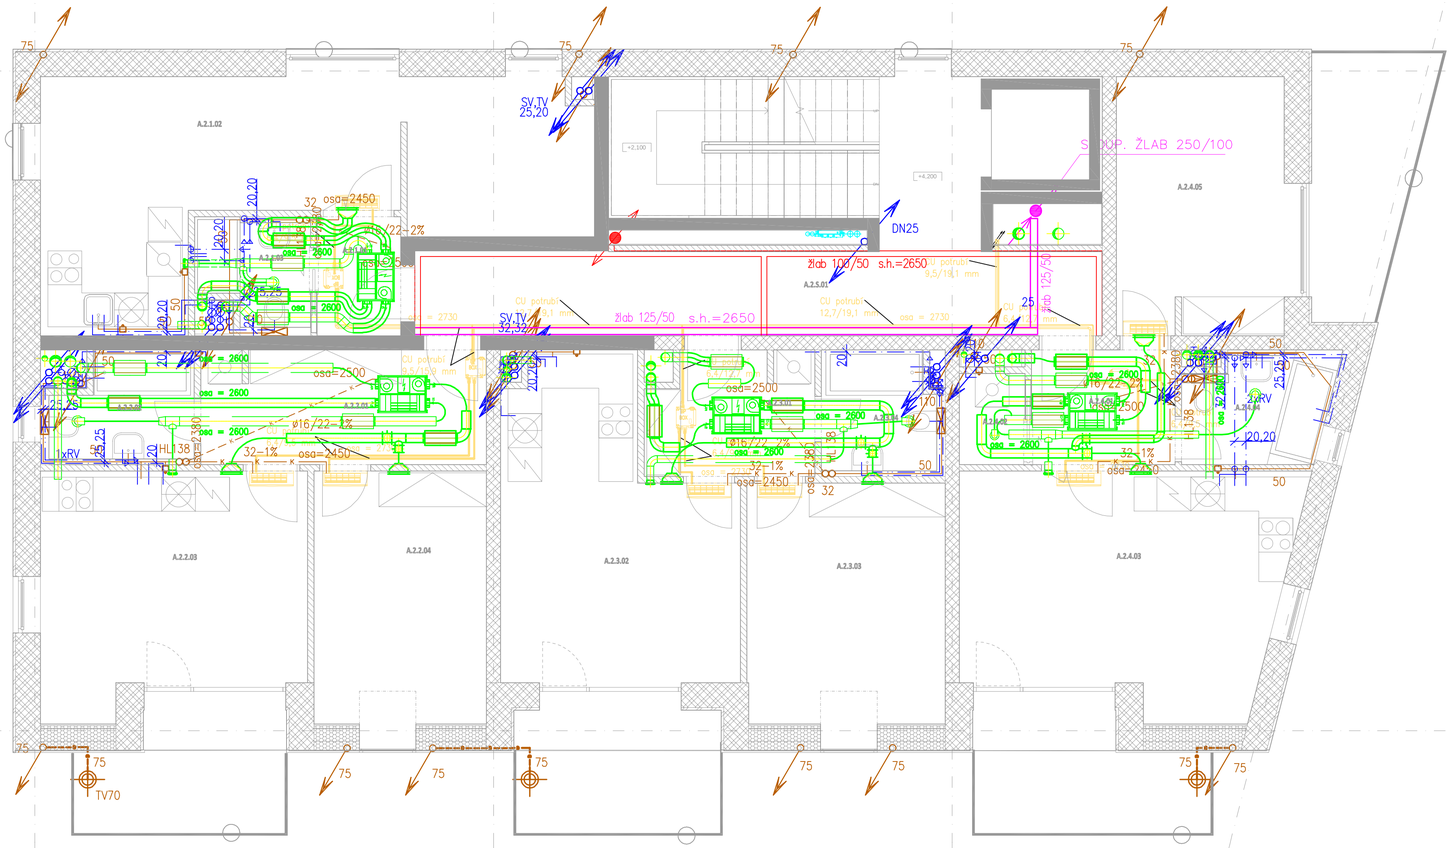


## Legenda rozvodů a zařízení

- vzduchotechnika
- chlazení
- vytápění
- vodovod (horizontální rozvody v bytech jsou vedeny v podlaze nebo max. ve výšce 1,3m)
- kanalizace
- silnoproud
- slaboproudy

**Tabulka místností 2.NP**

| Number | Name | Area |
|---|---|---|
| A.2.1.01 | CHODBA | 3 m² |
| A.2.1.02 | OBYVACÍ POKOJ + KK | 29 m² |
| A.2.1.03 | KOUPELNA | 3 m² |
| A.2.2.01 | CHODBA | 10 m² |
| A.2.2.02 | KOUPELNA | 5 m² |
| A.2.2.03 | OBYVACÍ POKOJ + KK | 18 m² |
| A.2.2.04 | POKOJ | Not Enclosed |
| A.2.3.01 | CHODBA | 6 m² |
| A.2.3.02 | OBYVACÍ POKOJ + KK | 20 m² |
| A.2.3.03 | POKOJ | 15 m² |
| A.2.3.04 | KOUPELNA | 4 m² |
| A.2.4.01 | CHODBA | 5 m² |
| A.2.4.02 | KOMORA | 2 m² |
| A.2.4.03 | OBYVACÍ POKOJ + KK | 23 m² |
| A.2.4.04 | KOUPELNA | 5 m² |
| A.2.4.05 | POKOJ | 13 m² |
| A.2.5.01 | SPOLEČNÁ CHODBA | 5 m² |
| A.2.5.02 | SPOLEČNÁ CHODBA | 18 m² |

projekt / project — číslo zakázky / project number: 185-01

BYTOVÝ SOUBOR LIBUŠE

stupeň dokumentace / design stage

DOKUMENTACE PRO PROVEDENÍ STAVBY — DPS

DETAIL DESIGN DOCUMENTATION — DDD


ilient / client

VELTON REAL ESTATE
Na Strži 2102/61a
140 00, Praha 4 - Krč

architekt / architect

adns architekti
A.D.N.S. architekti s.r.o.
Na Příkopě 853/12
110 00 Praha 1 - Nové Město

generální projektant / general designer

ABMV WORLD
ABMV world s.r.o.
Prosecká 527/24
180 00 Praha 8

projektant / designer

ABMV WORLD
ABMV world s.r.o.
Prosecká 527/24
180 00 Praha 8

odpovědný projektant / designer
Ing. arch. Zdeněk Vávra

vypracoval / drawn by
Štěpán Šustr

kontroloval / checked by
Ing. Marek Veselý


| revize / revision | popis / description | datum / date |
|---|---|---|
| RM | stručný popis revize | datum vydání revize |

část dokumentace / documentation part

D | DOKUMENTACE OBJEKTŮ A TECHNICKÝCH A TECHNOLOGICKÝCH ZAŘÍZENÍ

stavební objekt / building object

SO01 | BYTOVÝ DŮM

profesní díl / specialist part

110 | ARCHITEKTONICKO-STAVEBNÍ ŘEŠENÍ - OBJEKT A, NADZEMNÍ ČÁST

N

±0.000 = 303,800 m n. m.
výškový systém: Bpv
souřadný systém: JTSK

název výkresu / drawing title

OBJEKT A - KOORDINAČNÍ VÝKRES 2.NP

| datum revize 00 / revision date 00 | měřítko / scale | počet A4 / A4 count | paré |
|---|---|---|---|
| 15.09.2021 | 1:50 | 8 x A4 | |

číslo výkresu / sheet number: 9120

kód výkresu / sheet code: 185D1_DPS_D_SO01_110_9120_R00