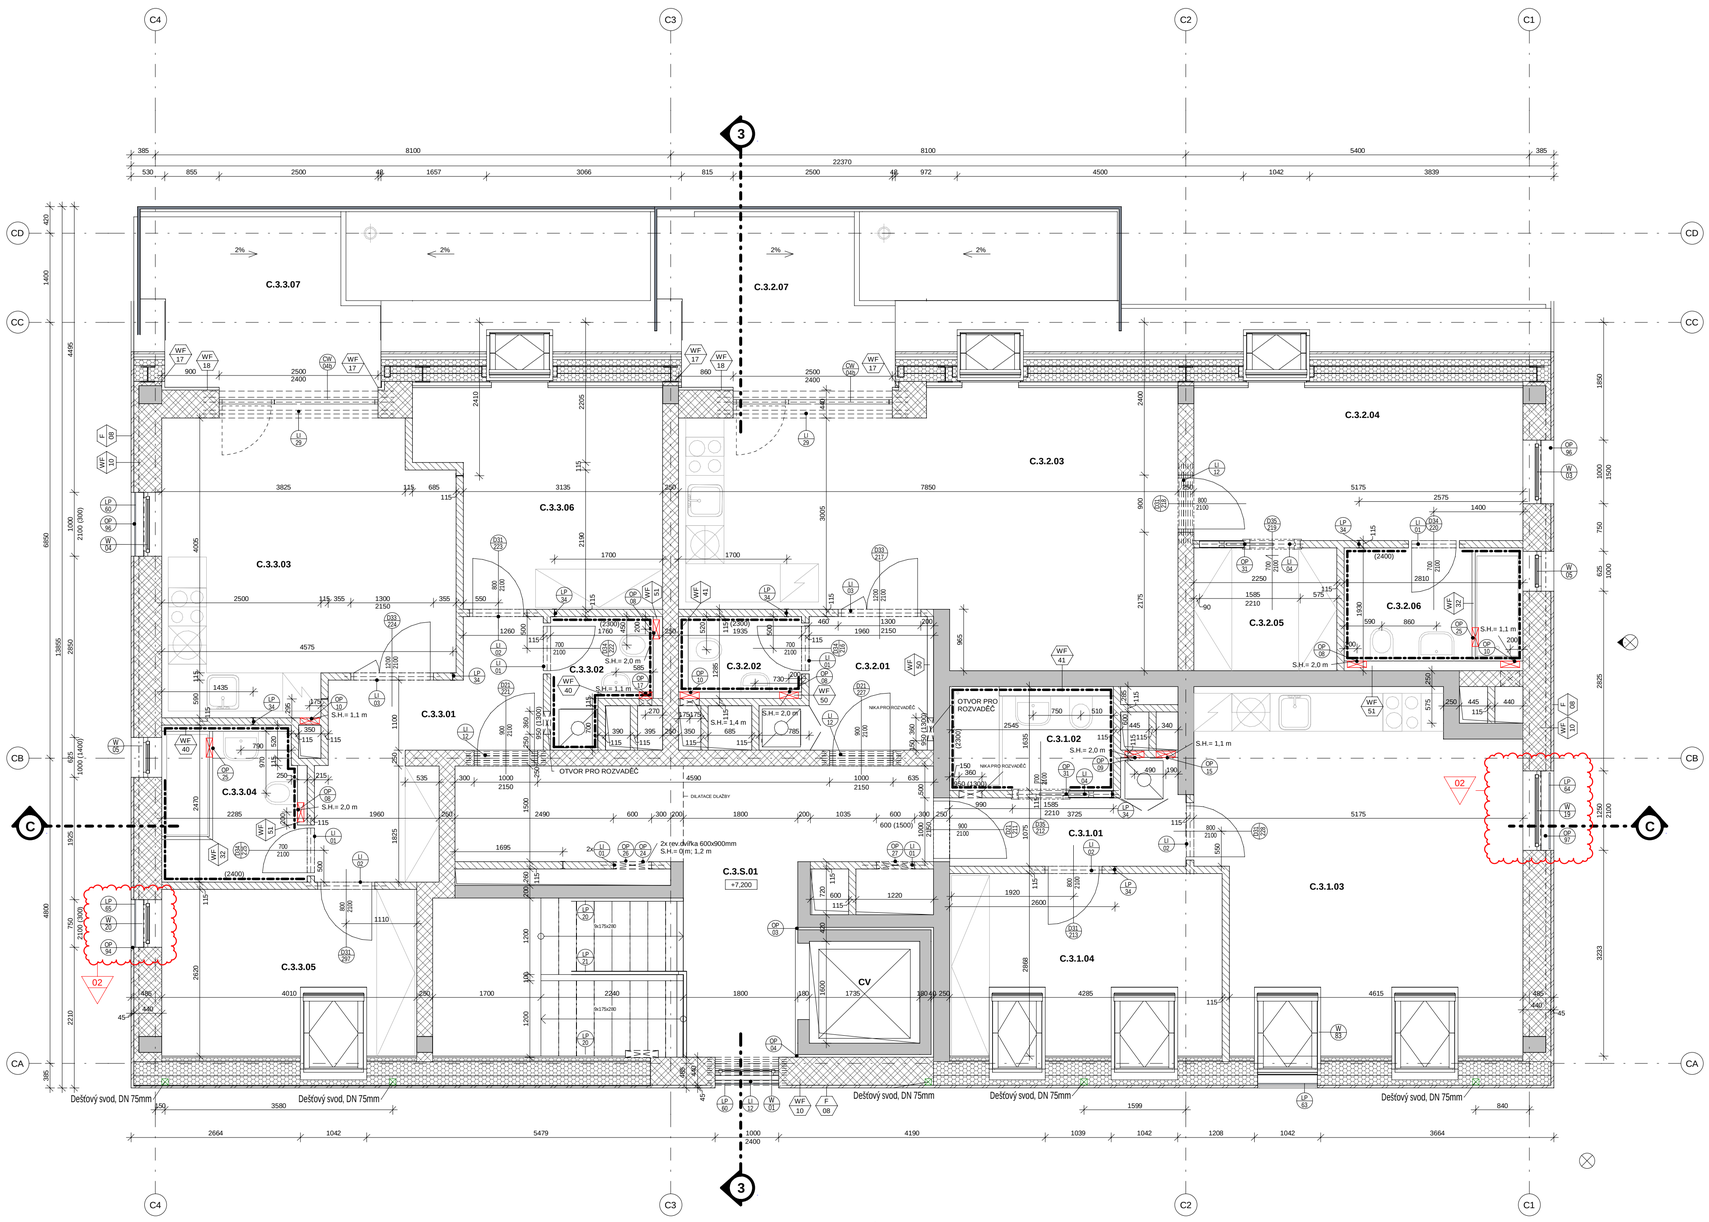

LEGENDA MATERIÁLŮ

- ŽELEZOBETON (WF 21)
- NOSNÉ ZDIVO - KERAMICKÁ TVÁRNICE (WF 10)
- NOSNÉ ZDIVO - AKUSTICKÉ KERAM. TVÁRNICE (WF20)
- PŘÍČKY - KERAMICKÁ TVÁRNICE (WF 3x)
- SDK PŘEDSTĚNY (WF 4x)
- TEPELNÁ IZOLACE - MINERÁLNÍ VATA
- CIHELNÉ PÁSKY TERCA (FOB)

LEGENDA TAGŮ

- XF 01 — Označení specifikace skladby a povrchu; značení CF, WF, FF, RF. Viz D_01_100_030 - Tabulka specifikace skladeb a povrchů
- D01 001 — Označení dveří. Viz D_01_100_041 - Tabulka dveří
- LP 01 — Označení zámečnických prvků. Viz D_01_100_050 - Tabulka zámečnických prvků
- TP 01 — Označení klempířských prvků. Viz D_01_100_060 - Tabulka klempířských prvků
- OP 001 — Označení ostatních prvků. Viz D_01_100_080 - Tabulka ostatních prvků
- W 01 — Označení oken. Viz D_01_100_040 - Tabulka výplně otvorů
- CW 001 — Označení prosklených příček. Viz D_01_100_040 - Tabulka výplně otvorů

Tabulka místností 3.NP

Č. místnosti	Název	Plocha
C.3.1		
C.3.1.01	CHODBA	4,6 m²
C.3.1.02	KOUPELNA	4,2 m²
C.3.1.03	OBÝVACÍ POKOJ + KK	27,4 m²
C.3.1.04	POKOJ	12,3 m²
C.3.1: 4		48,4 m²
C.3.2		
C.3.2.01	CHODBA	4,5 m²
C.3.2.02	WC	2,3 m²
C.3.2.03	OBÝVACÍ POKOJ + KK	28,9 m²
C.3.2.04	POKOJ	12,4 m²
C.3.2.05	ŠATNA	4,3 m²
C.3.2.06	KOUPELNA	5,0 m²
C.3.2.07	BALKON	15,1 m²
C.3.2: 7		72,6 m²
C.3.3		
C.3.3.01	CHODBA	8,9 m²
C.3.3.02	WC	2,7 m²
C.3.3.03	OBÝVACÍ POKOJ + KK	19,6 m²
C.3.3.04	KOUPELNA	5,4 m²
C.3.3.05	POKOJ	10,5 m²
C.3.3.06	POKOJ	11,9 m²
C.3.3.07	BALKON	16,5 m²
C.3.3: 7		75,4 m²
Společné prostory		
C.3.S.01	SPOLEČNÁ CHODBA	17,1 m²
Společné prostory: 1		17,1 m²

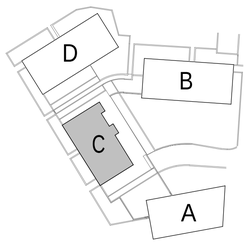

POZN.:
VŠECHNY ČÁSTI PROJEKTOVÉ DOKUMENTACE A REALIZACE JEDNOTLIVÝCH PROFESNÍCH ČÁSTÍ (ARCHITEKTONICKÁ, STAVEBNĚ KONSTRUKČNÍ, TZB A DALŠÍ) PODLEHAJÍ KOORDINACI GENERÁLNÍHO PROJEKTANTA. V PŘÍPADĚ JAKÝCHKOLIV ROZPORŮ V PROJEKTOVÉ DOKUMENTACI NEBO V PRŮBĚHU REALIZACE JSOU ZHOTOVITELÉ/DODAVATELÉ JEDNOTLIVÝCH ČÁSTÍ POVINNI VYŽÁDAT SI STANOVISKO AUTORIZOVANÉ OSOBY A ARCHITEKTA.

KONSTRUKCE JSOU KÓTOVÁNY BEZ POVRCHOVÝCH ÚPRAV.

UVEDENÉ ROZMĚRY A POZICE KONSTRUKCÍ, INSTALAČNÍCH ROZVODŮ, KONCOVÝCH PRVKŮ APOD. JSOU JEN ORIENTAČNÍ, ZHOTOVITEL/DODAVATEL JE POVINEN ZAMĚŘIT SKUTEČNÝ STAV NA MÍSTĚ STAVBY. V PŘÍPADĚ ZMĚNY PODKLADŮ ČI VZNIKU NOVÝCH SKUTEČNOSTÍ JE NUTNÉ INFORMOVAT GP A DÁLE POSTUPOVAT AŽ PO KOORDINACI, VYDÁNÍ A SCHválení ZMĚNY V PROJEKTOVÉ DOKUMENTACI.

DODAVATEL STAVBY MUSÍ DBÁT NA DODRŽOVÁNÍ MONTÁŽNÍCH A TECHNOLOGICKÝCH POKYNŮ PŘÍSLUŠNÝCH VÝROBCŮ STAVEBNÍCH PRVKŮ A KONSTRUKCÍ UVEDENÝCH V TÉTO DOKUMENTACI.

DOKUMENTACI JE MOŽNÉ UŽÍVAT VÝHRADNĚ A BEZ VYJÍMKY VE SMYSLU SMLOUVY O DÍLO. DOKUMENTACE JE POVAŽOVÁNA ZA RELEVANTNÍ JEN JAKO CELEK PODLE PLATNÉHO SEZNAMU DOKUMENTACE.

NAVRŽENÉ VÝROBKY A MATERIÁLY BUDOU ZHOTOVITELEM PŘEDLOŽENÉ KE SCHVÁLENÍ V RÁMCI VZORKOVÁNÍ. PŘESNÉ UMÍSTĚNÍ KONCOVÝCH PRVKŮ V PODHLEDECH BUDE REALIZOVANÉ PODLE VÝKRESU PODHLEDŮ V ARCHITEKTONICKO-STAVEBNÍ ČÁSTI.

PROJEKT INTERIÉRU JE ŘEŠEN SAMOSTATNOU DOKUMENTACÍ.

TATO PROJEKTOVÁ DOKUMENTACE BYLA ZPRACOVÁNA NA ZÁKLADĚ INFORMACÍ, PODKLADŮ A ZNALOSTÍ PLATNÝCH KE DNI JEJÍHO VYDÁNÍ A SLOUŽÍ VÝHRADNĚ PRO POTŘEBY UVEDENÉHO STUPNĚ DOKUMENTACE (NENAHRAZUJE PŘEDCHOZÍ NEBO NÁSLEDUJÍCÍ STUPNĚ). V PŘÍPADĚ ROZPORU MEZI JEDNOTLIVÝMI PŘÍLOHAMI NEBO PROFESNÍMI DÍLY JE POTŘEBNÉ NA TENTO ROZPOR UPOZORNIT A VYŽÁDAT SI OFICIÁLNÍ STANOVISKO GENERÁLNÍHO PROJEKTANTA.

±0,000 = 303,800 m n. m.
výškový systém: Bpv
souřadný systém: JTSK

projekt / project — *číslo zakázky / project number:* 185-01

BYTOVÝ SOUBOR LIBUŠE

stupeň dokumentace / design stage

DOKUMENTACE PRO PROVEDENÍ STAVBY — DPS
DETAIL DESIGN DOCUMENTATION — DDD

klient / client

VELTON REAL ESTATE
Na Strži 2102/61a
140 00, Praha 4 - Krč

architekt / architect

adns architekti
A.D.N.S. architekti s.r.o.
Na Příkopě 853/12
110 00 Praha 1 - Nové Město

general projektant / general designer

ABMV WORLD
ABMV world s.r.o.
Prosecká 527/24,180 00 Praha 8
tel.: +420 731 441 125

projektant / designer

ABMV WORLD
ABMV world s.r.o.
Prosecká 527/24,180 00 Praha 8
tel.: +420 731 441 125

odpovědný projektant / designer | Ing. arch. Zdeněk Vávra

vypracoval / drawn by | Ing. Lukáš Vojta

kontroloval / checked by | Ing. Marek Veselý

revize / revision	popis / description	datum / date
01	Spádování balkónů	30.11.2021
02	Oprava výměr OP a úprava zobrazení místností C.1.1.04	11.04.2022

část dokumentace / documentation part | D | DOKUMENTACE OBJEKTŮ A TECHNICKÝCH A TECHNOLOGICKÝCH ZAŘÍZENÍ

stavební objekt / building object | SO01 | BYTOVÝ DŮM

profesní díl / specialist part | 130 | ARCHITEKTONICKO-STAVEBNÍ ŘEŠENÍ, OBJEKT C - NADZEMNÍ ČÁST

název výkresu / drawing title

OBJEKT C - Půdorys 3. NP

datum revize 00 / revision date 00	měřítko / scale	počet A4 / A4 count	paré
15/09/2021	1:50	8 x A4	

číslo výkresu / sheet number 4330

kód výkresu / sheet code 185-01_DPS_D_SO01_130_4330_02