




TVAR A VÝZTUŽ ŘÍMS
PŮDORYSNÉ SCHÉMA 1:200

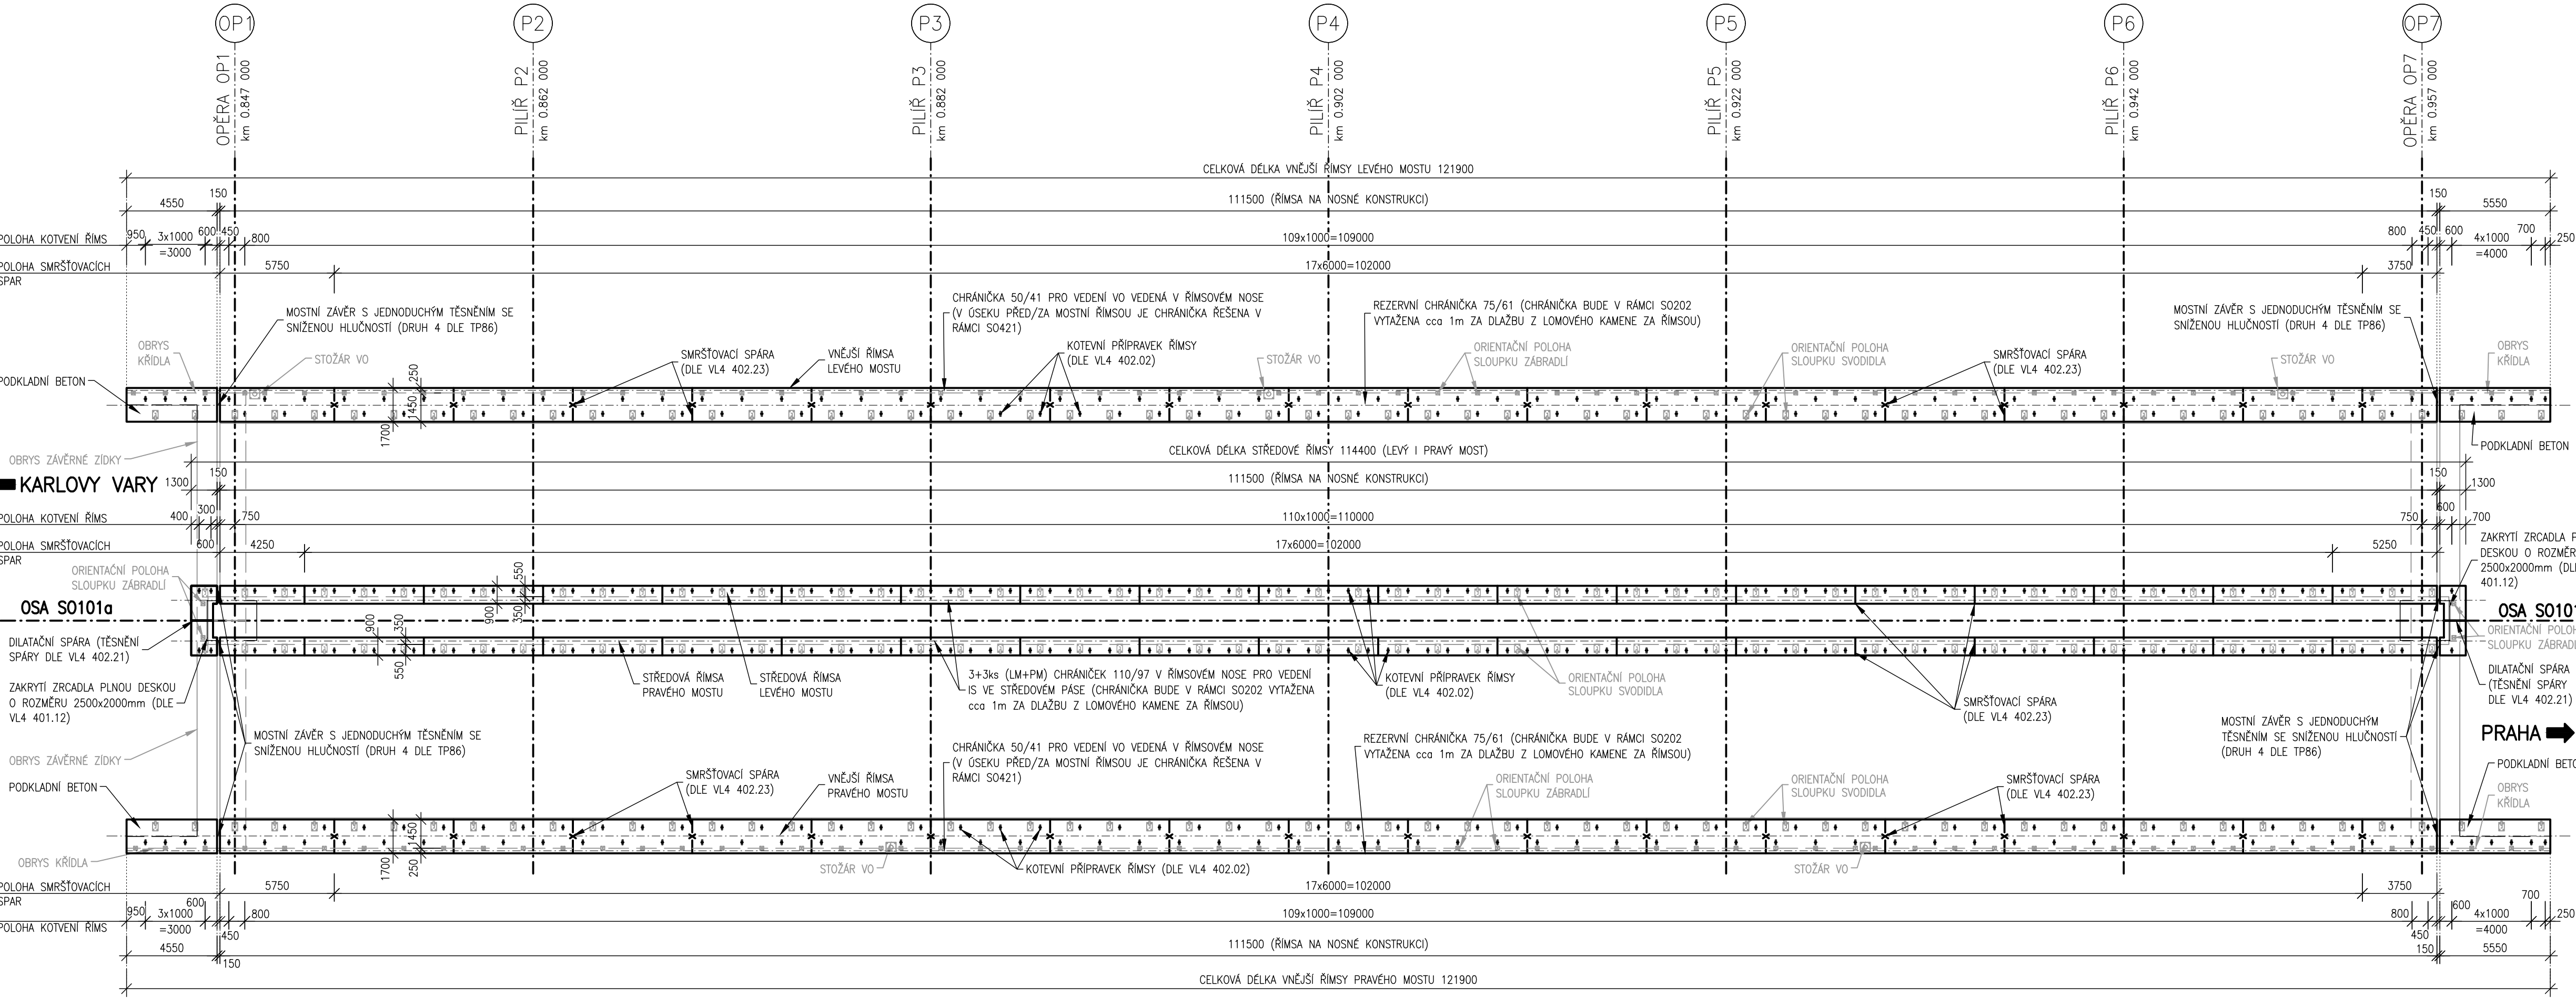


PRÍČNÝ ŘEZ ŘÍMSOU NA NOSNÉ KONSTRUKCI 1:20
VNĚJŠÍ ŘÍMSA

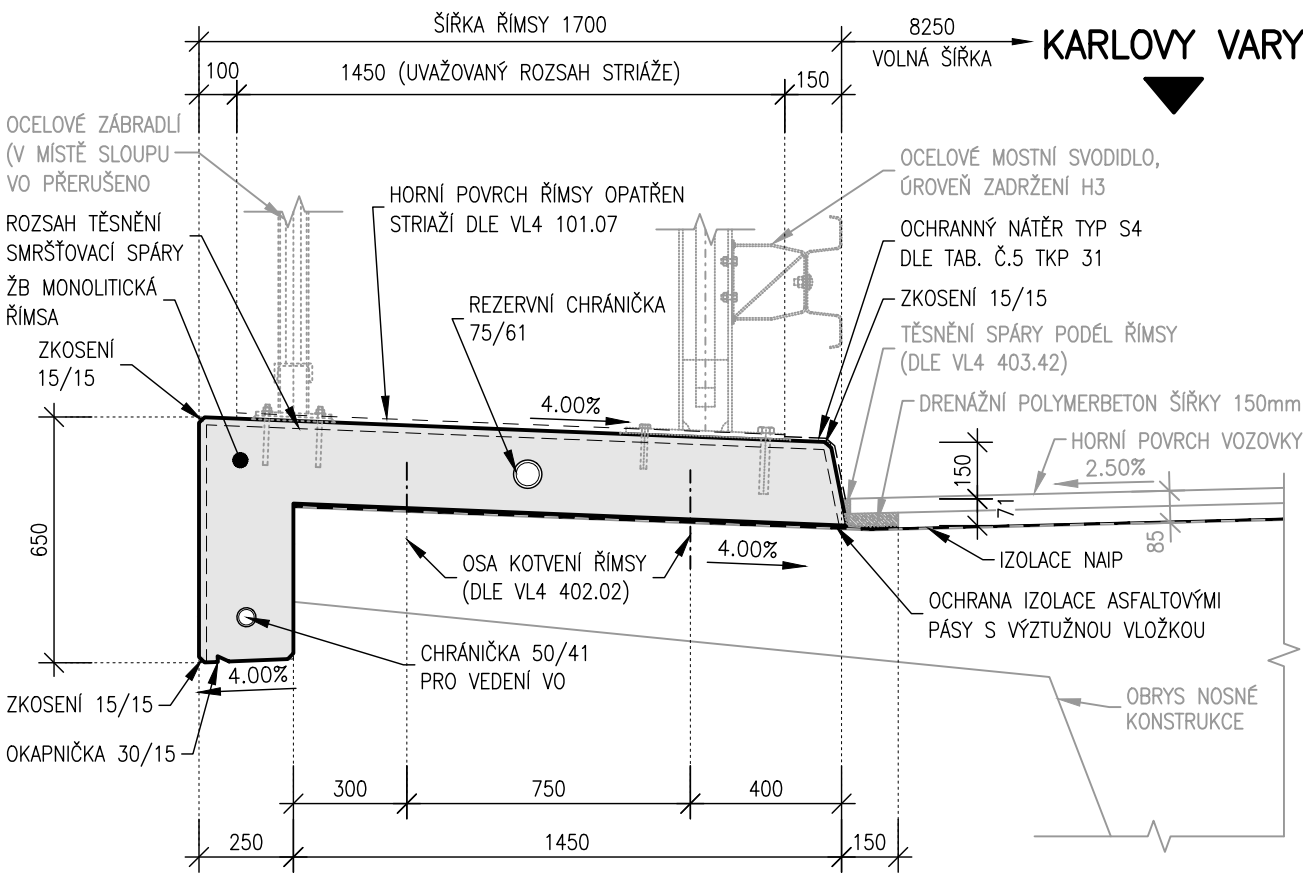


STŘEDOVÁ ŘÍMSA
KARLOVY VARY

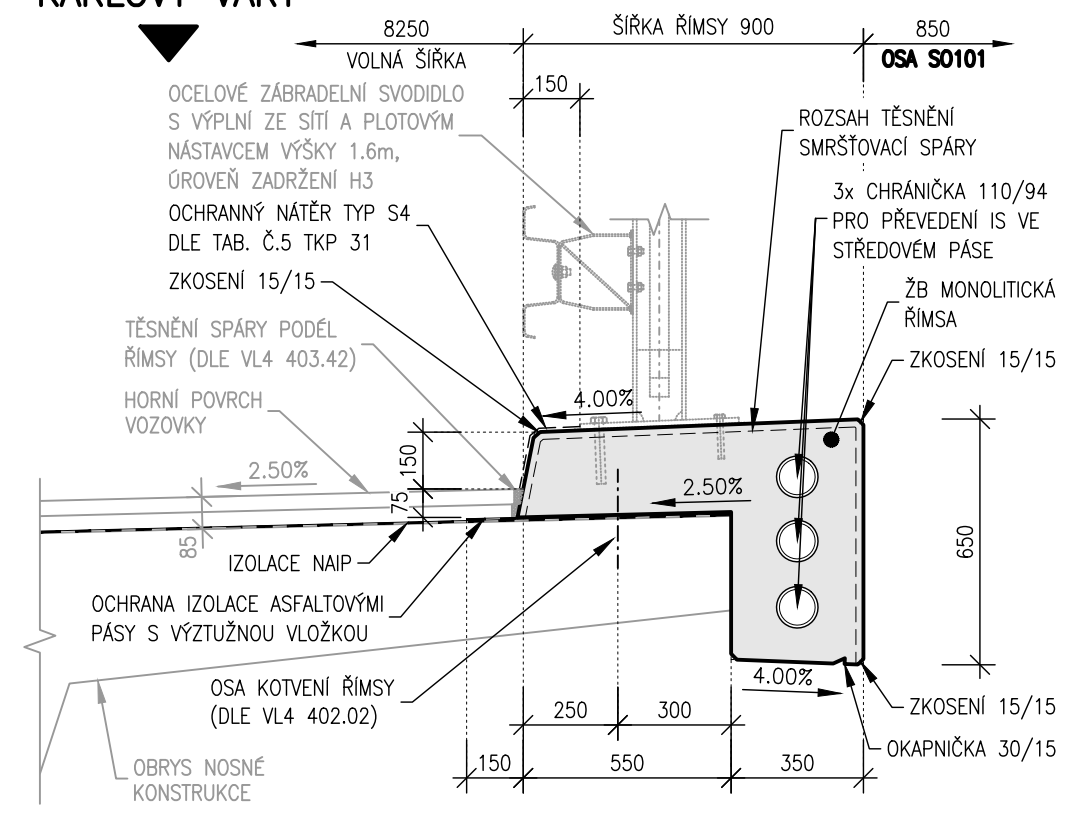


PRÍČNÝ ŘEZ ŘÍMSOU NA MOSTNÍ OPĚŘE 1:20
VNĚJŠÍ ŘÍMSA NA MOSTNÍM KŘÍDLĚ

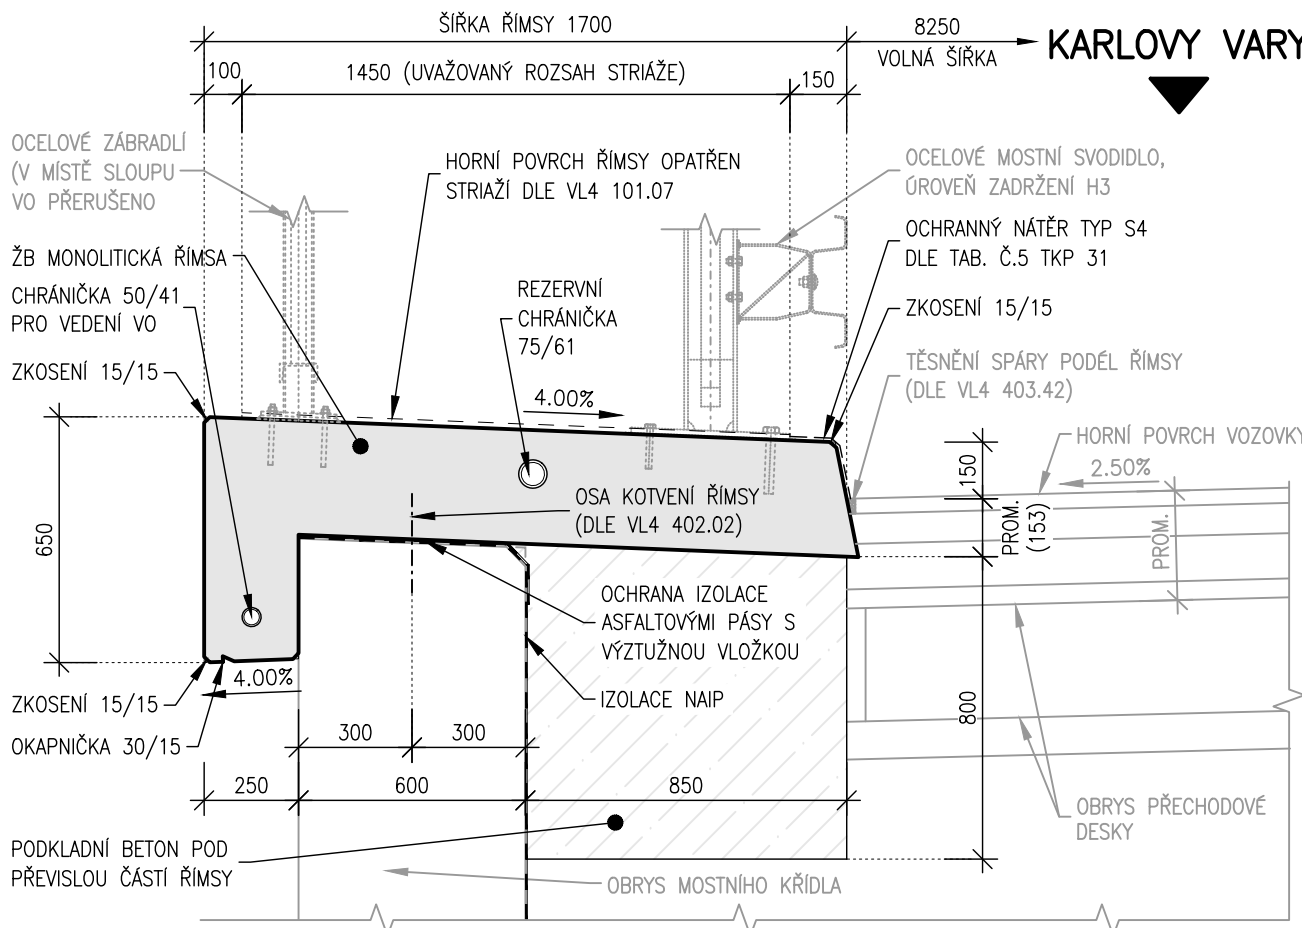


STŘEDOVÁ ŘÍMSA NA ZÁVĚRNÉ ZÍDCE
KARLOVY VARY

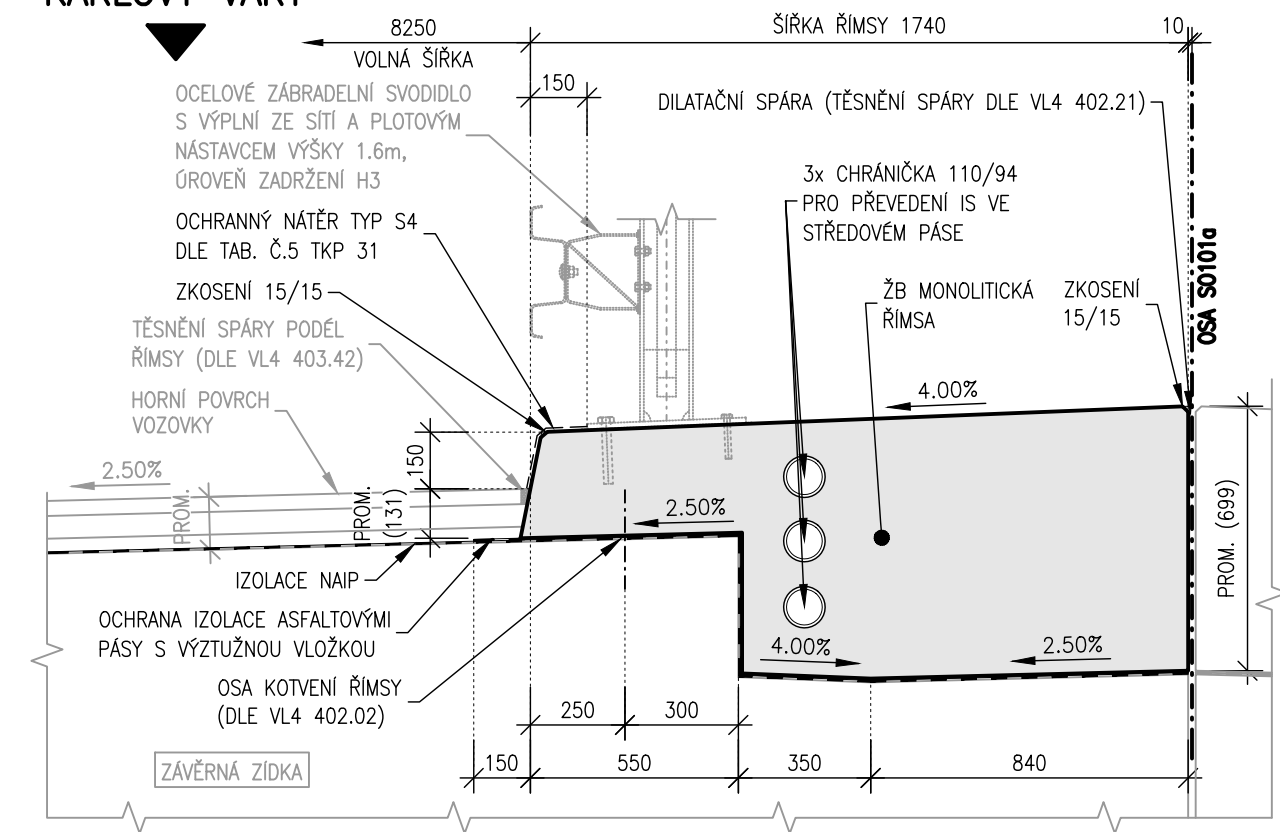


BETONÁŘSKÁ VÝZTUŽ ŘÍMSY NA NOSNÉ KONSTRUKCI 1:20
VNĚJŠÍ ŘÍMSA

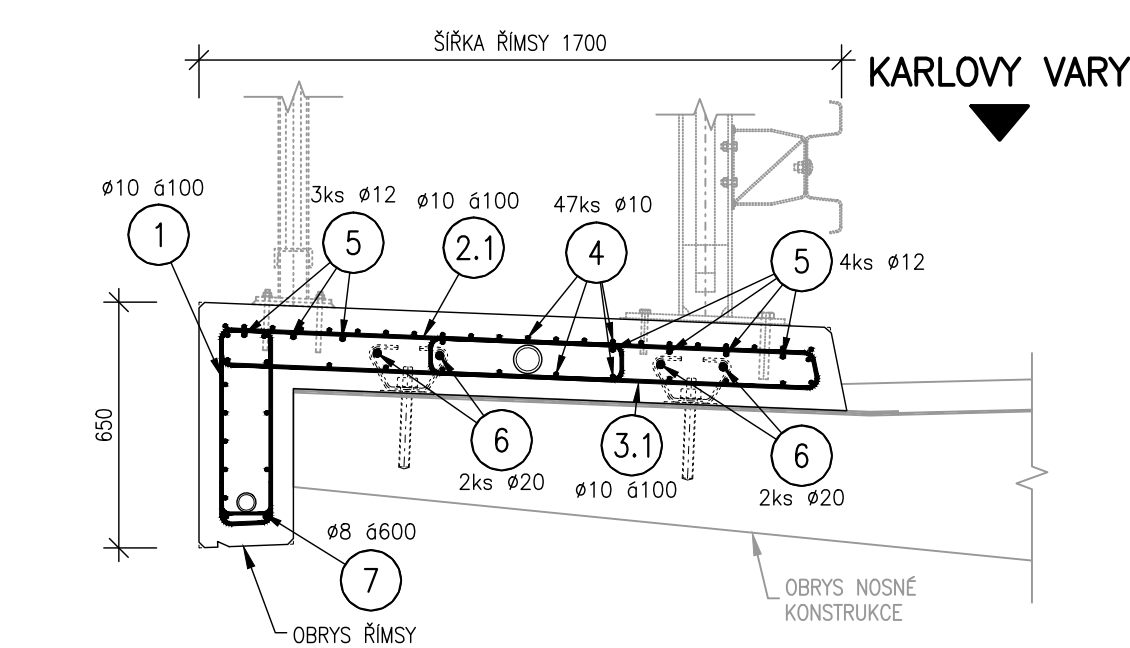


STŘEDOVÁ ŘÍMSA
KARLOVY VARY

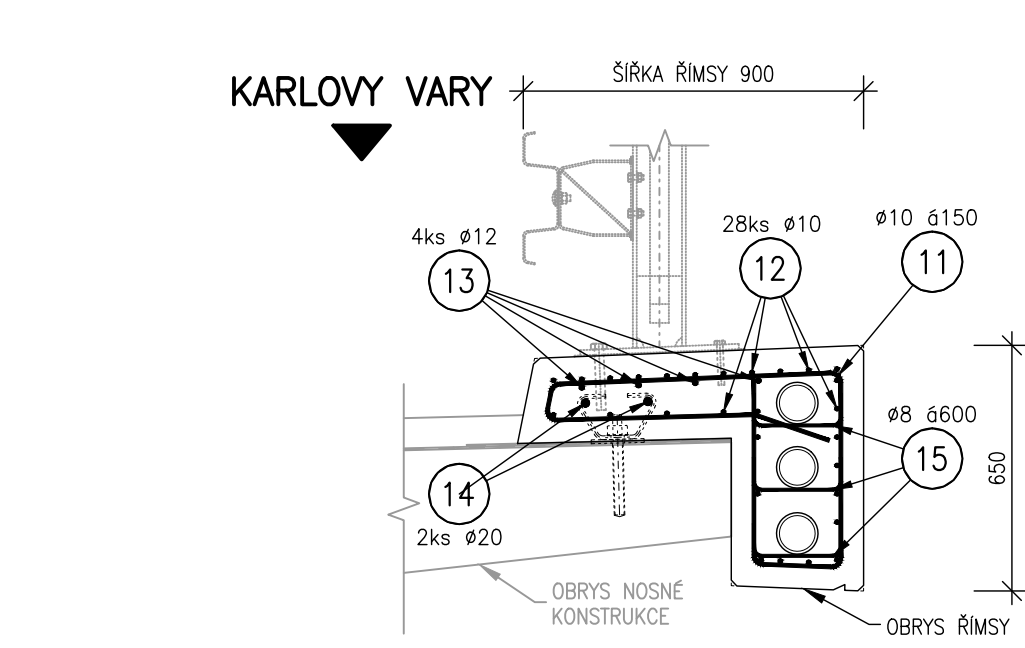

BETONÁŘSKÁ VÝZTUŽ ŘÍMSY NA MOSTNÍ OPĚŘE 1:20
VNĚJŠÍ ŘÍMSA NA MOSTNÍM KŘÍDLĚ

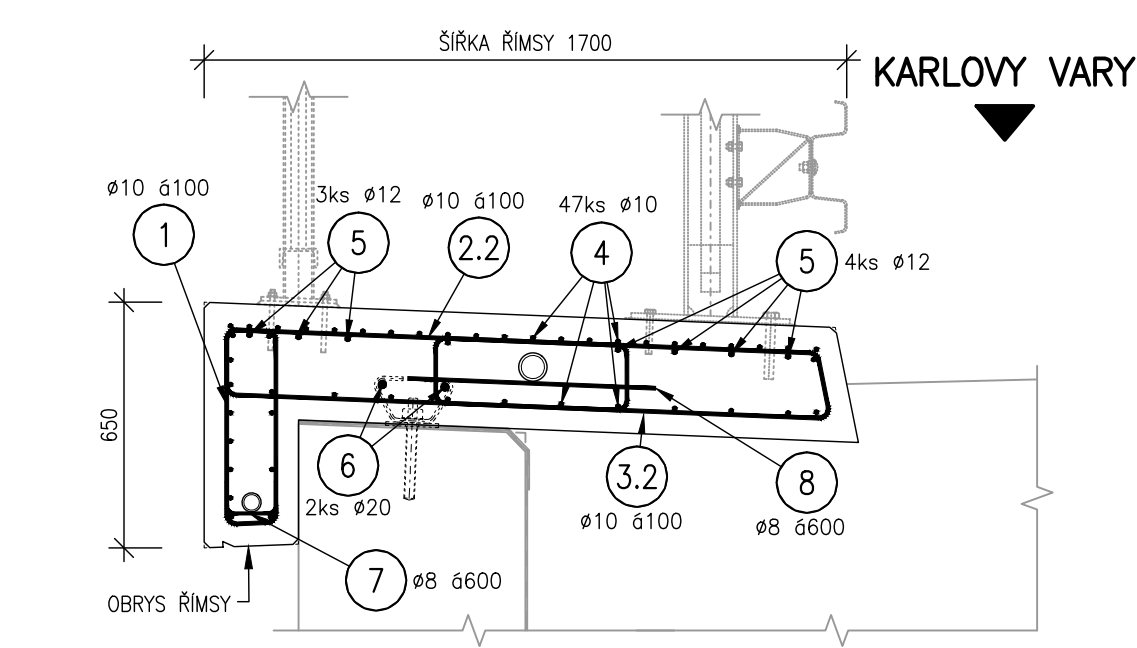


STŘEDOVÁ ŘÍMSA NA ZÁVĚRNÉ ZÍDCE
KARLOVY VARY

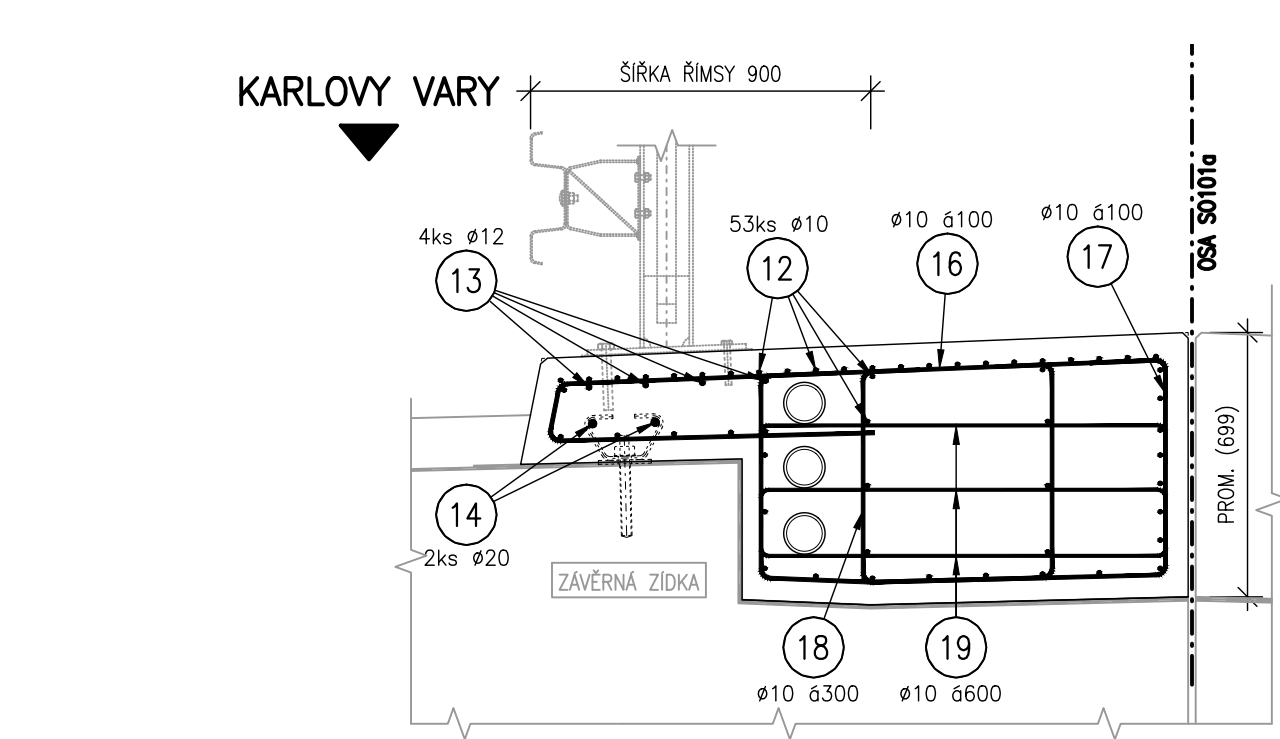


POZNÁMKA:

- PRÍČNÉ ŘEZY S TVAREM A VÝZTUŽENÍM VNĚJŠÍ A STŘEDOVÉ ŘÍMSY JSOU VYKREJLENY POUZE PRO LEVÝ MOST. MOSTNÍ ŘÍMSY PRAVÉHO MOSTU JSOU ŘEŠENY ANALOGICKY.

PRÍČNÝ ŘEZ ŘÍMSOU V MÍSTĚ SLOUPU VO 1:20

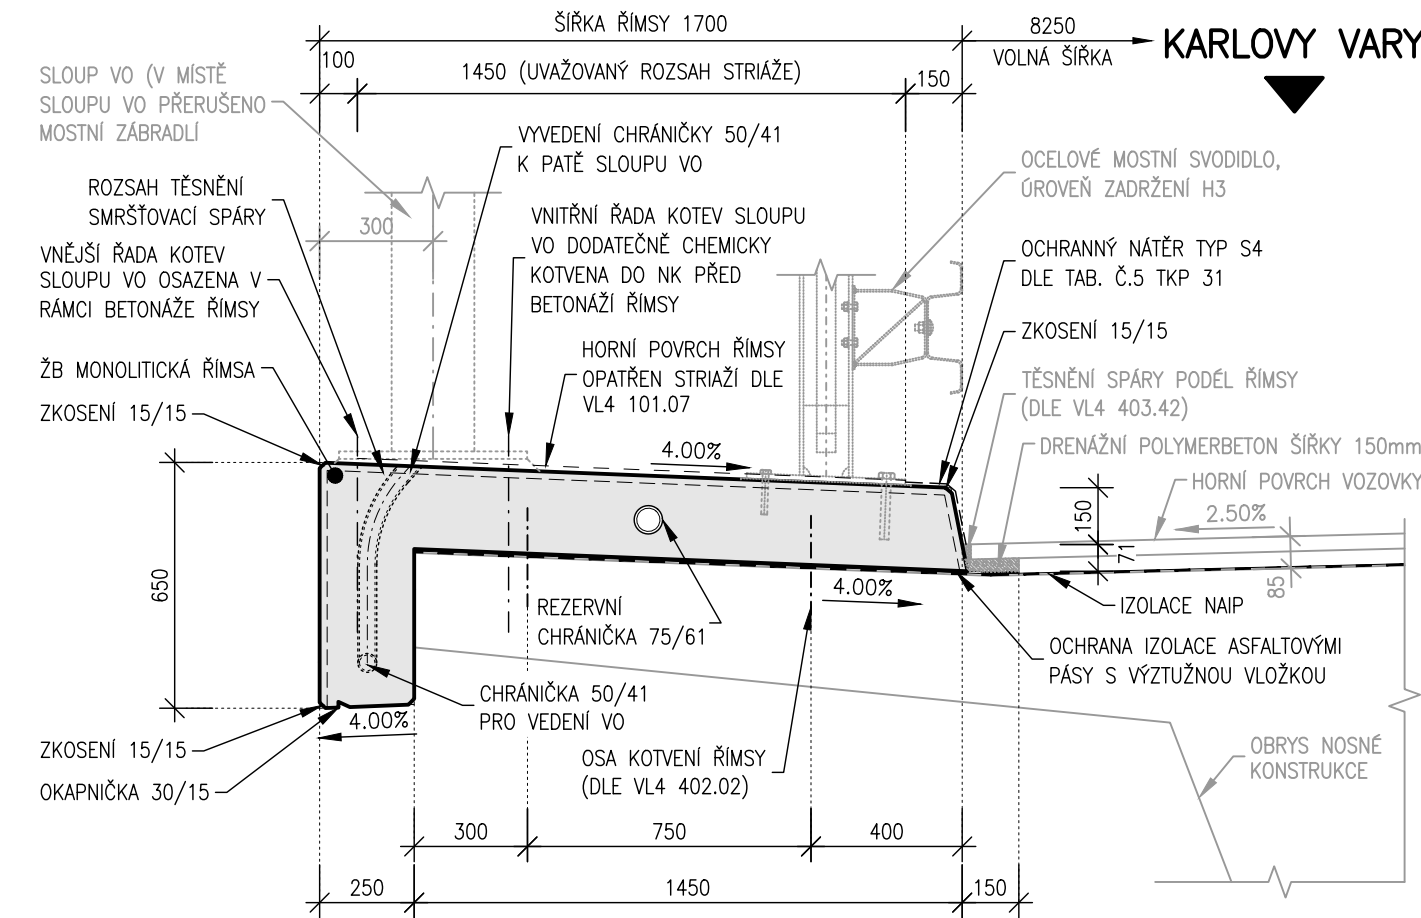

PRŮMĚRY OHYBACÍCH TRNŮ dr:
PRO BETONÁŘSKOU OCEL PODLE ČSN EN 1992-1-1

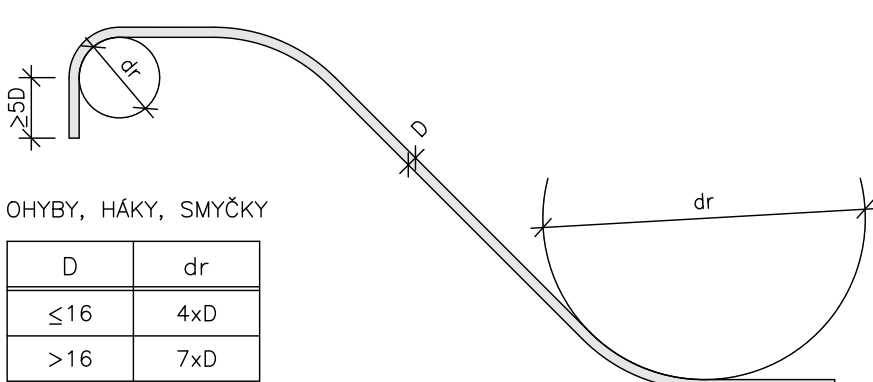

STYKOVÁNÍ VÝZTUŽE

PRŮMĚR VLOŽKY	ø10	ø12	ø16	ø20	ø25	ø28
MIN. DÉLKA STYKU [mm]	500	600	800	1000	1200	1400

MATERIÁLY:

BETON:

(DLE ČSN EN 206+A2 A TKP 18)

PODKLADNÍ BETON POD PŘEVISLOU ČÁSTÍ ŘÍMSY C25/30 XF3

ZB MONOLITICKÁ ŘÍMSA C30/37 XF4

BETONÁŘSKÁ VÝZTUŽ:

(DLE ČSN EN 10080 A ČSN 42 0139)

VÁŽANÁ BETONÁŘSKÁ VÝZTUŽ B500B

KRYTÍ BETONÁŘSKÉ VÝZTUŽE:

MINIMÁLNĚ: 45mm (NEMÍ-LI UVEDENO JINAK)

NOMINÁLNĚ: 55mm (NEMÍ-LI UVEDENO JINAK)

POZNÁMKY:

- SKLON "NÁSLAPNĚ" HRANY ŘÍMSY BUDE UPŘESNĚN DLE POŽADAVKŮ UVEDENÝCH V TPV POUŽITÉHO TYPU SVODIDLA.
- OCHRANA IZOLACE POD ŘÍMSAMI – ASFALTOVÝ PÁS S KOVOVOU VLOŽKOU PŘETAŽENÝ 150mm NA NK A KŘÍDLĚ.
- DO KAŽDÉ ŘÍMSY BUDE OSAZENO 13ks HŘEBŮVÝCH NIVELAČNÍCH ZNAČEK DLE VL4 509.01 PRO SLEDOVÁNÍ TRVALÝCH DEFORMACÍ. SLOUPKY BUDOU UMÍSTĚNY UPROSTŘED POLE A V OSÁCH ULOŽENÍ. CELKOVÝ POČET ZNAČEK ČINÍ 4x13=52ks.
- ROZMÍSTĚNÍ SLOUPKŮ MOSTNÍCH SVODIDEL JE POUZE ORIENTAČNÍ (UVAŽOVÁNA ROZTĚČ SLOUPKŮ 2,0m) A BUDE UPŘESNĚNO DLE POUŽITÉHO TYPU SVODIDLA.
- **MAXIMÁLNÍ POVLÁKNĚNÍ DÉLKA VRTU PRO UKOTVĚNÍ SLOUPKY MOSTNÍHO SVODIDLA:**
 - PRO VNĚJŠÍ ŘÍMSU LEVÉHO A PRAVÉHO MOSTU: 170mm
 - PRO STŘEDOVOU ŘÍMSU LEVÉHO A PRAVÉHO MOSTU: 175mm
- POLOHA SMRŠŤOVACÍCH SPAR A KOTVENÍCH PŘÍPRAVKŮ ŘÍMSY BUDE UPŘESNĚNA DLE ROZTĚČÍ SLOUPKŮ POUŽITÉHO MOSTNÍHO SVODIDLA.
- KOTVENÍ PŘÍPRAVKŮ ŘÍMSY MUSÍ BÝT CERTIFIKOVÁN DO BETONU S TRHLINAMI DLE ETAG. KOTVENÍ ŘÍMS DO NOSNÉ KONSTRUKCE MUSÍ ODPOVÍDAT POŽADAVKŮM TPV ZHOTOVITĚLE VYBRANÉHO SVODIDLA.
- TĚSNĚNÍ SMRŠŤOVACÍCH SPAR BUDE PROVEDENO DLE VL4 402.23 (ALTERNATIVA 1). HŘEBŮVÉ NIVELAČNÍ ZNAČKY BUDOU OSAZENY DLE VL4 509.01. KOTVA ŘÍMSY VE VÝVRTU BUDE PROVEDENA DLE VL4 402.2.
- KOTVENÍ STOŽÁRU VO BUDE UPŘESNĚNO DLE POŽADAVKŮ A MOŽNOSTI DODAVATELE. PŘEDPOKLADÁME KOTVENÍ STOŽÁRU VO V RAMCI PDPS.
- VNĚJŠÍ RADA KOTEV: 2xM24 OSAZENÉ V RAMCI BETONÁŽE MOSTNÍ ŘÍMSY
- VNITŘNÍ RADA KOTEV: 2xM24 DODATEČNĚ CHEMICKY UKOTVENÉ DO NK PŘED BETONÁŽÍ ŘÍMSY
- PŘÍDAVA BETONÁŘSKÁ VÝZTUŽ V MÍSTĚ STOŽÁRU VO BUDE UPŘESNĚNA V RAMCI NAVAZUJÍCÍHO STUPNĚ DOKUMENTACE (RDS) DLE POŽADAVKŮ DODAVATELE STOŽÁRU.
- PŘEDPOKLAD KONTINUITNÍ BETONÁŽE ŘÍMSY.
- MINIMÁLNÍ POČET DÍLŮVÝCH PODOLEŽEK BETONÁŘSKÉ VÝZTUŽE JE 4ks/m².

ODHAĐOVANÁ PARAMETRICKÁ SPOTŘEBA
BETONÁŘSKÉ VÝZTUŽE: 160 kg/m³

D

PDPS

OBJEDNATEL	ŘEDITELSTVÍ SILNIC A DÁLNIC s. p. ČERČANSKÁ 12, 140 00 PRAHA 4 STAVBU ZAJIŠŤUJE: SPRÁVA KARLOVY VARY, ZÁVODNÍ 82, 360 06 KARLOVY VARY	
------------	--	--

ZHOTOVITEL	Morava - RD velké zakázky FIDIC 2023 VEDOUČÍ SDRUŽENÍ: VIAPONT s.r.o., VODNÍ 13, 602 00 BRNO	ČLENOVÉ SDRUŽENÍ: Stráský, Huší a partneři s.r.o. SHB, akciová společnost DOPRAVNÍ PROJEKT, Ostrava a.s. PK OSSENDORF s.r.o. G-Consult, spol. s r.o. Mott MacDonald CZ, spol. s r.o. METROPROJEKT Praha a.s.
------------	--	---

HLAVNÍ PROJEKTANT	VIAPONT s.r.o. VODNÍ 13, 602 00 BRNO	
HLAVNÍ INŽENÝR PROJEKTU	ING. IVO FISCHER	ČÍSLO ZAKÁZKY: 2550-01

D.1.2.1 SO202 Most na sil. I/6 v km 0,900

SOUŘADNICOVÝ SYSTÉM: S-JTSK	VÝŠKOVÝ SYSTÉM: Bpv	VEDOUČÍ PROJEKTANT: ING. IVAN KUŠAK	ZODPOVĚDNÝ PROJEKTANT: ING. JAN MACÁK	VYPRACOVAL: ING. JAN MACÁK	KONTROLOVAL: ING. IVAN KUŠAK	KRAJ: KARLOVARSKÝ	OBEC: KARLOVY VARY, ANĚLSKÁ HORA	STUPEŇ: PDPS	DATUM: ŘÍJEN 2025
NÁZEV STAVBY: D6 KARLOVY VARY - OLŠOVÁ VRATA									FORMÁT: 10 A4
NÁZEV PŘÍLOHY: TVAR A VÝZTUŽ ŘÍMS									MĚŘÍTKO: 1:200, 20
									Č. ZAKÁZKY: 2550-01
									ARCHIVNÍ Č.
									Č. SOUPRAVY:
									Č. PŘÍLOHY: 23